


Diagrama de um poço de visita com cotas e identificação de pontos:

- Cota da geratriz inferior do tubo de chegada**: Indica a cota da base do tubo de chegada.
- Cota da geratriz inferior do tubo de chegada**: Indica a cota da base do tubo de chegada.
- PV**: Identificação do ponto de visita.
- Cota do topo do poço de visita**: Indica a cota da borda superior do poço.
- Número do PV**: Identificação numérica do ponto de visita.
- Cota da geratriz inferior do tubo**: Indica a cota da base do tubo.

01 - Quando não indicado, medidas em metros;
02 - Rede coletora, ramais condominiais e emissário por gravidade com tubulação em PVC tipo Coletor Público
03 - Emissário por recalque com tubulação em PEAD PE-100 PN-10 DE-180
04 - Emissário pressurizado por gravidade com tubulação em PVC DEFoFo conforme NBR-7665/2020.

PRONCHA	01/12	ASSUNTO	CONDOMÍNIO RECANTO DAS CEREJEIRAS PLANTA DE GERAL DE ESGOTO
	ELABORADO POR: TÚLIO LINS E ISABELLE FRANÇA REVISÃO: 01 DATA: 12/03/2026		

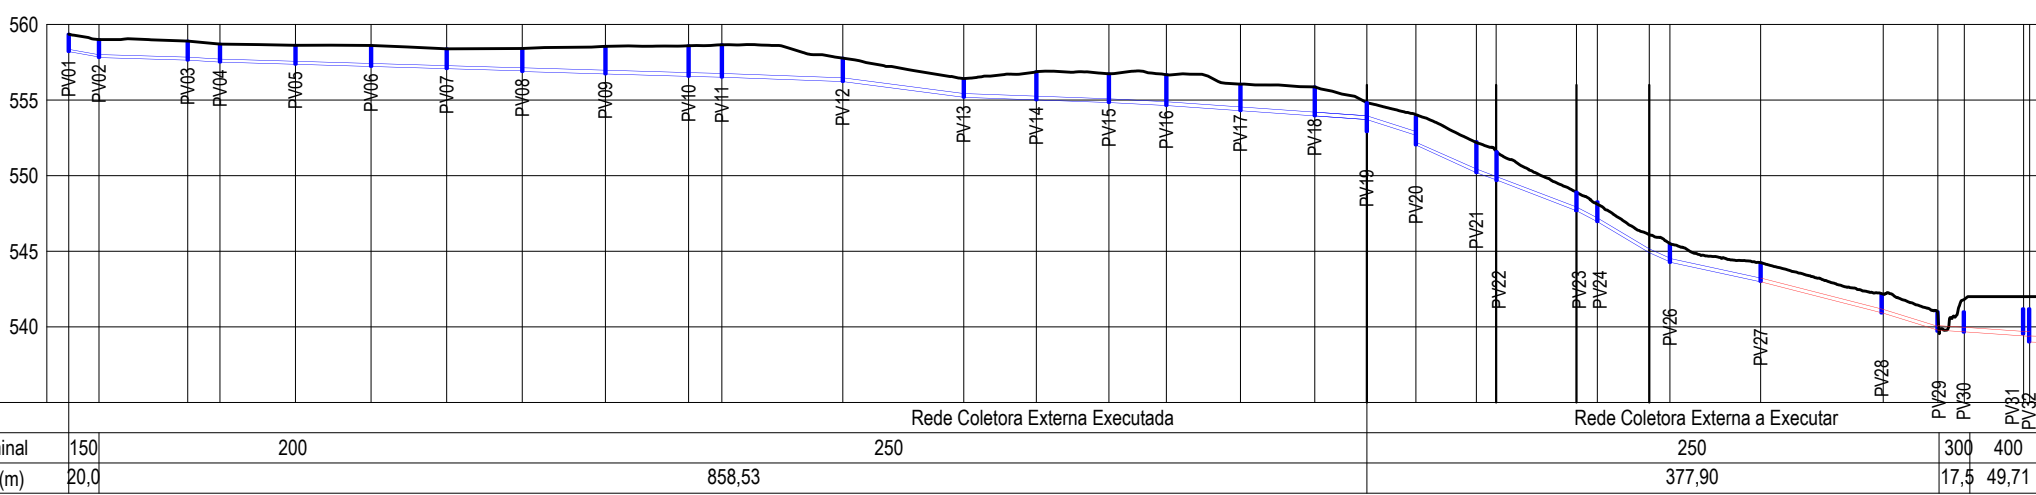