




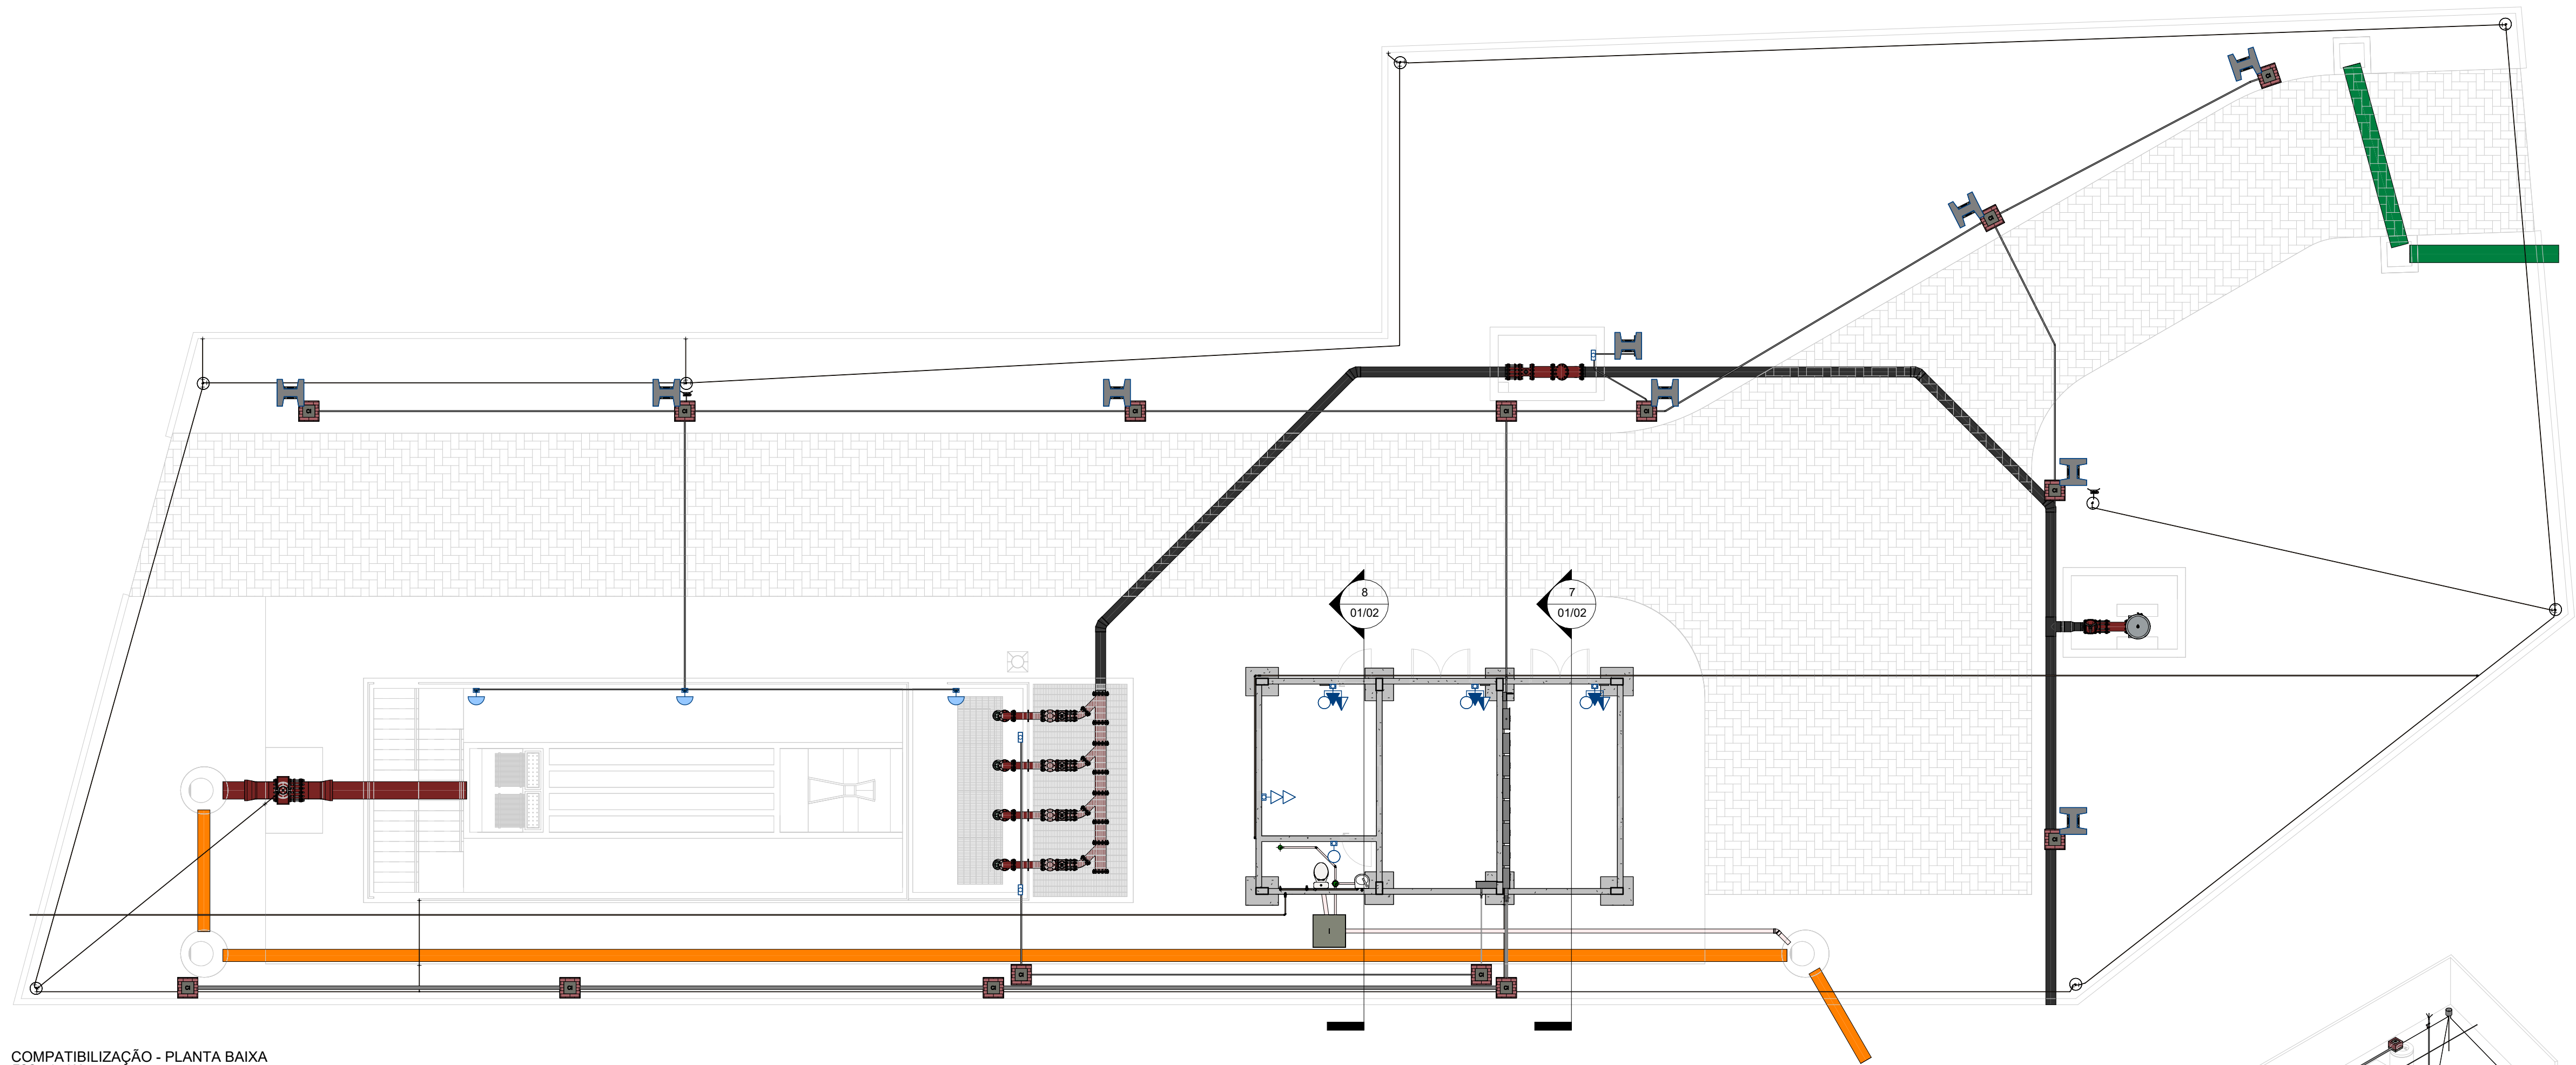


COMPATIBILIZAÇÃO - PLANTA BAIXA
ESC.: 1:100

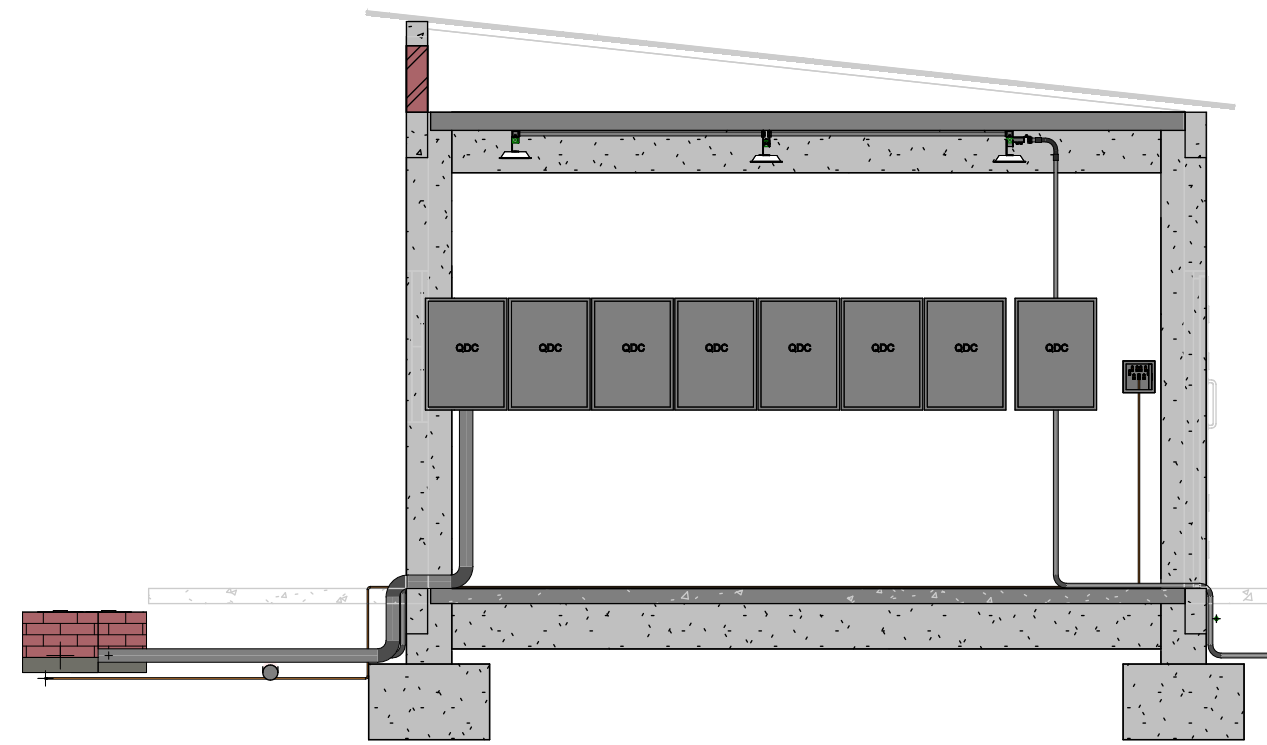


CORTE - SALA DE COMANDO
ESC.: 1:50

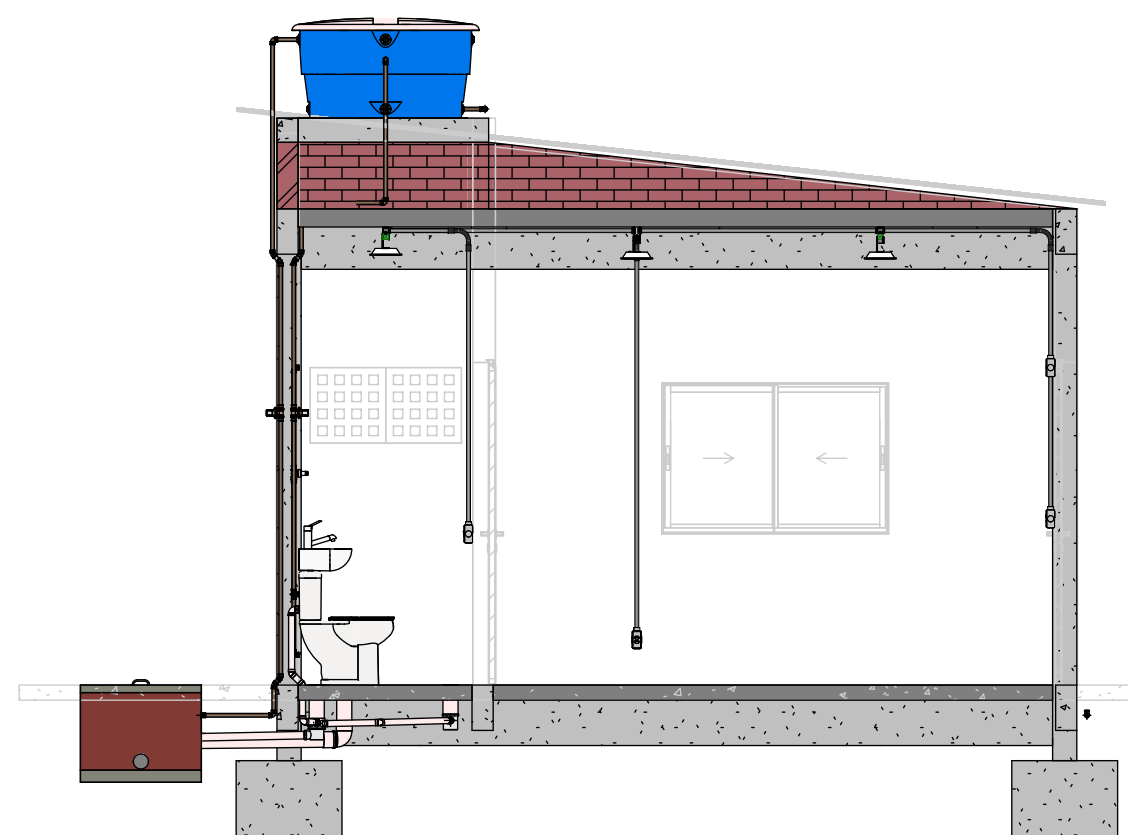


CORTE - SALA DO OPERADOR + BANHEIRO
ESC.: 1:50

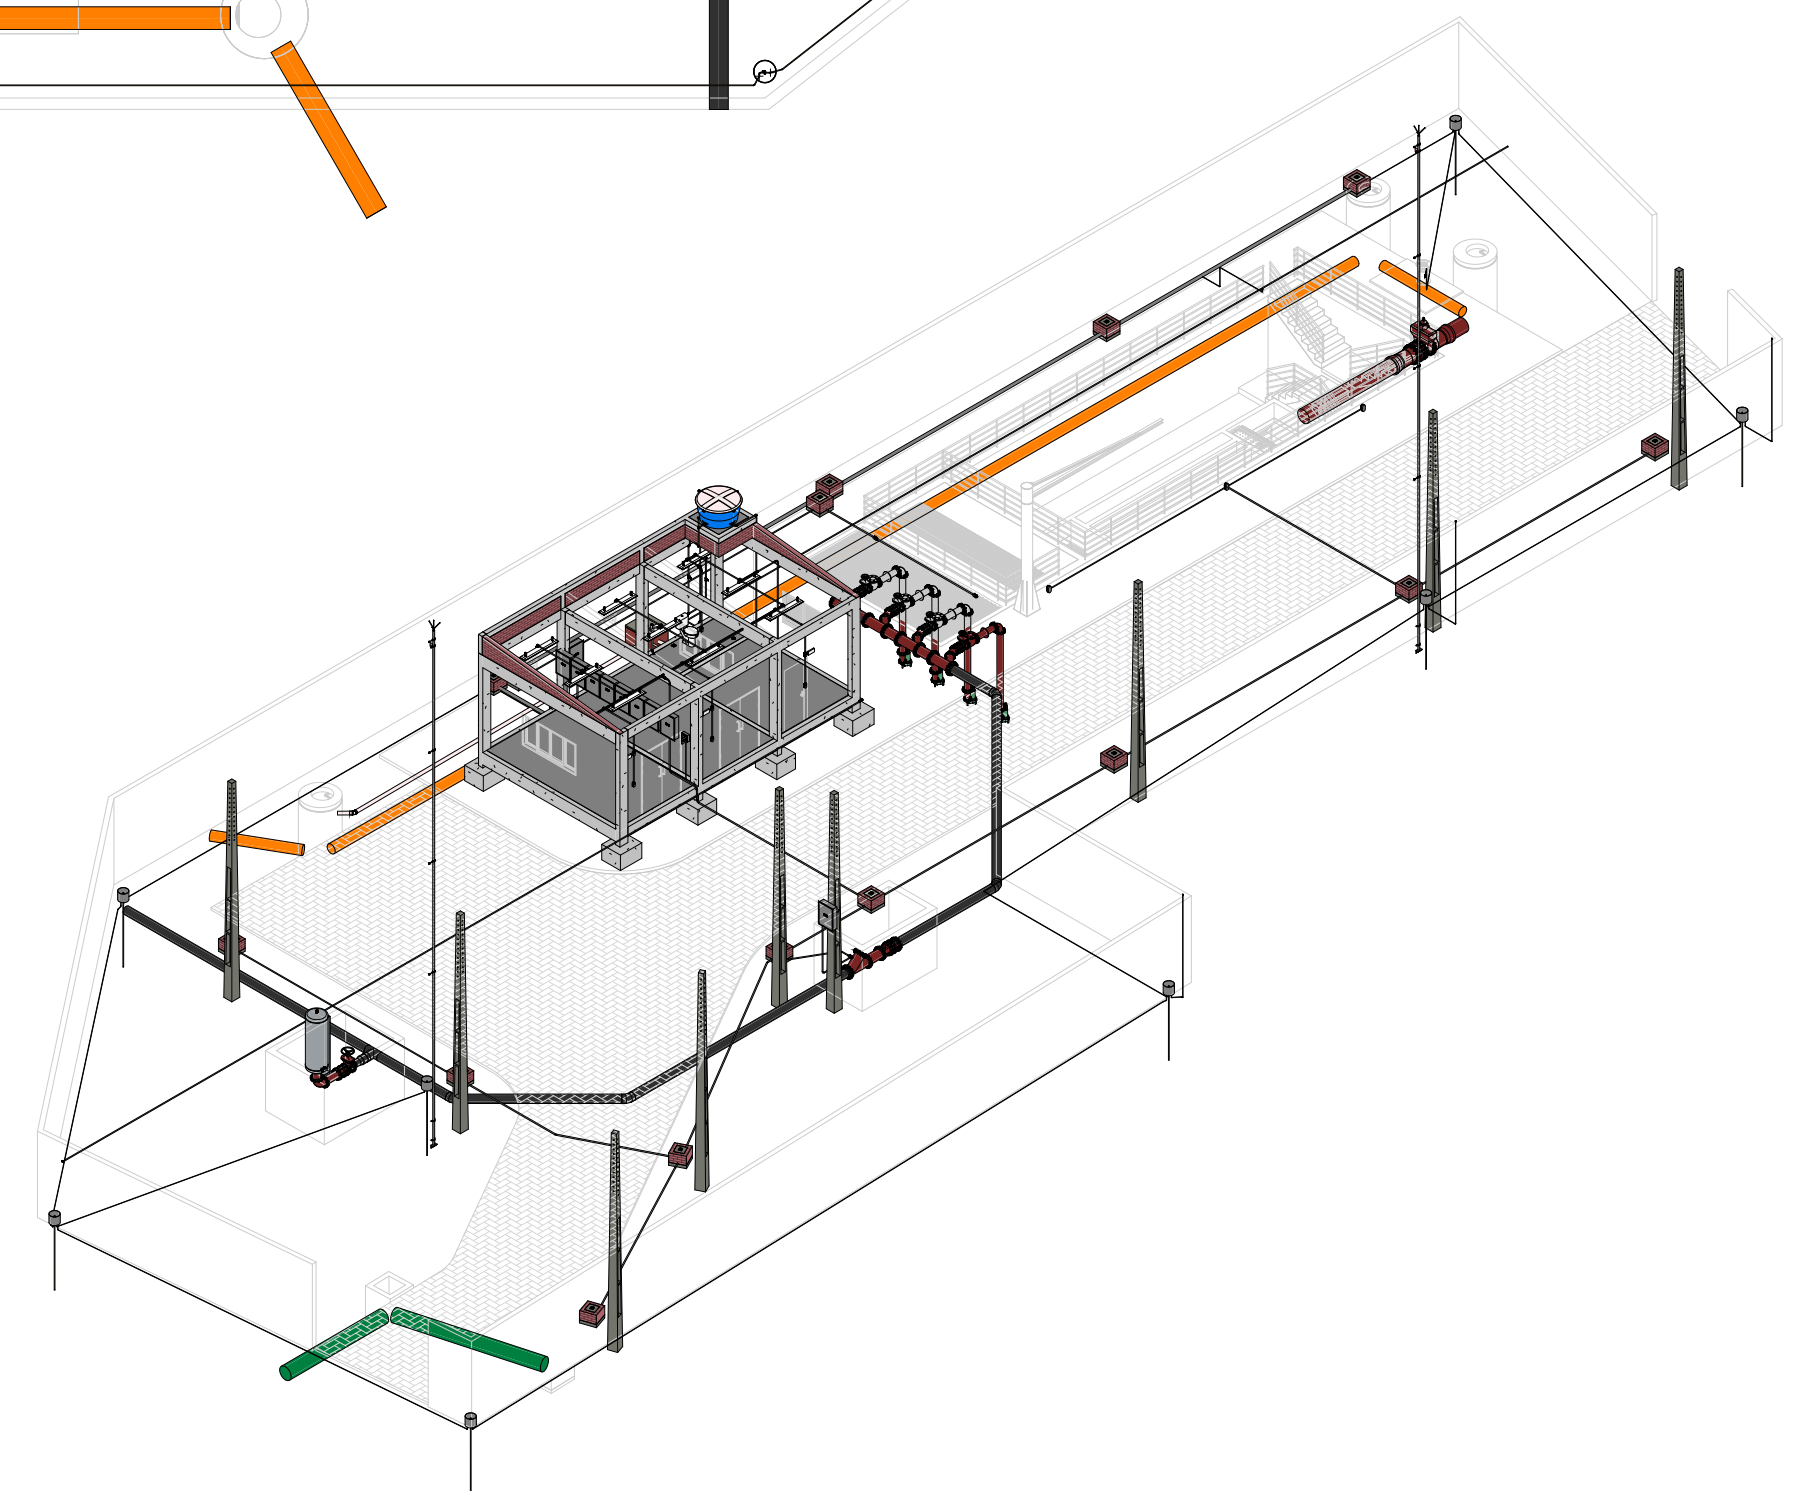


ISOMÉTRICO - EEE DEFINITIVA CEREJEIRAS
ESC.: 1:50

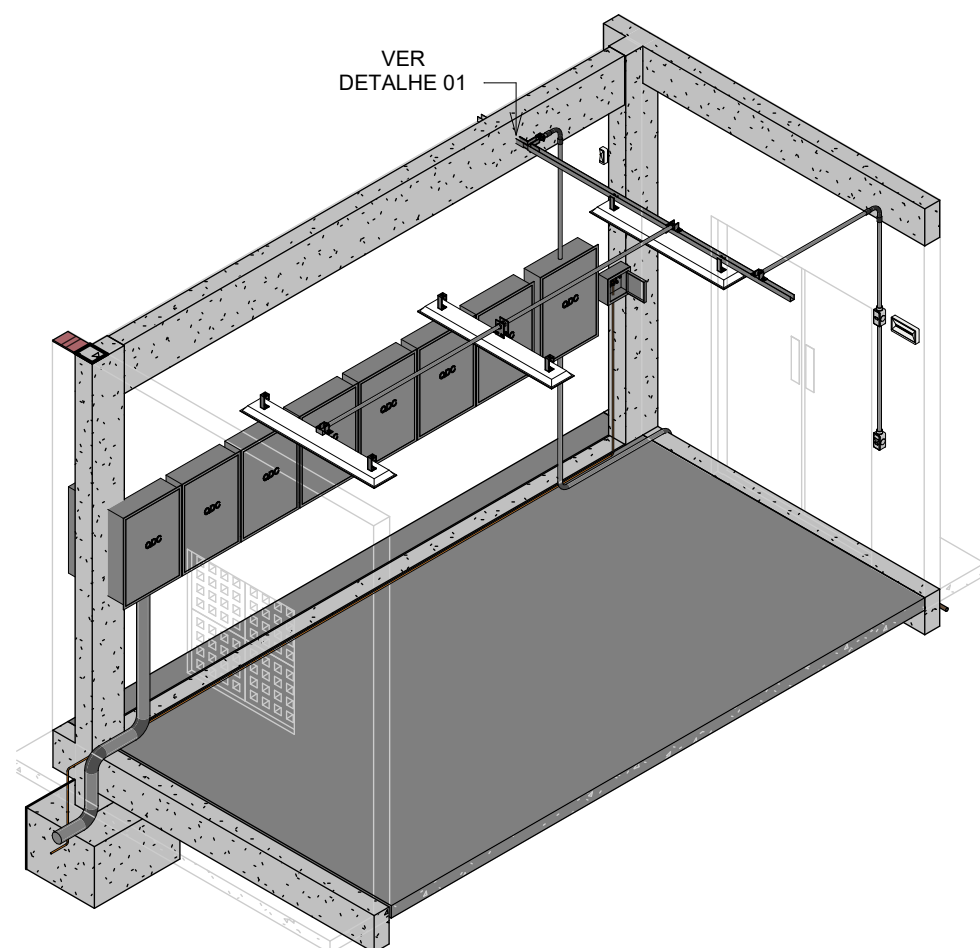


ISOMÉTRICO - SALA DE COMANDO
ESC.: 1:50

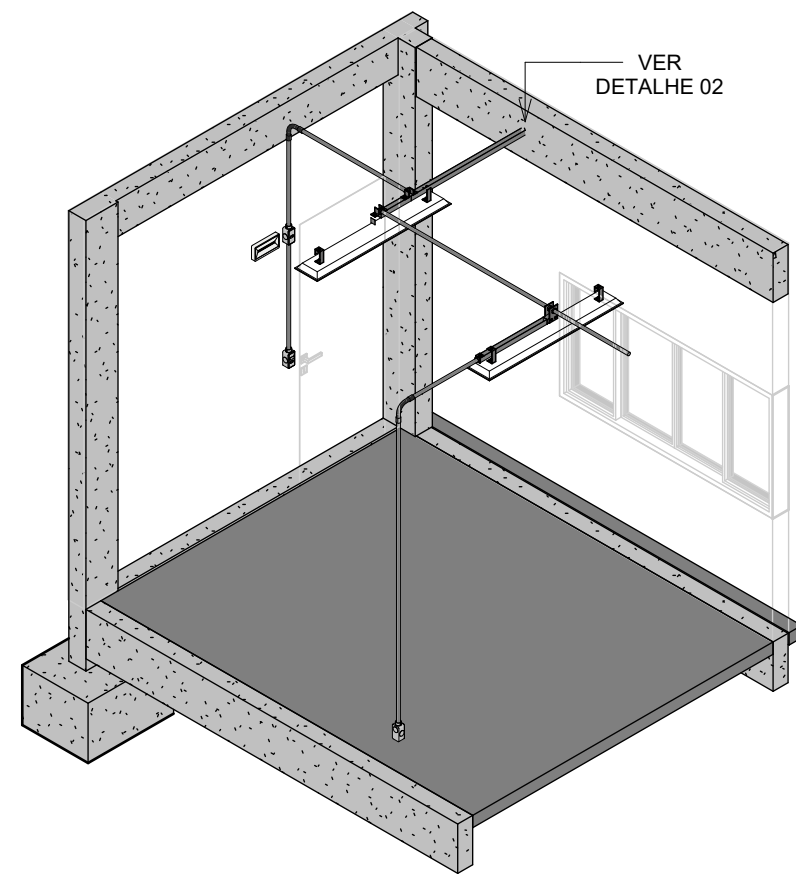


ISOMÉTRICO - SALA DO OPERADOR
ESC.: 1:50

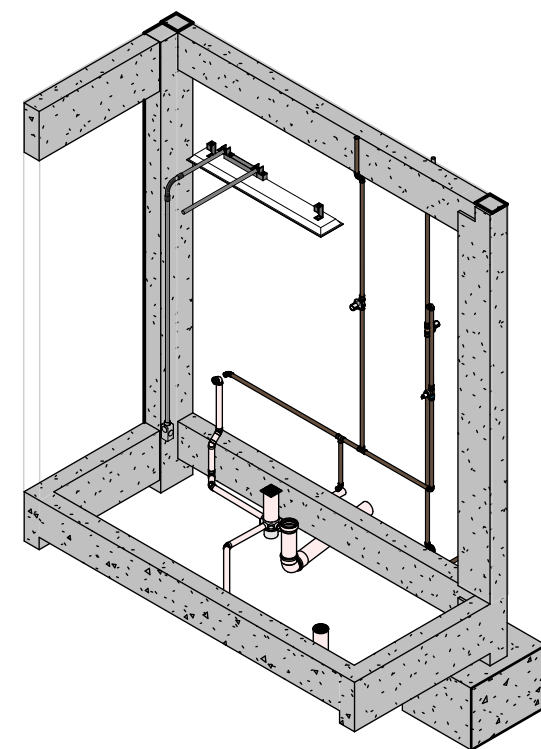

ISOMÉTRICO - BANHEIRO
ESC.: 1:50

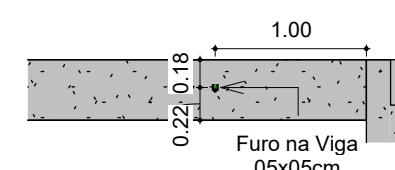

DETALHE 01
ESC.: 1:50

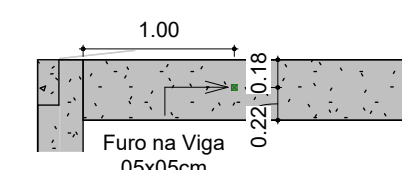

DETALHE 02
ESC.: 1:50

NOTAS GERAIS - COMPATIBILIZAÇÃO

- Os projetos especializados (hidrossanitário, estrutural, elétrico e SPDA) contêm todas as informações técnicas necessárias. Este projeto de compatibilização tem função visual e orientativa, auxiliando na identificação de possíveis interferências entre as disciplinas durante a execução da obra.
- Os projetos Elétrico e SPDA, não contêm as cotas de locação dos equipamentos. Assim, as plantas baixas destes sistemas foram incluídas no projeto de compatibilização para orientar a execução em obra.




COMPATIBILIZAÇÃO


CÓPIA DIGITAL VÁLIDA

PRONCHIA
01/02 ASSUNTO
VM - EEE NOVO MUNDO - COMPATIBILIZAÇÃO -
PLANTA BAIXA, VISTAS E DETALHAMENTOS
ELABORADO POR: ISABELLE FRANÇA E TÚLIO LINS
REVISÃO: 00 DATA: 07/10/2025



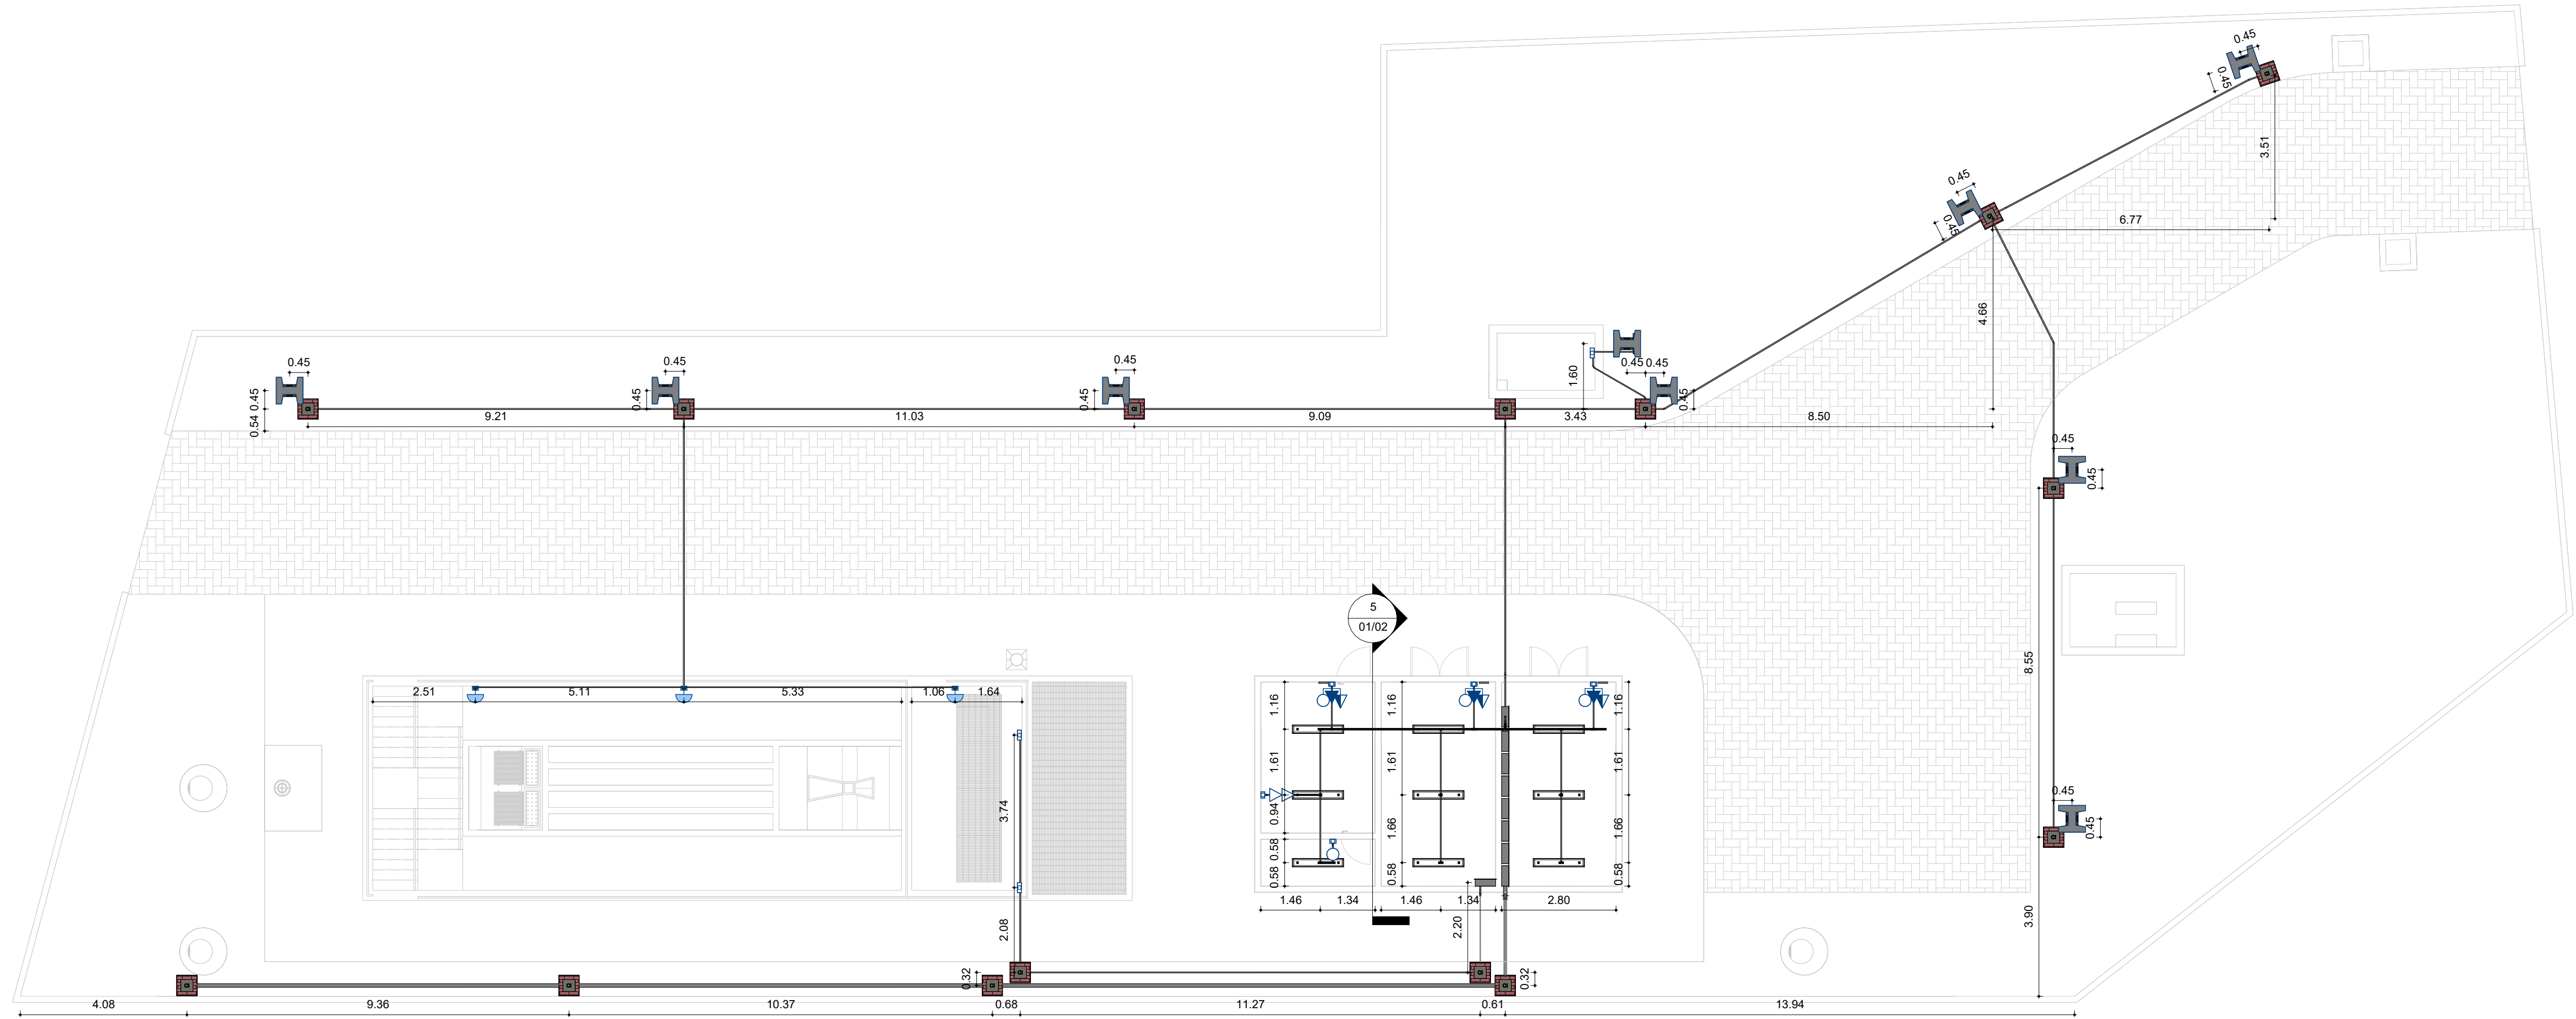

ELÉTRICO - PLANTA BAIXA
ESC.: 1 : 100

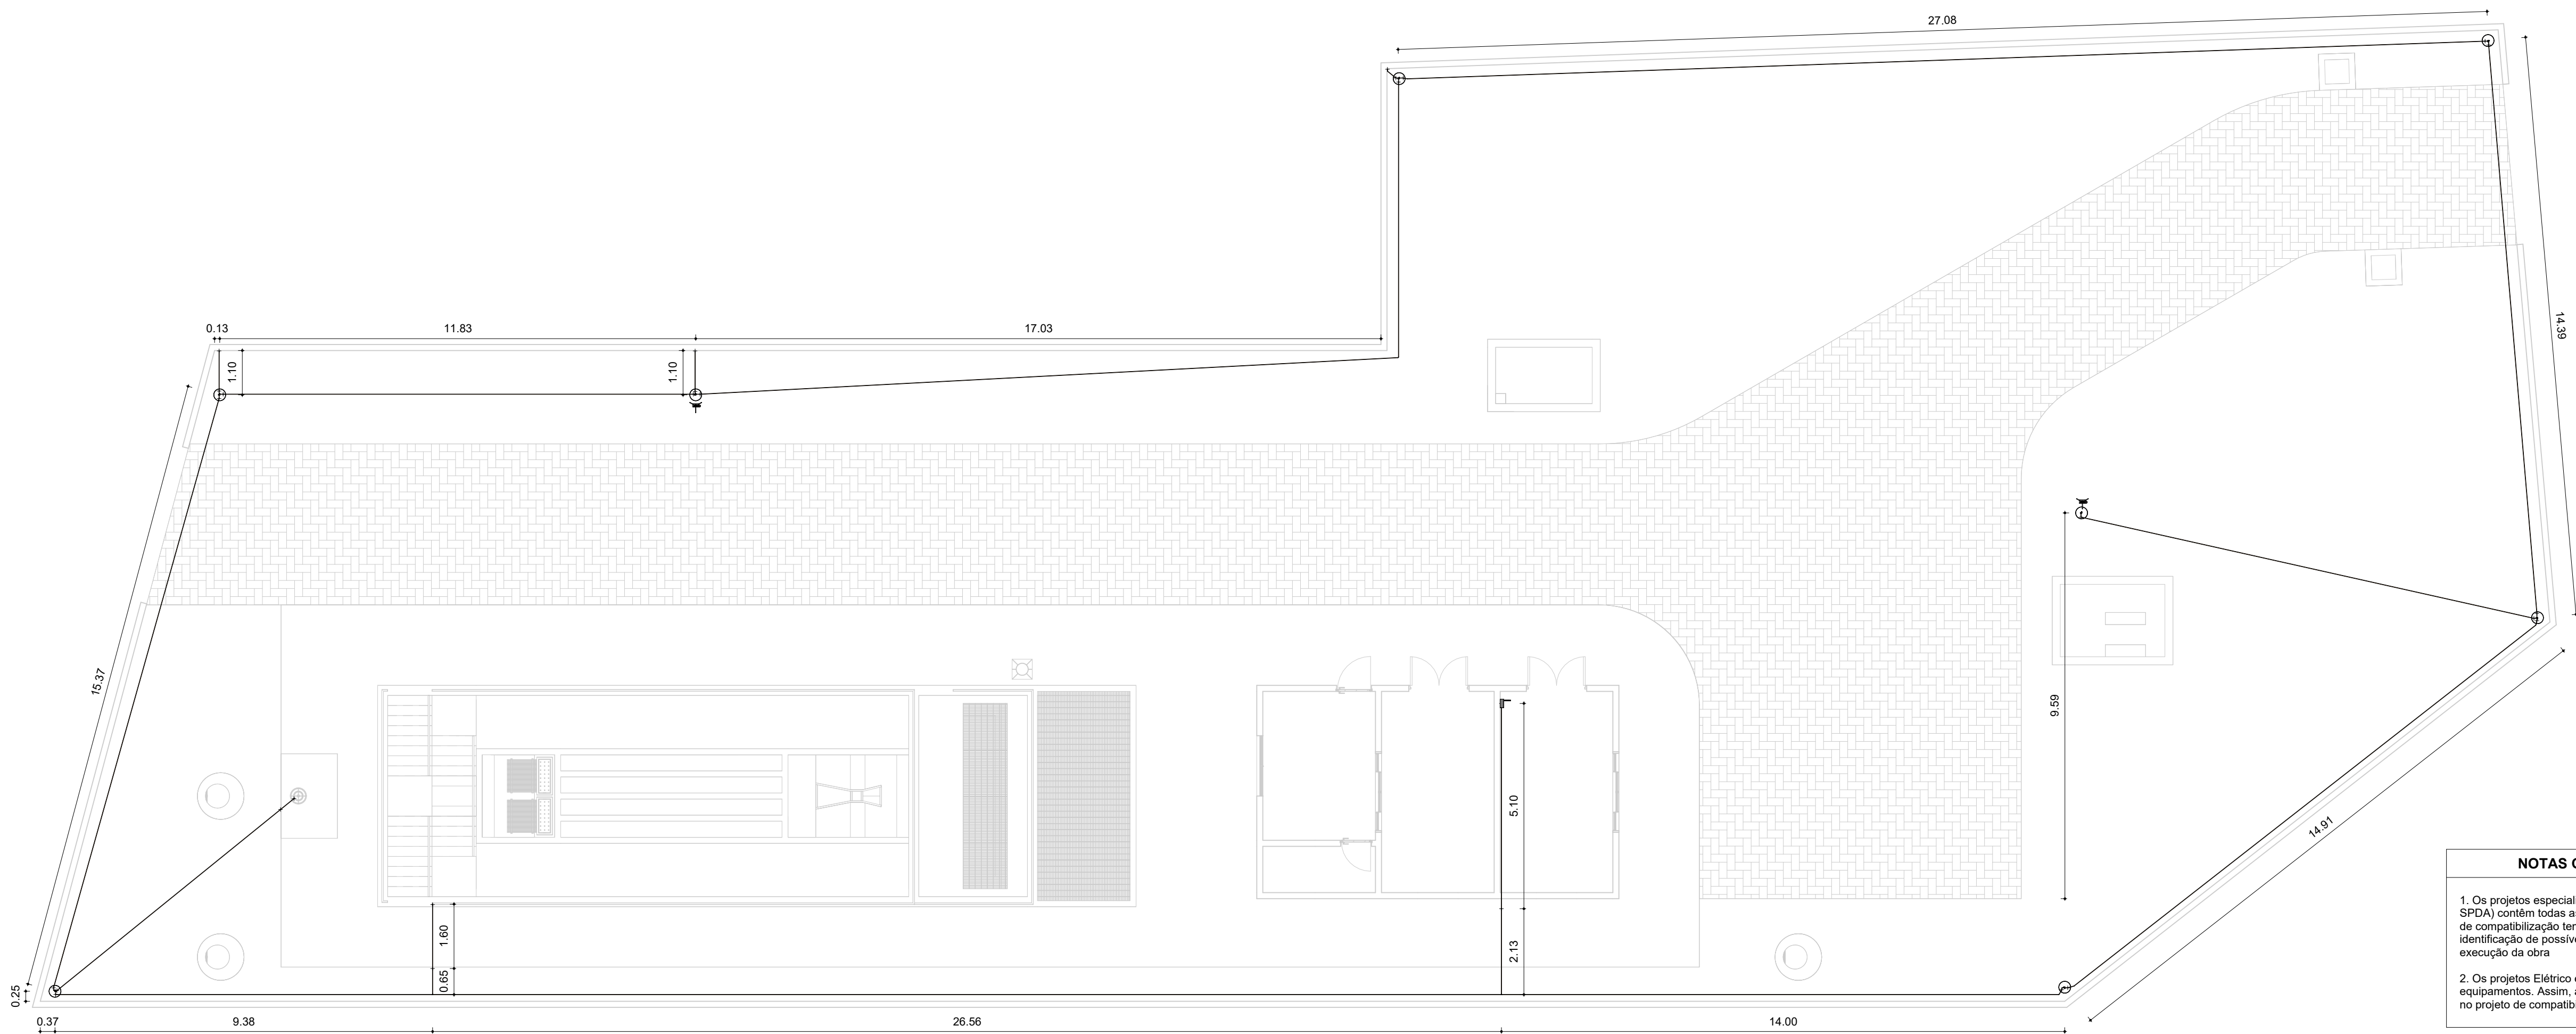

SPDA - PLANTA BAIXA
ESC.: 1 : 100

NOTAS GERAIS - COMPATIBILIZAÇÃO

1. Os projetos especializados (hidrossanitário, estrutural, elétrico e SPDA) contêm todas as informações técnicas necessárias. Este projeto de compatibilização tem função visual e orientativa, auxiliando na identificação de possíveis interferências entre as disciplinas durante a execução da obra.
2. Os projetos Elétrico e SPDA, não contêm as cotas de locação dos equipamentos. Assim, as plantas baixas destes sistemas foram incluídas no projeto de compatibilização para orientar a execução em obra.



COMPATIBILIZAÇÃO

CÓPIA DIGITAL VÁLIDA

PRIMEIRA	02/02	ASSUNTO	VM - EEE NOVO MUNDO - COMPATIBILIZAÇÃO - PLANTAS BAIXAS (ELÉTRICO E SPDA)
		ELABORADO POR:	ISABELLE FRANÇA E TÚLIO LINS
		REVISÃO:	00
		DATA:	07/10/2025

