
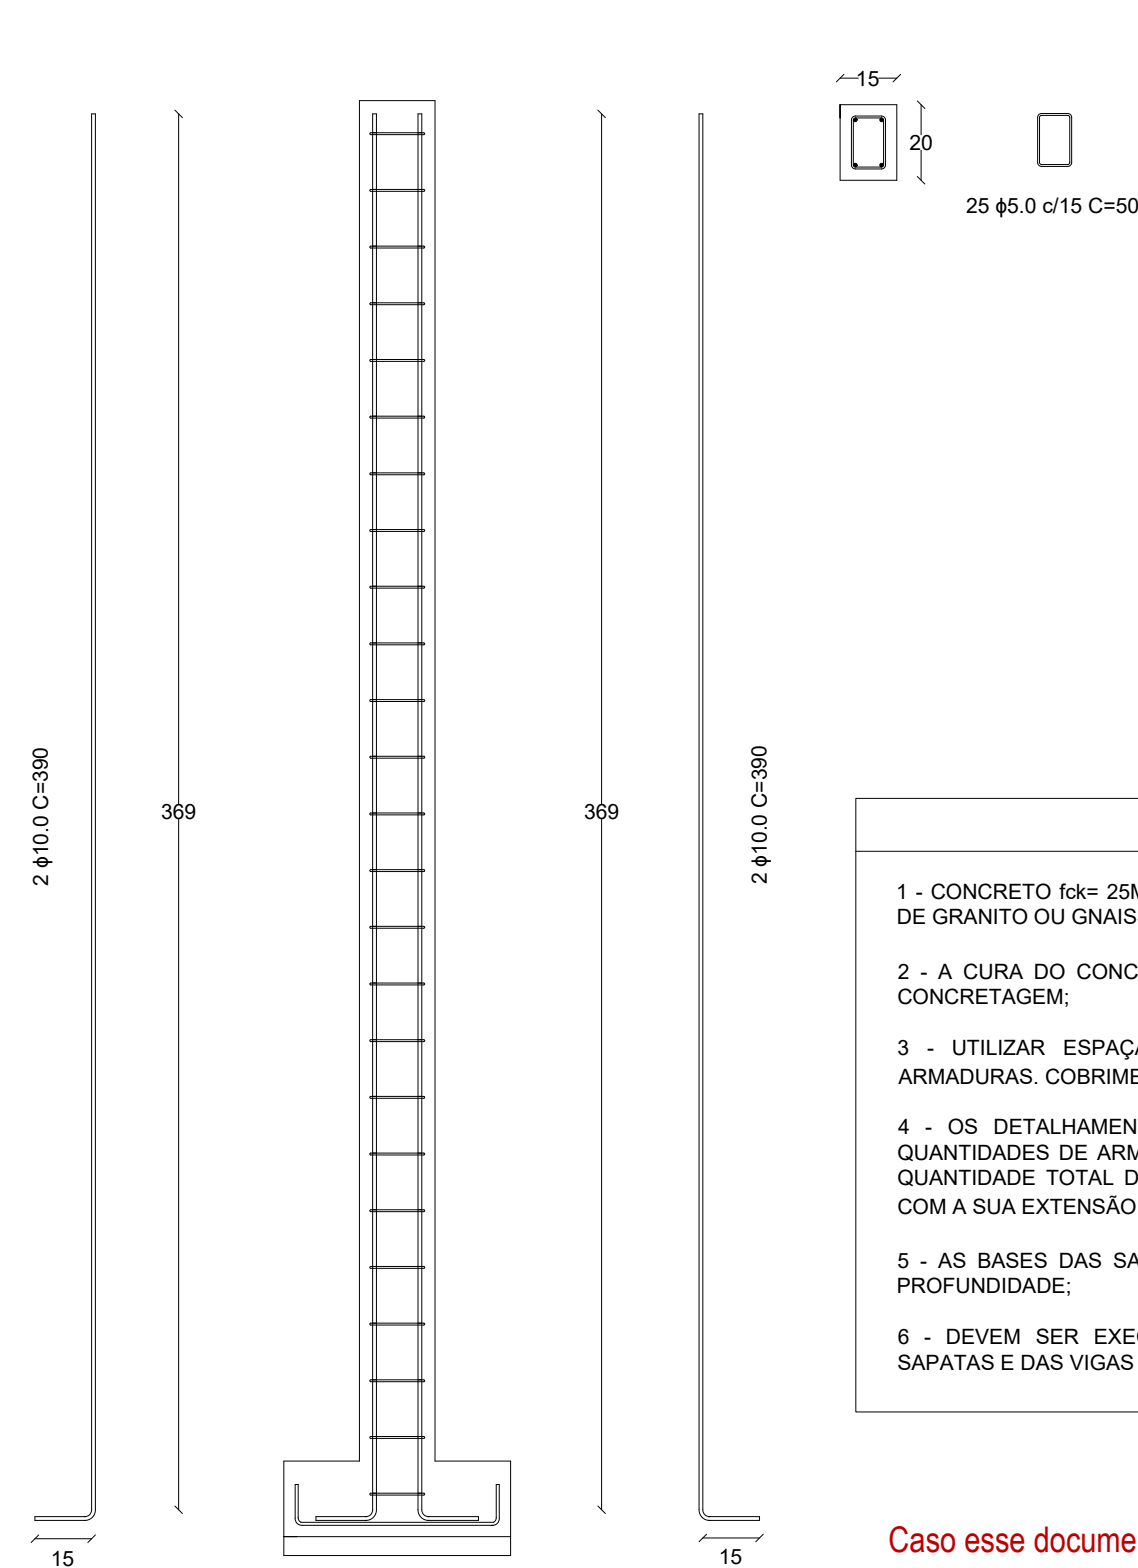
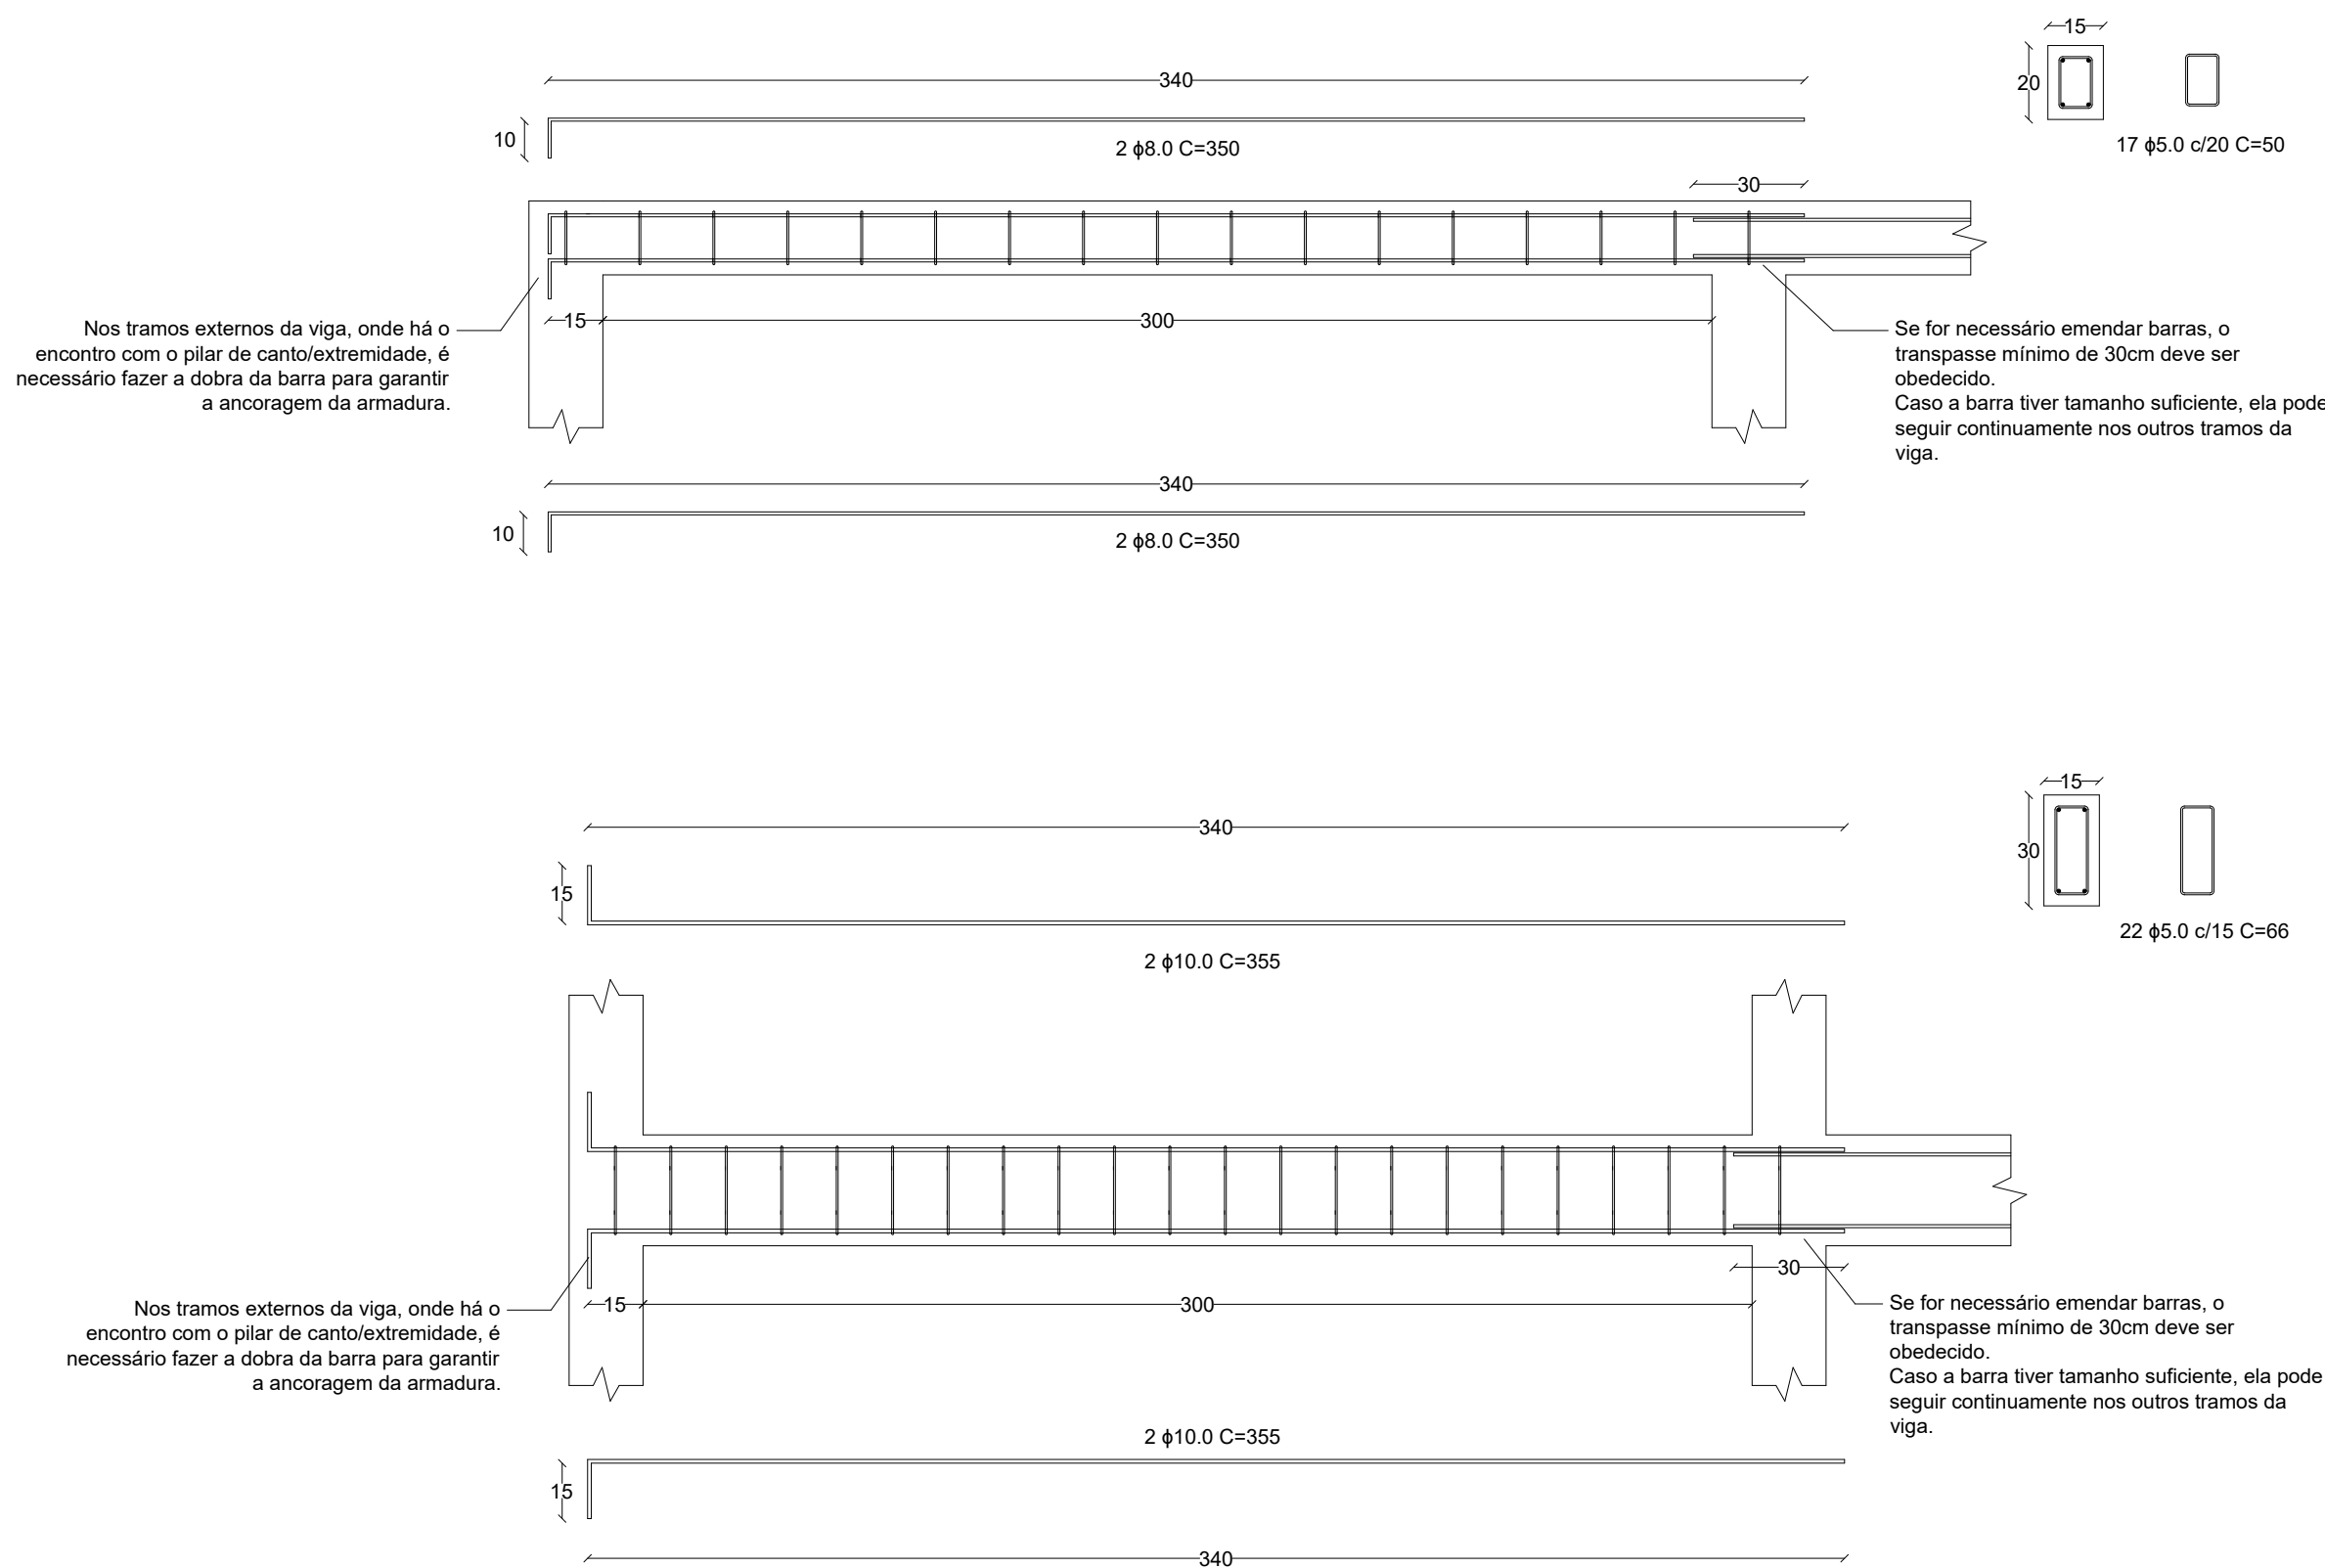
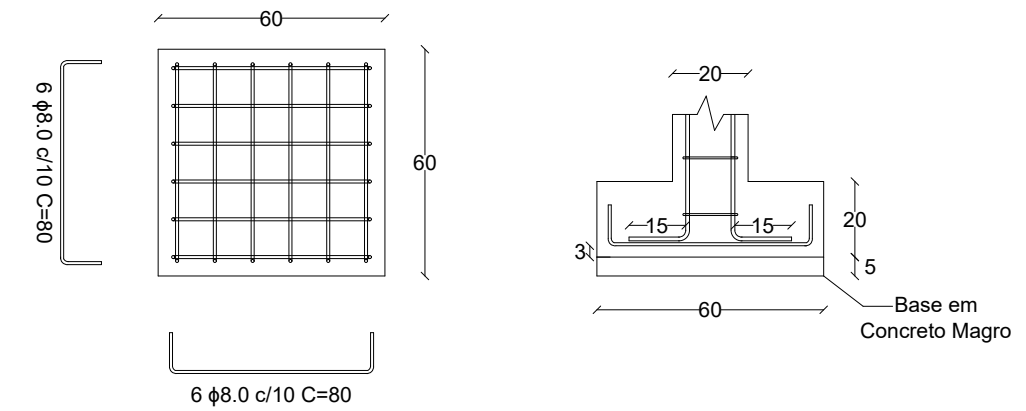


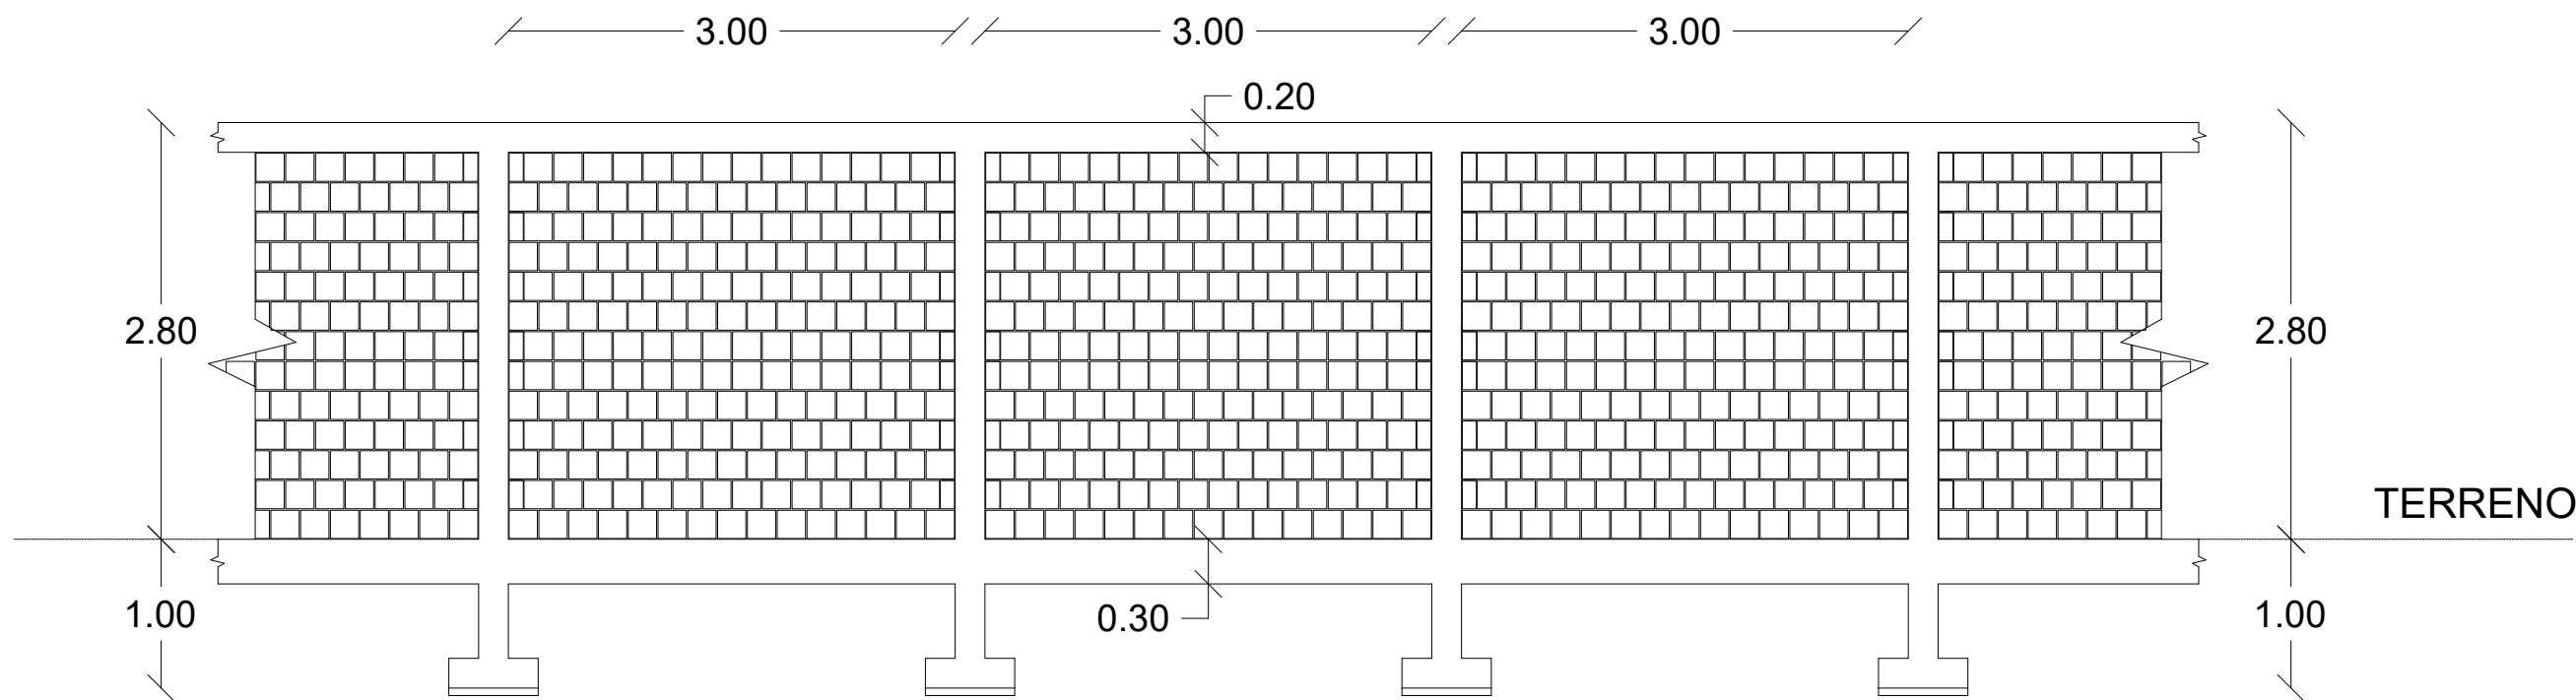

NOTAS GERAIS	
1 - CONCRETO fck= 25MPa (250kg/cm²) - NBR-6118/2023 C25 - BRITA 0 E 1 DERIVADA DE GRANITO OU GNAISSE - SLUMP 10+/-2;	
2 - A CURA DO CONCRETO DEVERÁ TER INÍCIO 5 HORAS APOS O TERMINO DA CONCRETAGEM;	
3 - UTILIZAR ESPAÇADORES PARA GARANTIR O COBRIMENTO MINIMO DAS ARMADURAS. COBRIMENTO MÍNIMO = 3,0 cm;	
4 - OS DETALHAMENTOS DAS VIGAS (CINTA E BALDRAME) APRESENTAM AS QUANTIDADES DE ARMADURAS PARA CADA TRAMO DAS VIGAS. DESSA FORMA, A QUANTIDADE TOTAL DE AÇO PARA O MURO DEVE SER CALCULADA DE ACORDO COM A SUA EXTENSÃO TOTAL;	
5 - AS BASES DAS SAPATAS DEVEM SER POSICIONADAS A NO MÍNIMO 1,0m DE PROFUNDIDADE;	
6 - DEVEM SER EXECUTADOS LASTROS DE CONCRETO MAGRO ABAIXO DAS SAPATAS E DAS VIGAS BALDRAME;	

CÓPIA DIGITAL VÁLIDA
Caso esse documento seja impresso, verificar a vigência na lista mestra.