


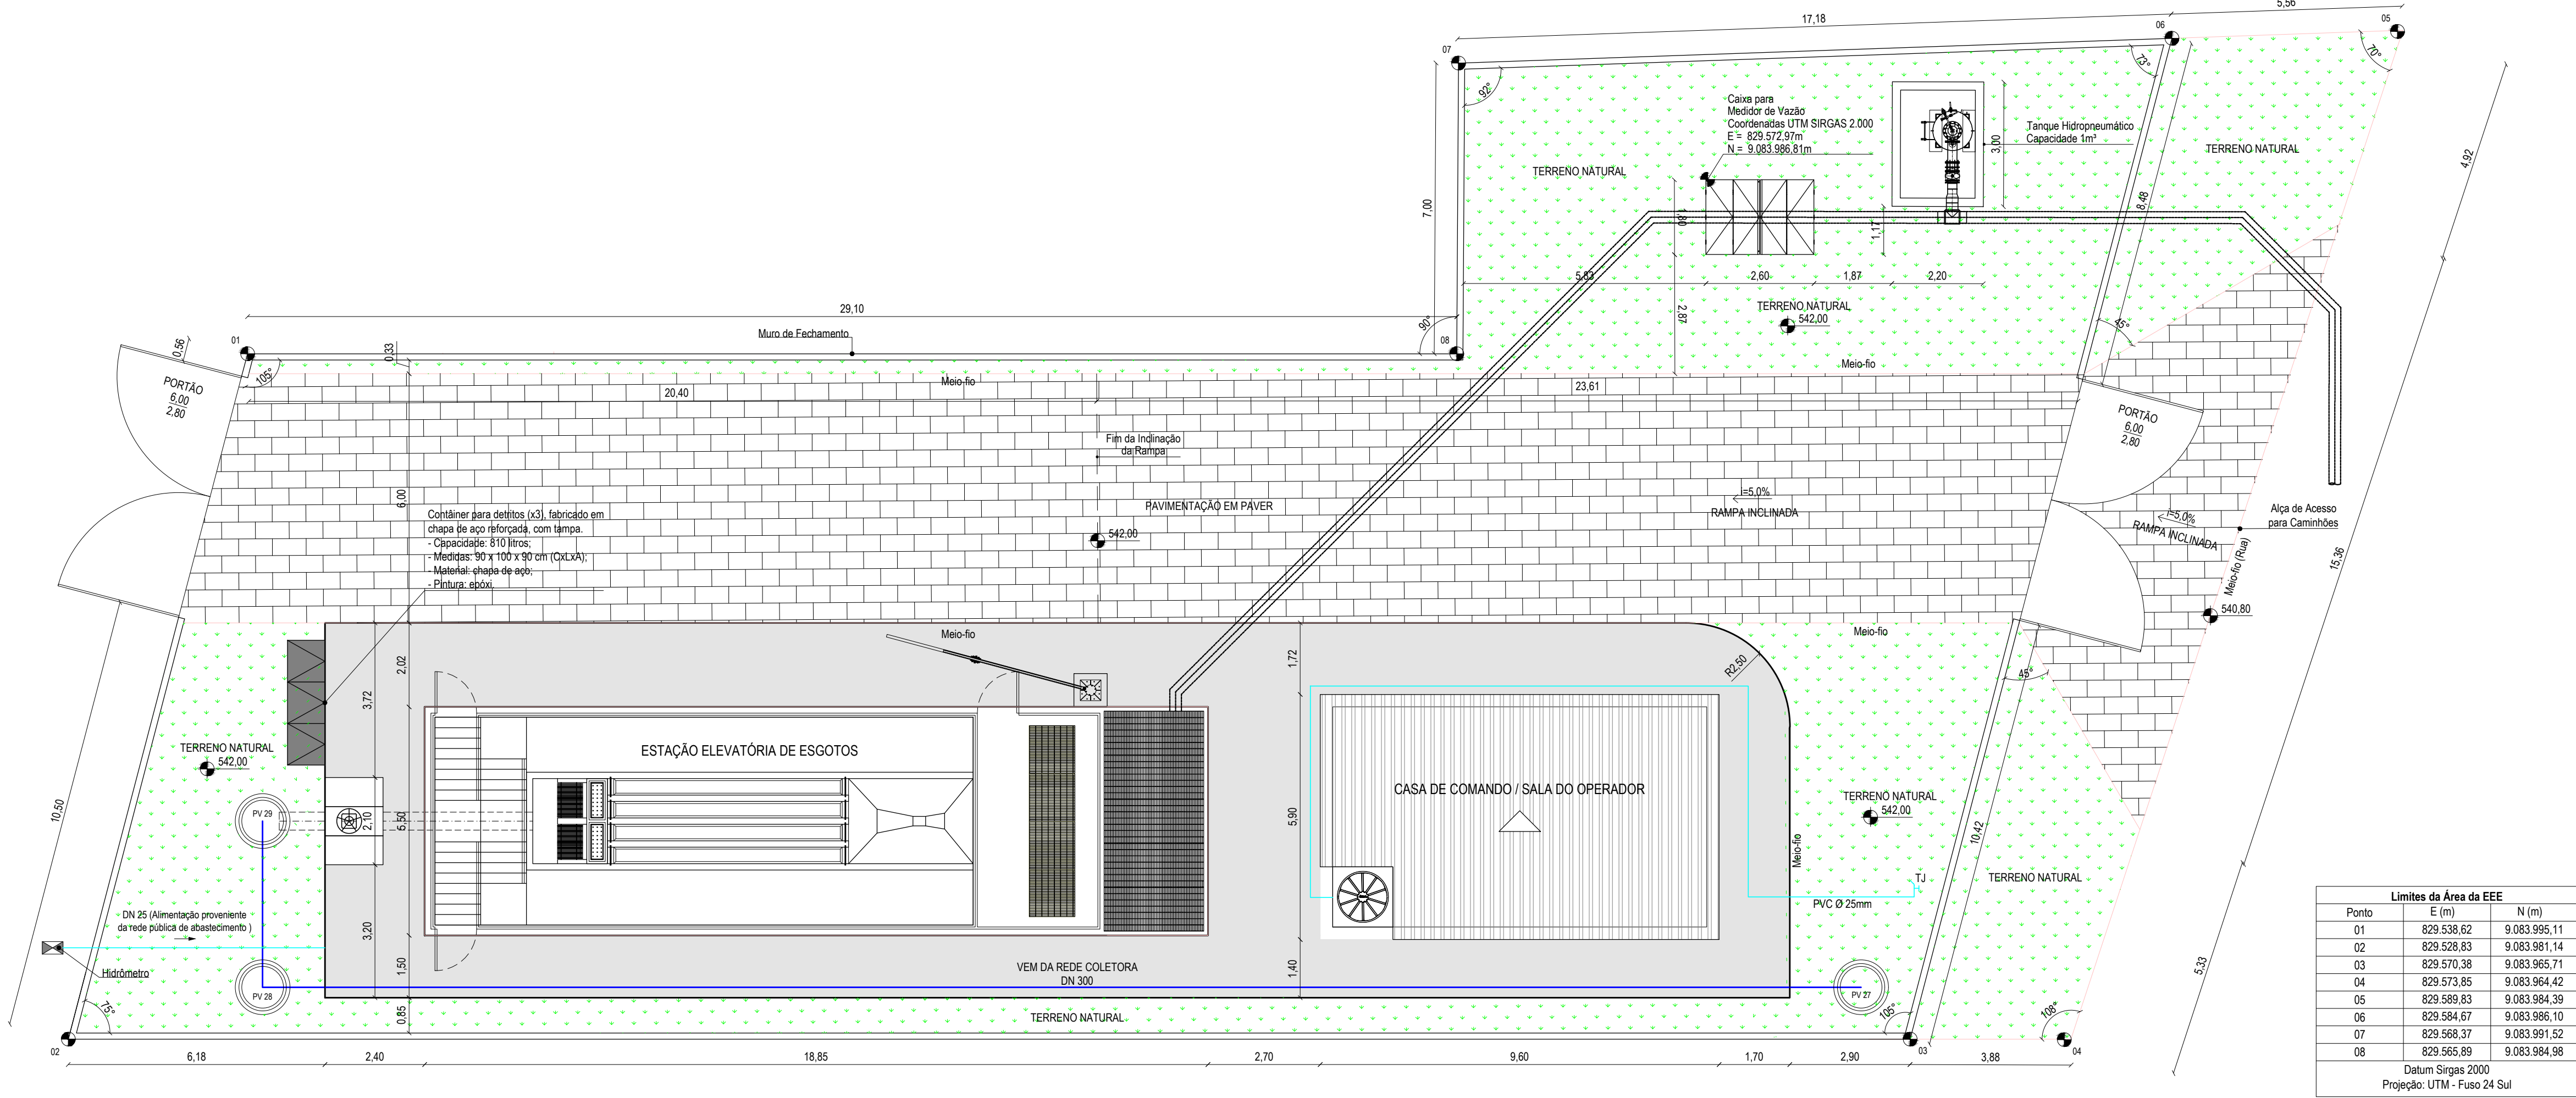


NOTAS

01 - Quando não indicado, medidas em metros;

02 - Letreiro e logotipo da Compesa deverá ser de acordo com o Manual de Identidade Visual.


LIGAÇÃO DE RAMAL PREDIAL DE ÁGUA COM HIDRÔMETRO NA CALÇADA

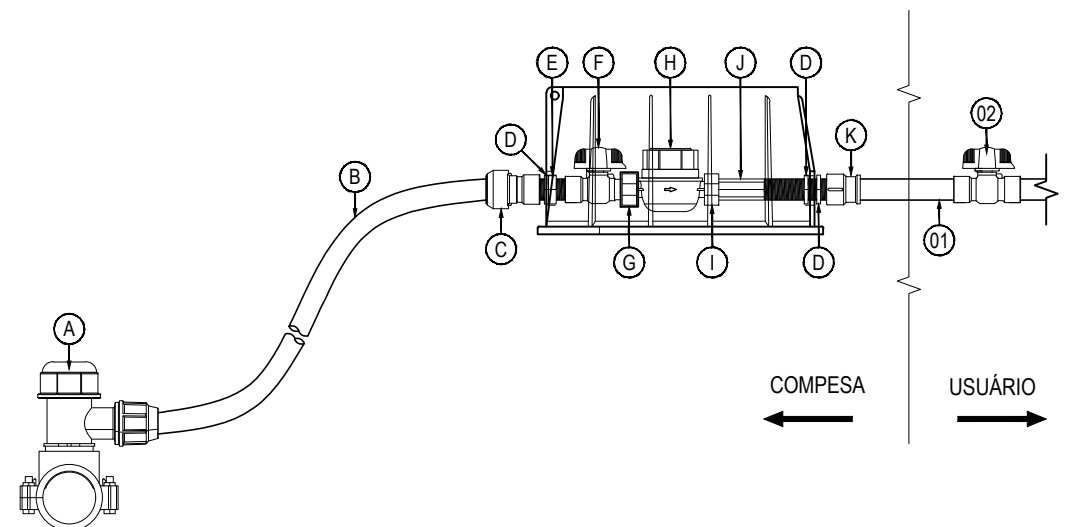


Detalhe Ligação Predial
Sem Escala

RELAÇÃO DE PEÇAS - LIGAÇÃO PREDIAL			
Ligação de Ramal Predial de Água - COMPESA			
Item	Descrição	Quant.	Diâmetros
A	Tê de serviço	1	D x 20mm
B	Tubo PEAD PE-80 na cor azul	-	20mm
C	Adaptador de compressão rosca fêmea para PEAD	1	20mm x 3/4"
D	Contrapressa sextavada	3	3/4"
E	Niple especial sextavado	1	3/4"
F	Registro esfera com porca tubete	1	3/4"
G	Lacre tipo carlota	1	3/4"
H	Hidrômetro	1	3/4"
I	Porca sextavada com inserto metálico em toda a rosca	1	20mm
J	Tubete longo com porca sextavada com inserto metálico em toda a rosca de 20mm	1	3/4"
K	Luva soldável com rosca	1	25mm x 3/4"
Ligação de Ramal Predial de Água - Cliente			
01	Tubo PVC soldável	-	25mm
02	Registro de esfera com borboleta soldável	1	25mm

RELAÇÃO DE PEÇAS - TANQUE HIDROPNEUMÁTICO						
Item	Material	PN	DN	dn	Descrição	Comp (mm)
01	PEAD	10	280	-	Tee para PEAD termofusão	-
02	PEAD	10	280	225	Redução sagol para PEAD termofusão	-
03	PEAD	10	225	-	Colarinho para PEAD termofusão	-
04	Aço	10	200	-	Flange solto para PEAD	-
05	FoFo	10	200	-	Valvula de gaveta com flanges e volante	-
06	FoFo	10	200	-	Junta de desmontagem travada axialmente	-
07	FoFo	10	200	-	Toco com flanges	500
08	FoFo	10	200	-	Curva 90° com flanges	-
09	-	-	-	-	Tanque hidropneumático, capacidade 1m³	-
	-	-	200	-	Arruela de borncha para flanges	-
	-	-	-	-	Parafuso para flange 20x90	-

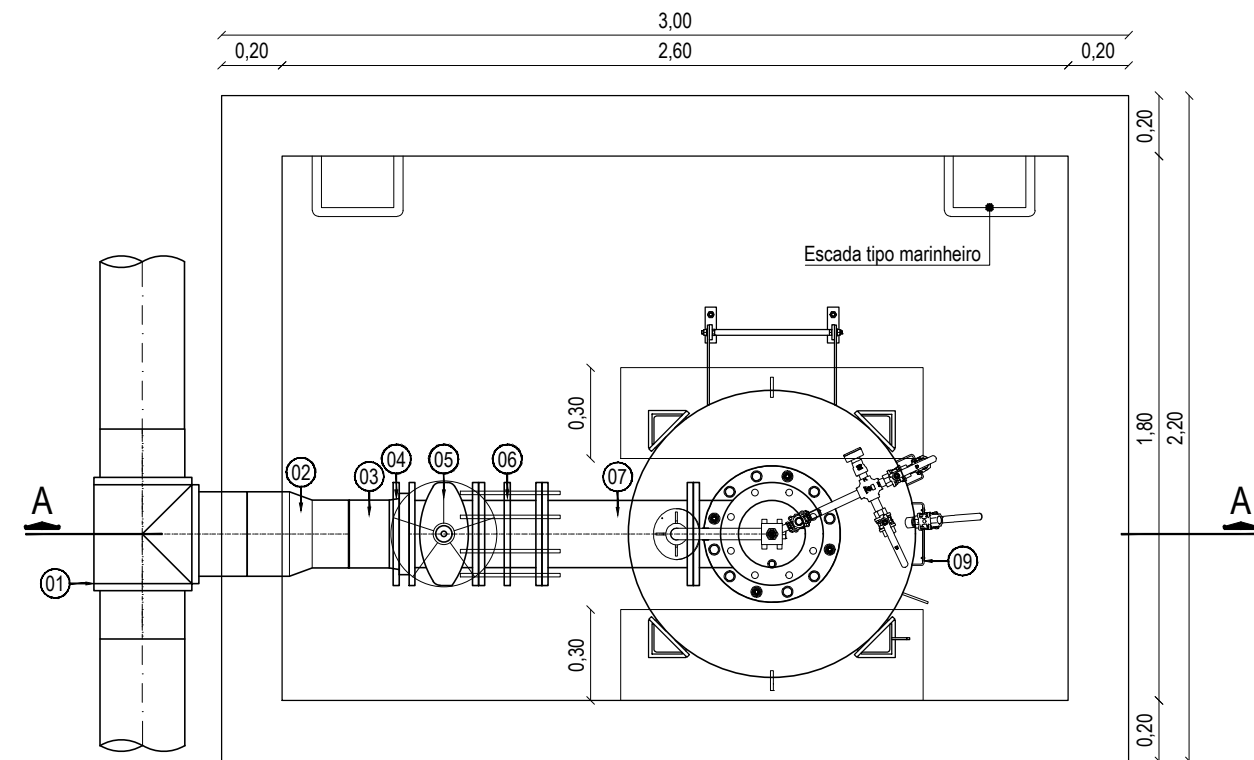


Tanque Hidropneumático - Planta Baixa
Escala 1 : 25

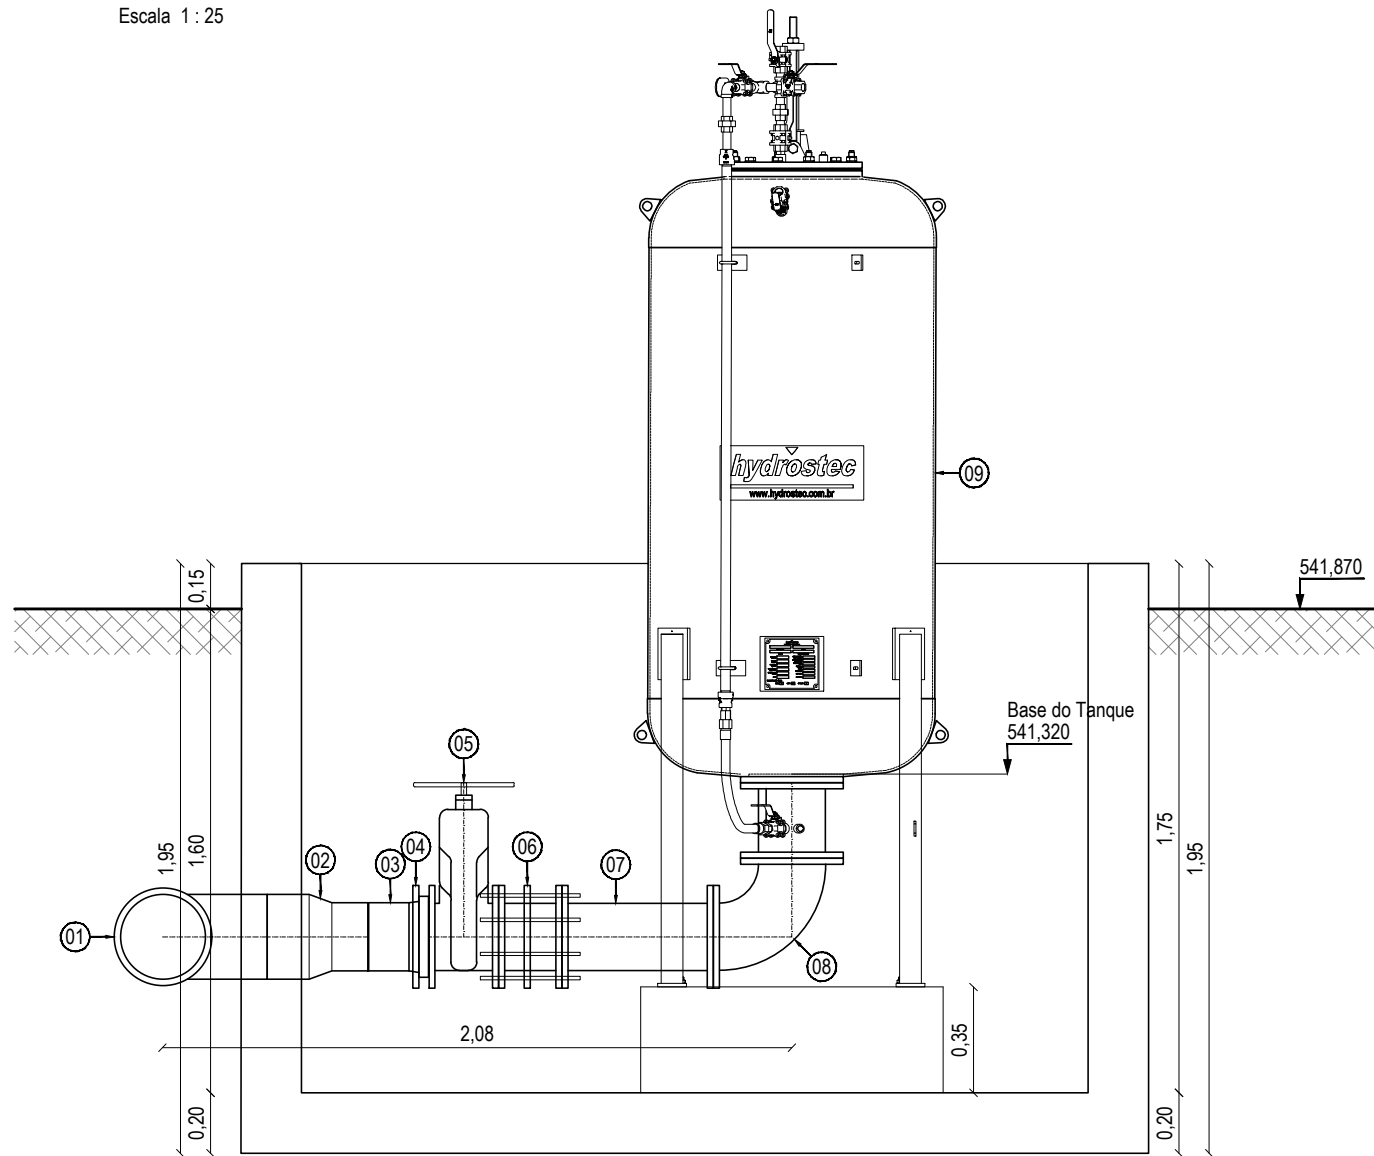


Tanque Hidropneumático - Corte A - A
Escala 1 : 25

Detalhe do Muro e Portão - Planta Baixa
Escala 1 : 50

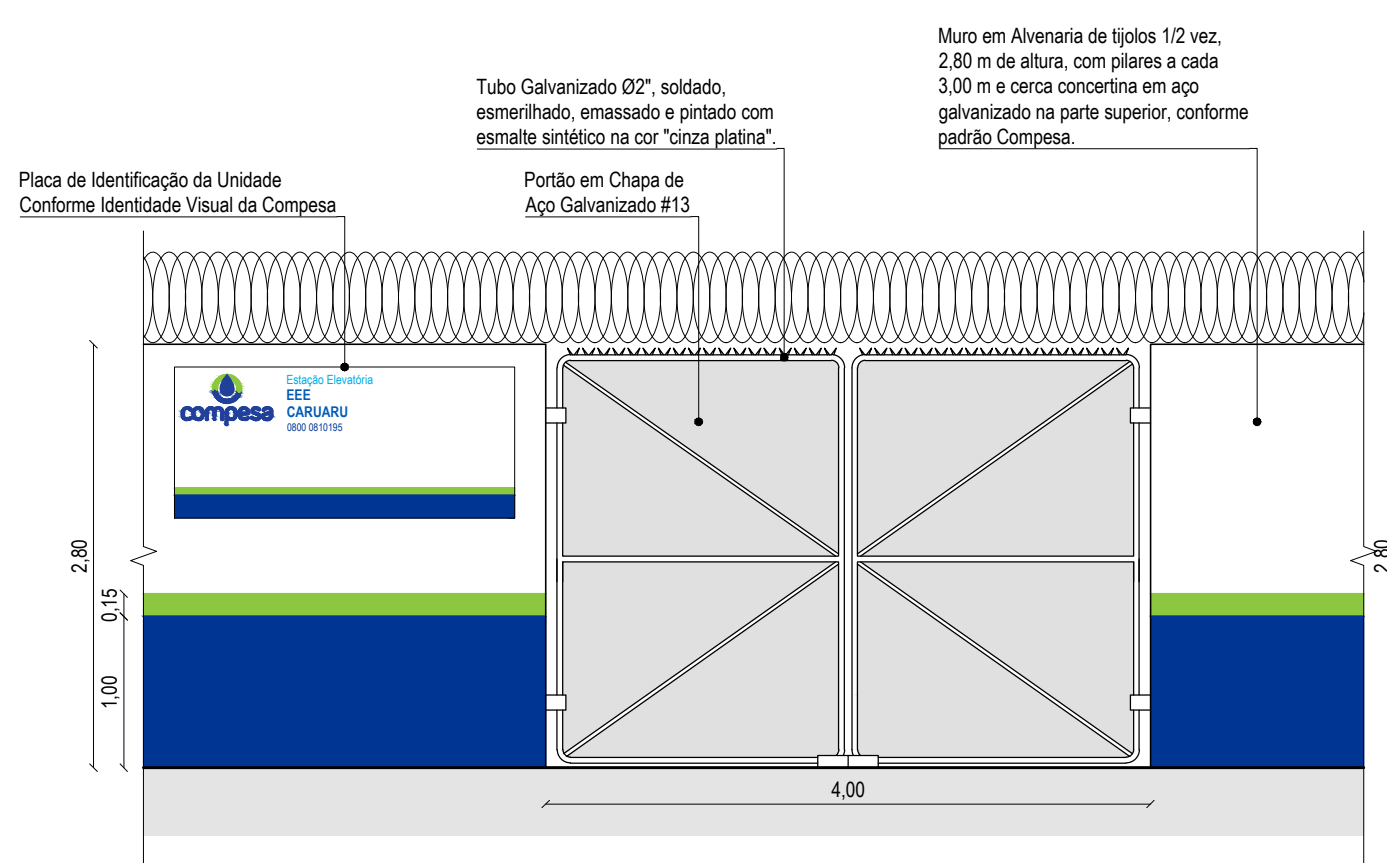

Fachada Principal
Escala 1 : 50

OBS:
Faixa Azul: 1,00 m a partir da base, cor PANTONE 661C
Faixa Verde: 0,15 m acima da faixa azul, cor PANTONE 360C

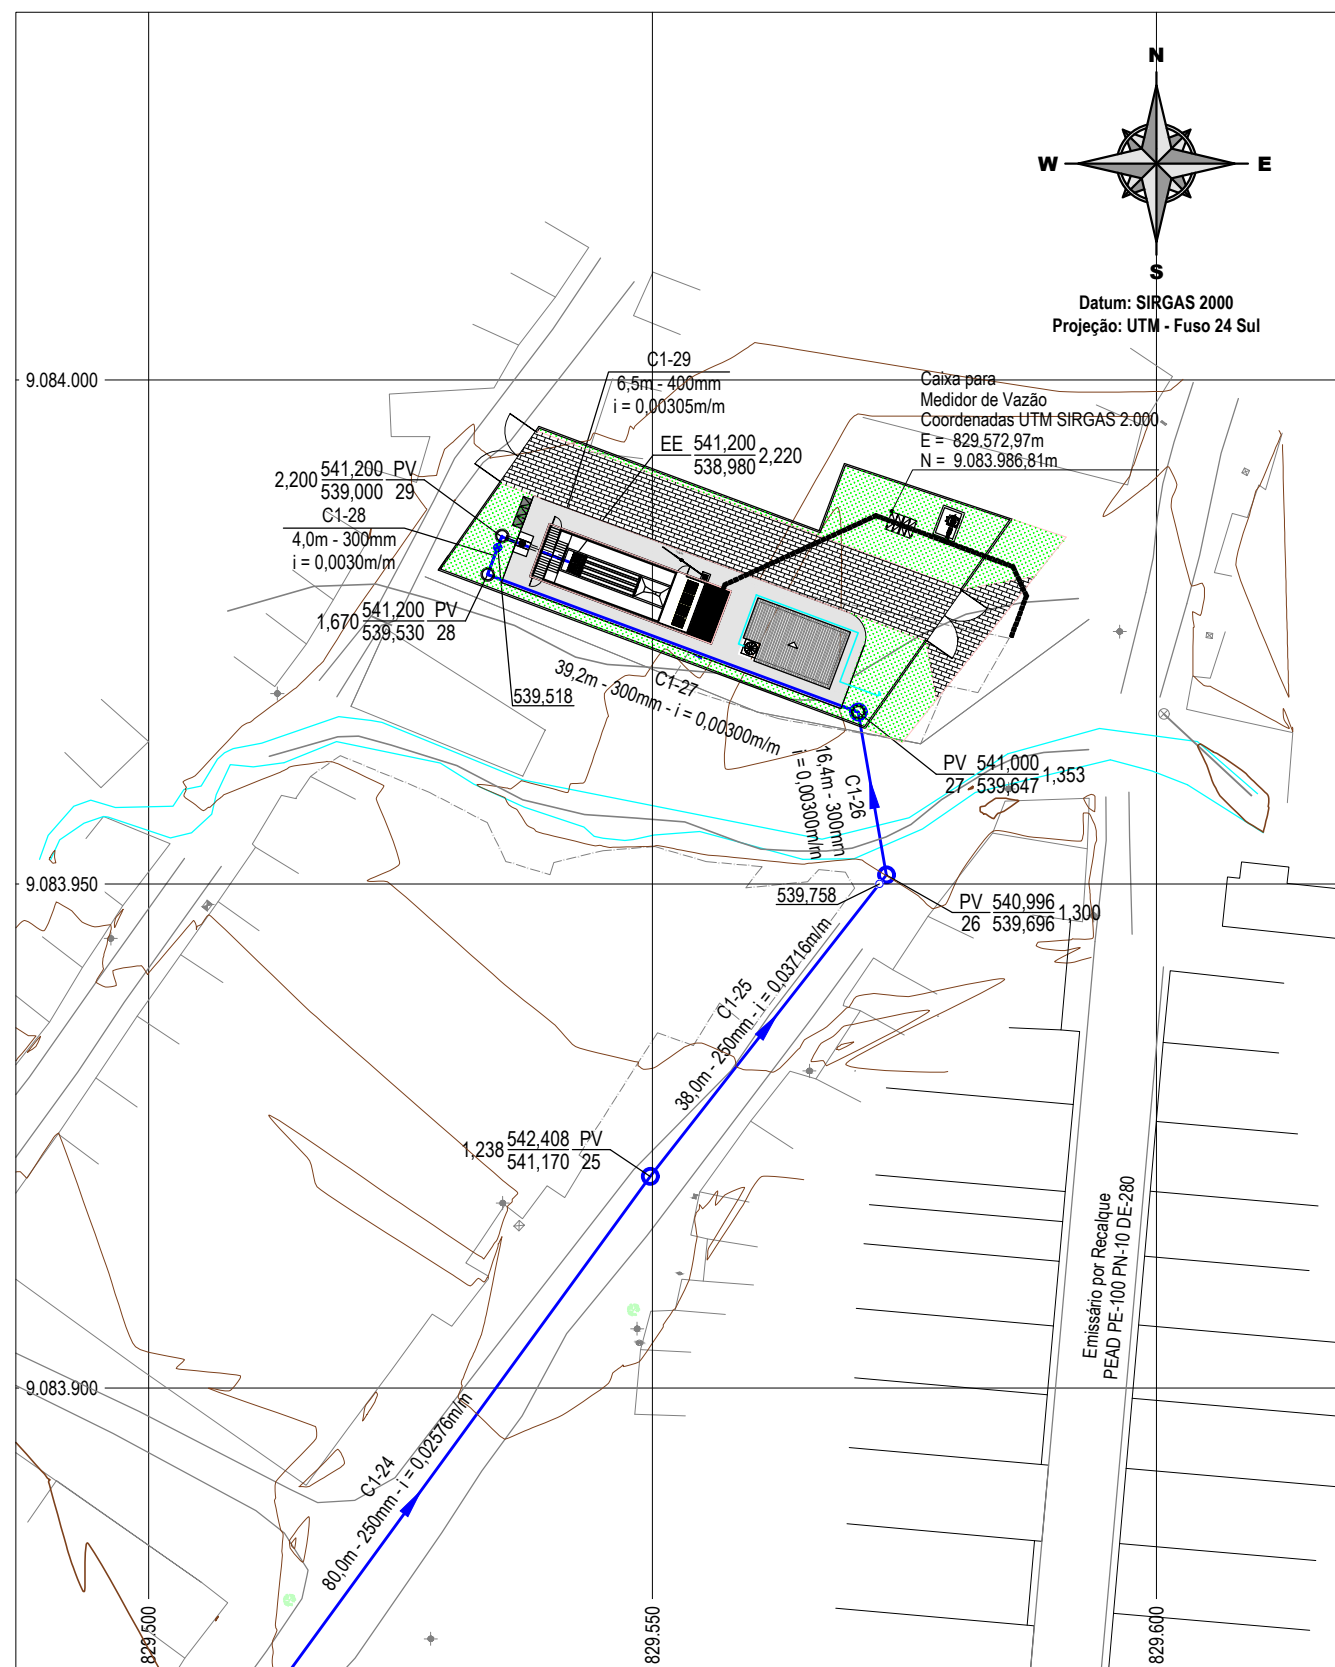

Planta de Situação
Escala 1 : 750

CÓPIA DIGITAL VÁLIDA
Caso esse documento seja impresso, verificar a vigência na lista mestra.