



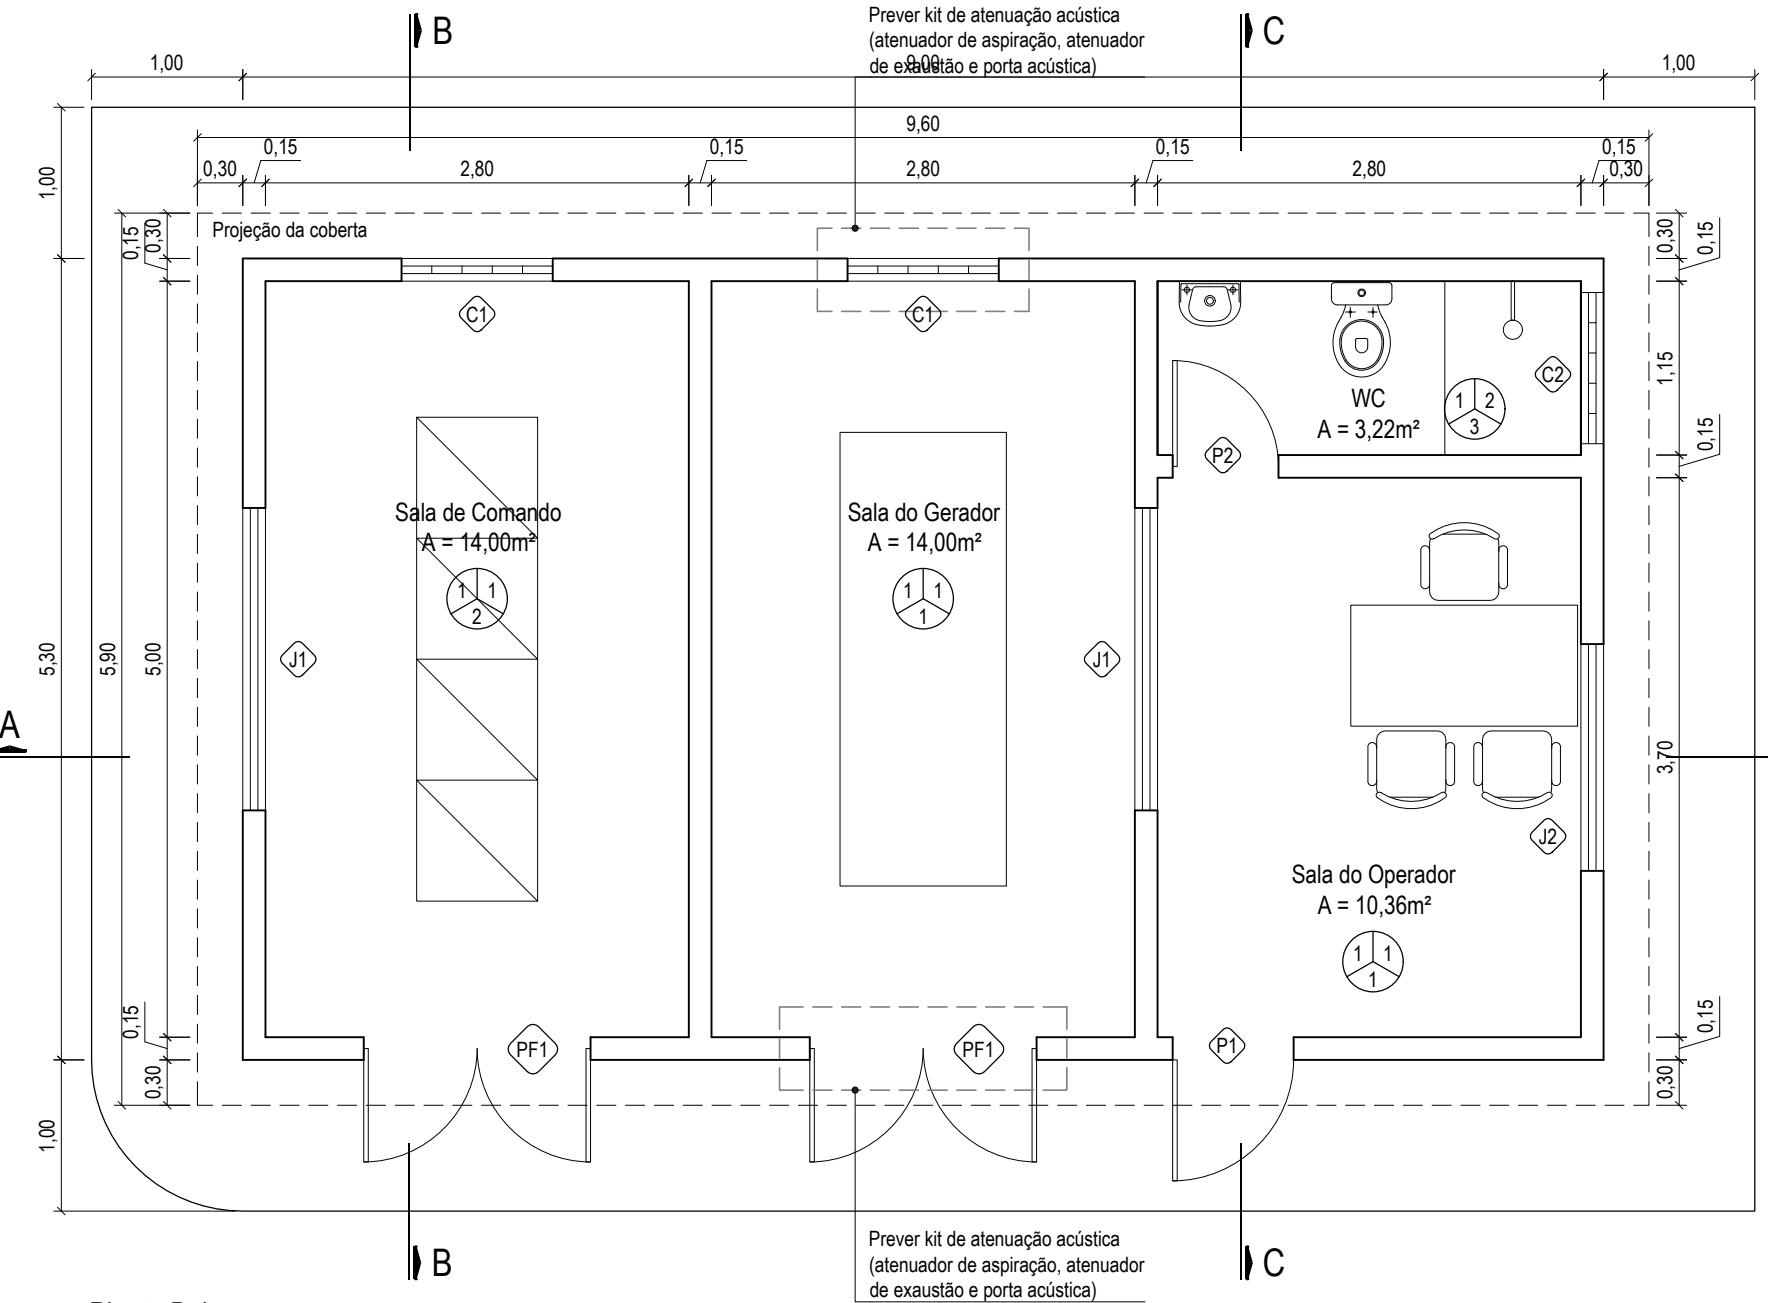

Planta Baixa
Escala 1 : 50

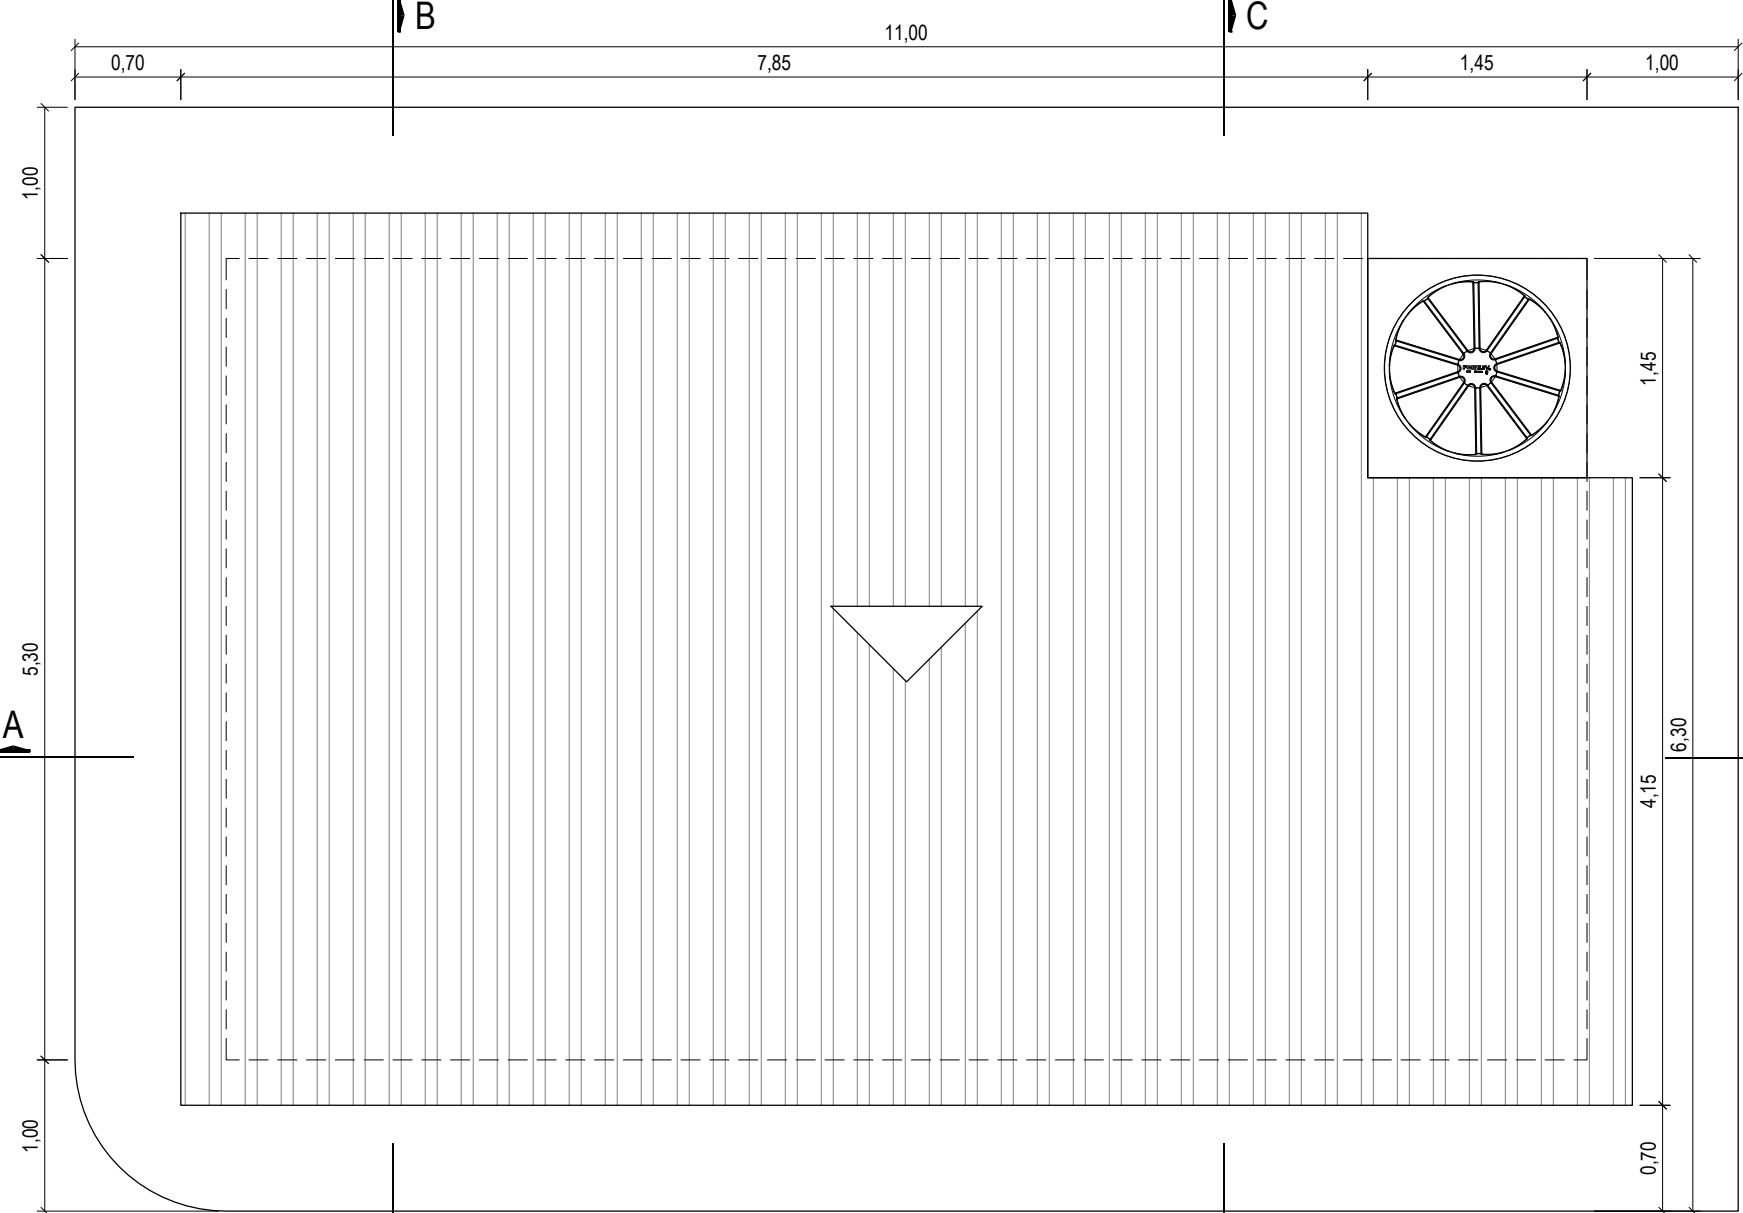


Planta de Coberta
Escala 1 : 50


Quadro de Esquadrias				
Legenda	Dimensões	Bandeirala	Descrição	Quant.
Portas	PF1	1,50 x 2,10m	Porta em chapa de aço nº 14	2
	P1	0,80 x 2,10m	Porta externa em madeira maciça	1
	P2	0,70 x 2,10m	Porta interna em madeira semi-oca	1
Legenda	Dimensões	Parapeito	Descrição	Quant.
Janelas	J1	2,00 x 1,00m	Janela de correr em alumínio anodizado com vidro	2
	J2	1,50 x 1,00m	Janela de correr em alumínio anodizado com vidro	1
Cobogós	C1	1,00 x 1,00m	Cobogó (elemento vazado) de concreto	2
	C2	1,00 x 0,50m	Cobogó (elemento vazado) de concreto	1

Especificações	
Teto:	01 - Pintura em tinta látex base PVA.
Parade:	01 - Pintura em tinta látex base PVA; 02 - Revestimento em cerâmica esmaltada, tipo A.
Piso:	01 - Piso em cimento impermeabilizado, esp. 1,5 cm; 02 - Piso em borracha anti-derrapante; 03 - Piso em cerâmica esmaltada, tipo A.


RELAÇÃO DE PEÇAS				
Item	Material	DN	Descrição	Quant.
01	PVC	20	- Tubo em PVC soldável	20 m
02	PVC	25	- Tubo em PVC soldável	10 m
03	PVC	20	- Joelho 90° soldável	4
04	PVC	20	- Registro de gaveta	1
05	PVC	20	- Adaptador para caixa d'água	1
06	PVC	25	- Adaptador para caixa d'água	1
07	PVC	25	- Joelho 90° soldável	2
08	PVC	25	- Registro de gaveta	1
09	PVC	25	- Tê soldável	3
10	PVC	25	- Joelho 90° com bucha de reforço	3
11	PVC	25	- Registro de pressão	1
12	PVC	50	- Tubo para esgoto predial	4 m
13	PVC	100	- Tubo para esgoto predial	7 m
14	PVC	100	- Ralo seco	1
15	PVC	150	- Caixa sifonada	2
16	PVC	50	- Joelho 45° para esgoto	3
17	PVC	50	- Joelho 90° para esgoto	2
18	PVC	100	- Joelho 90° para esgoto	1

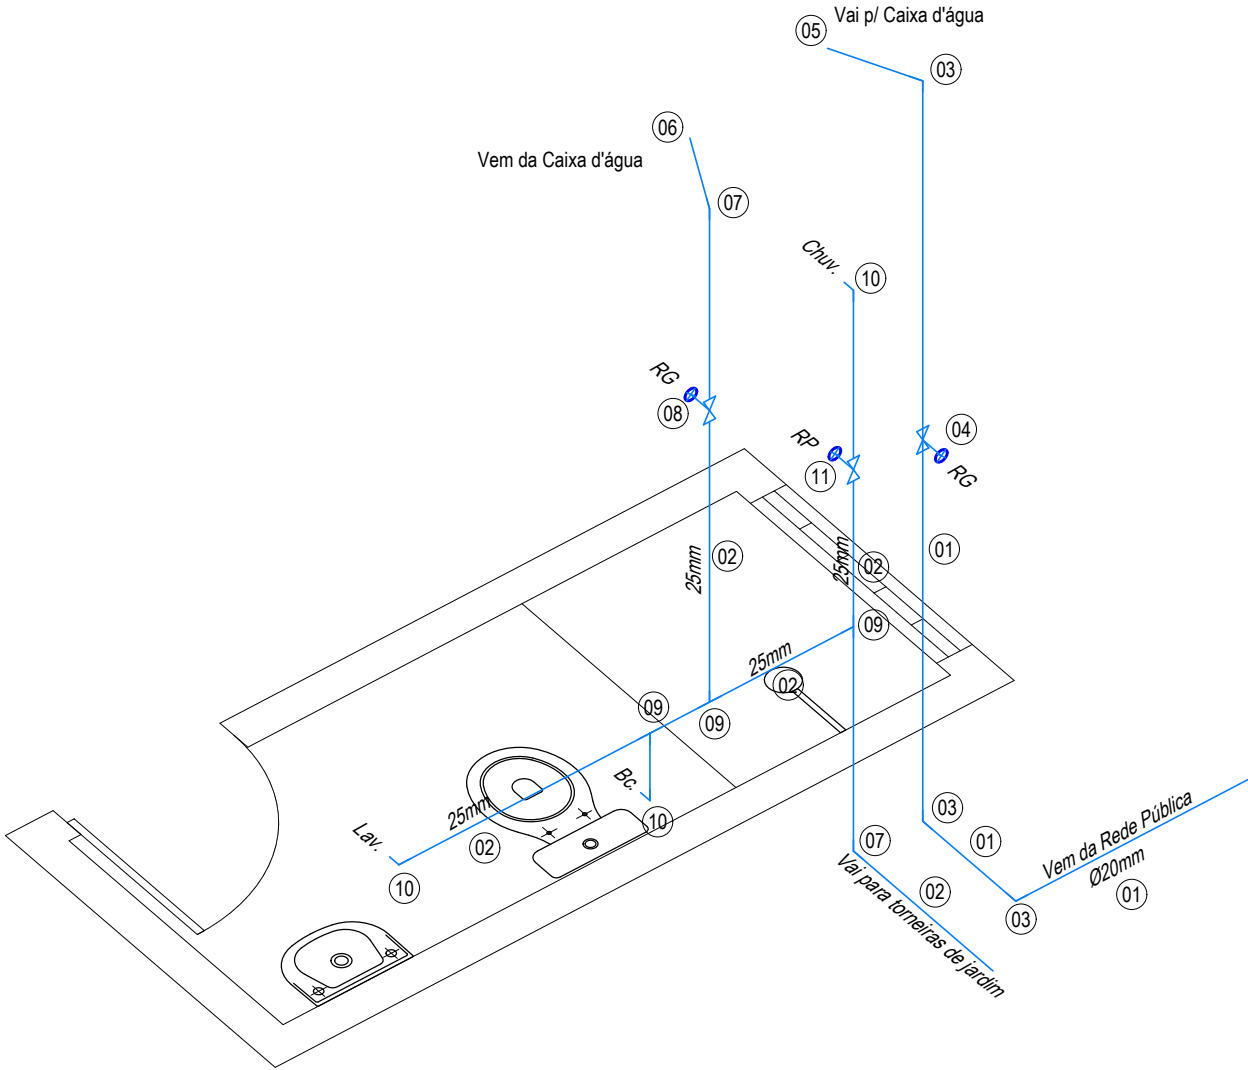


Instalações Hidráulicas - Perspectiva
Escala 1 : 25

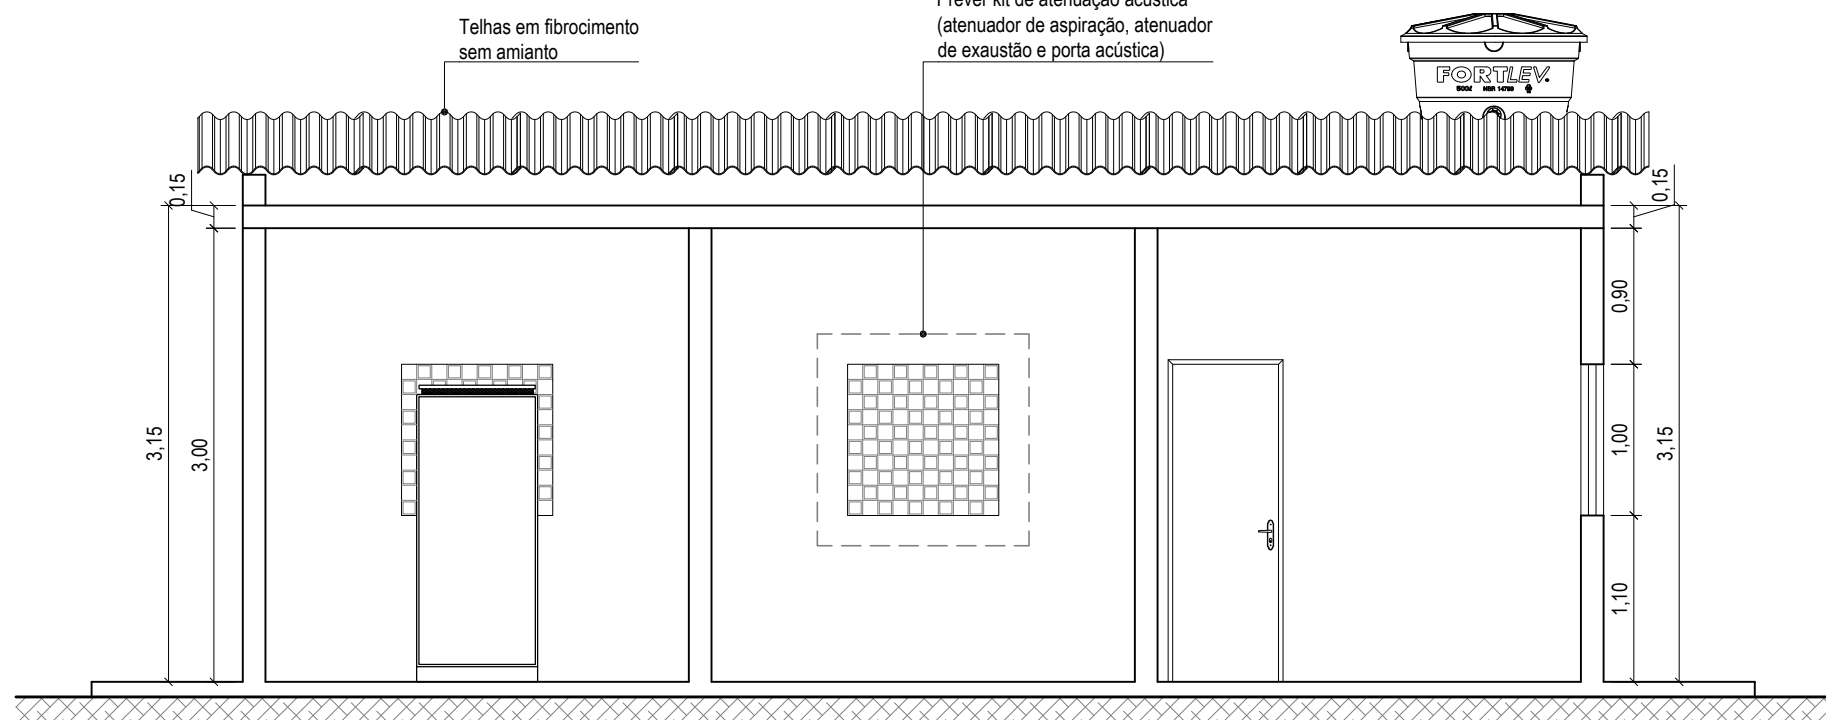


Corte A - A
Escala 1 : 50

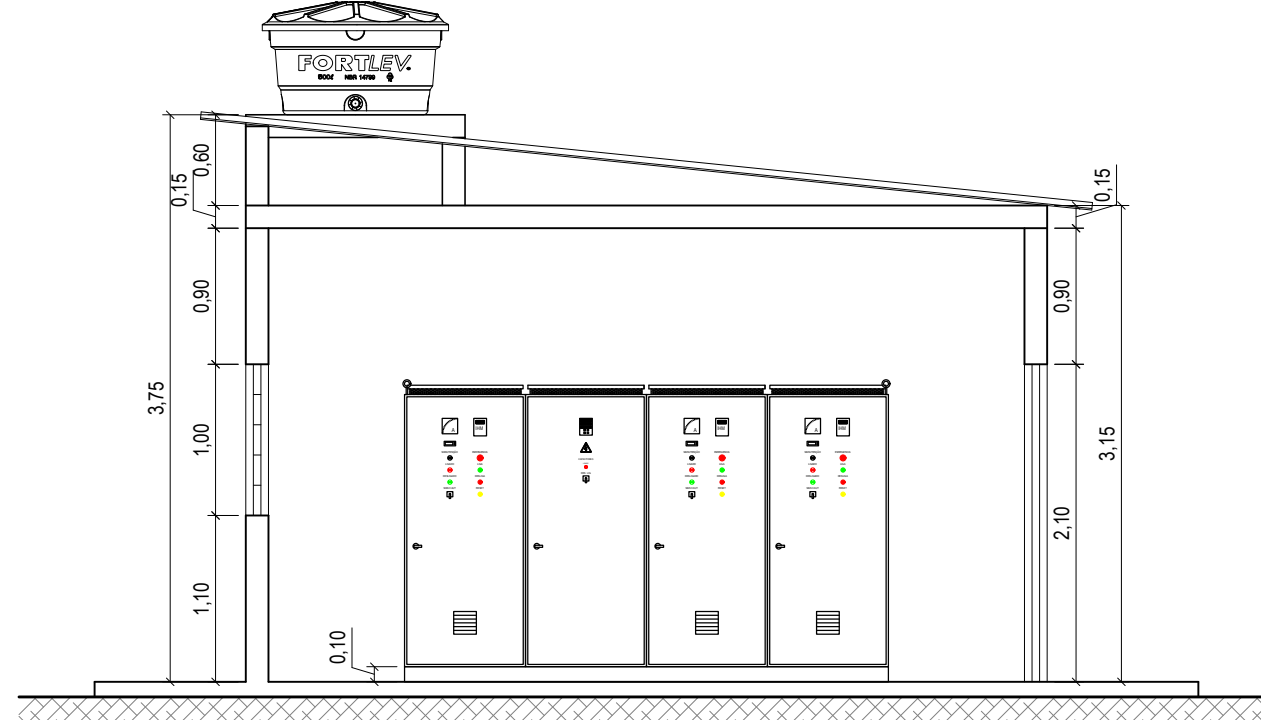


Corte B - B
Escala 1 : 50

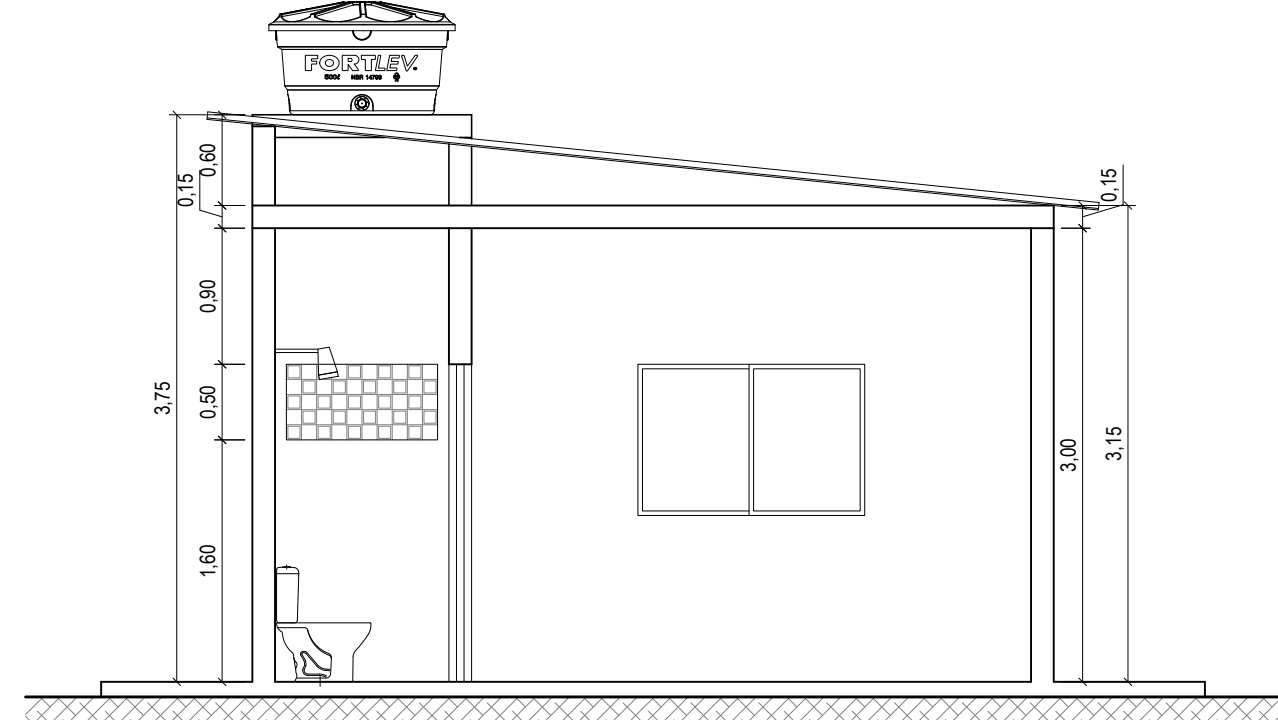


Corte C - C
Escala 1 : 50

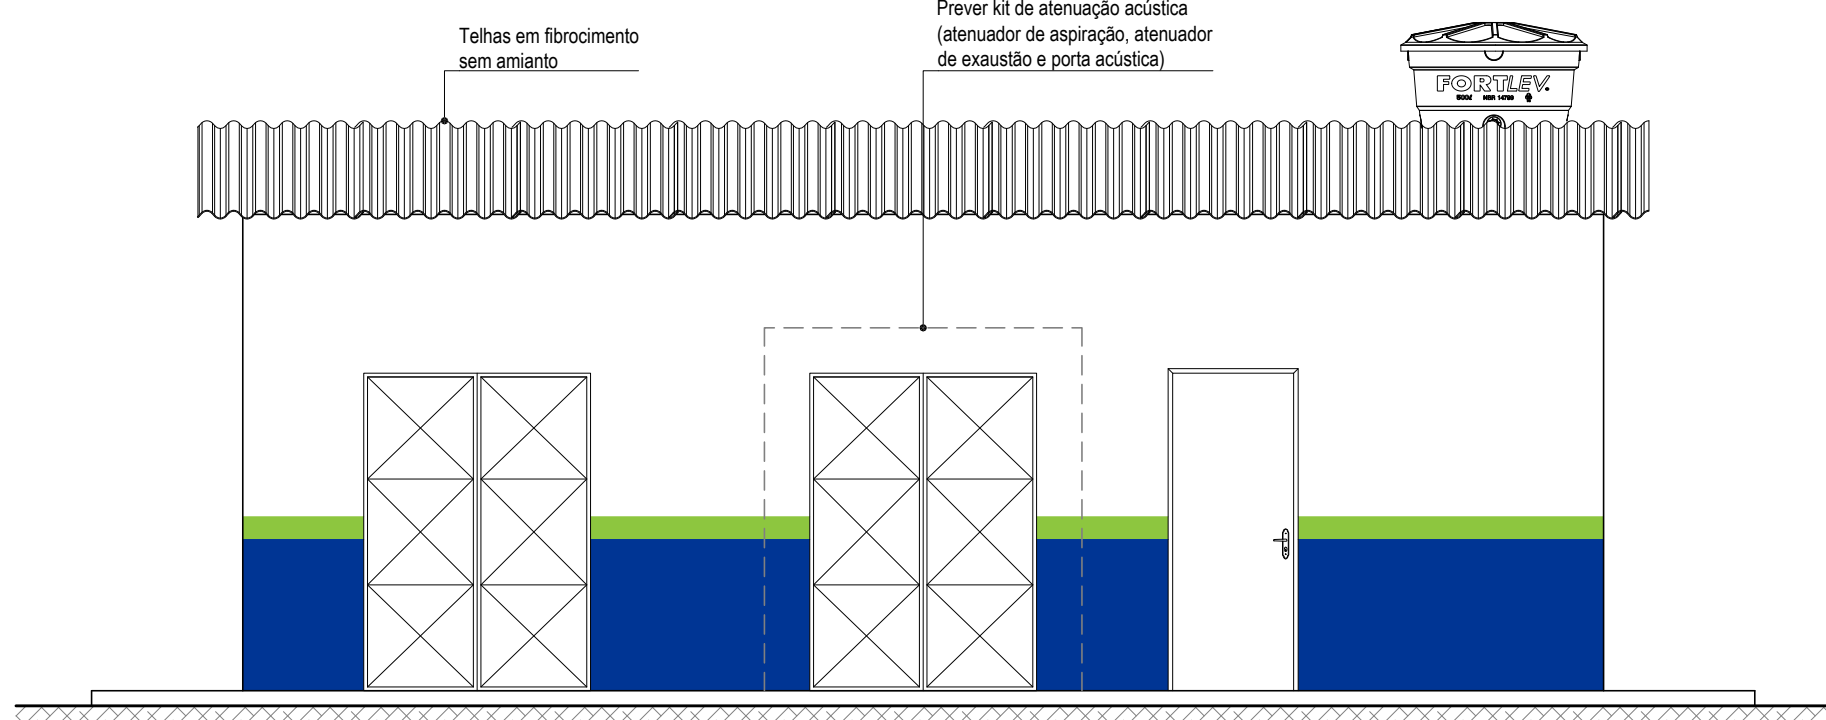


Fachada Frontal
Escala 1 : 50

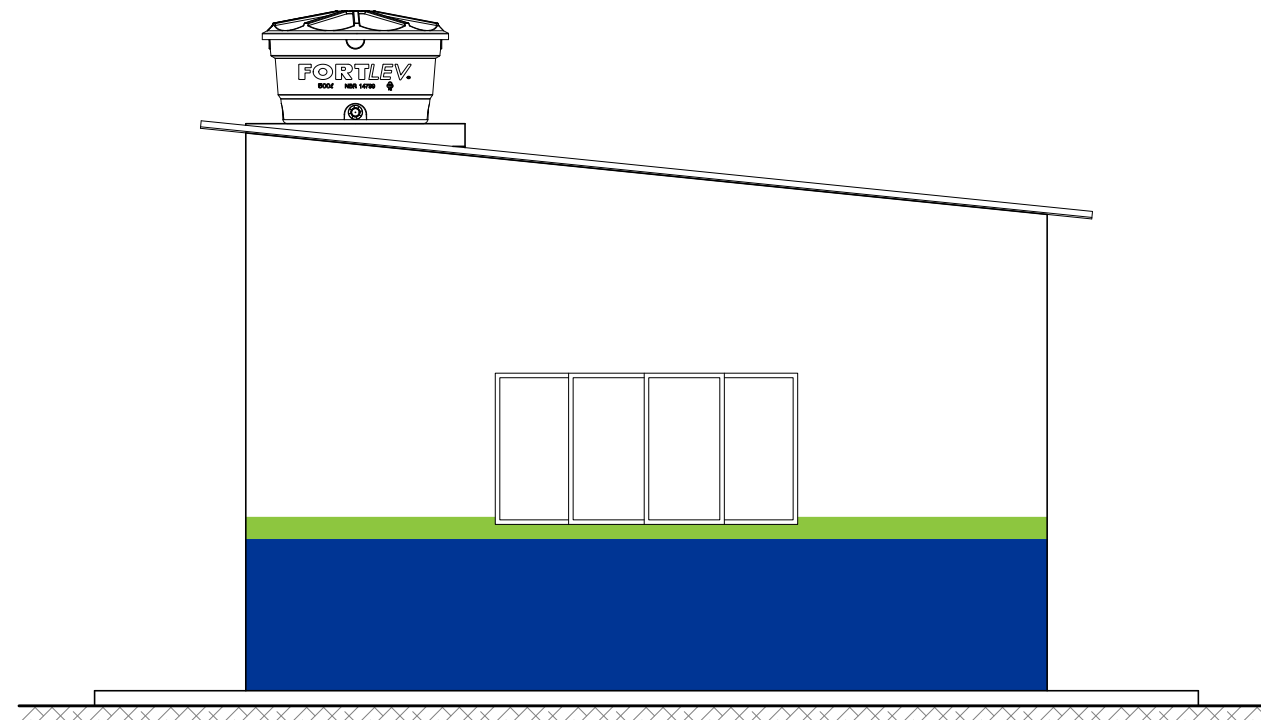


Fachada Lateral Esquerda
Escala 1 : 50

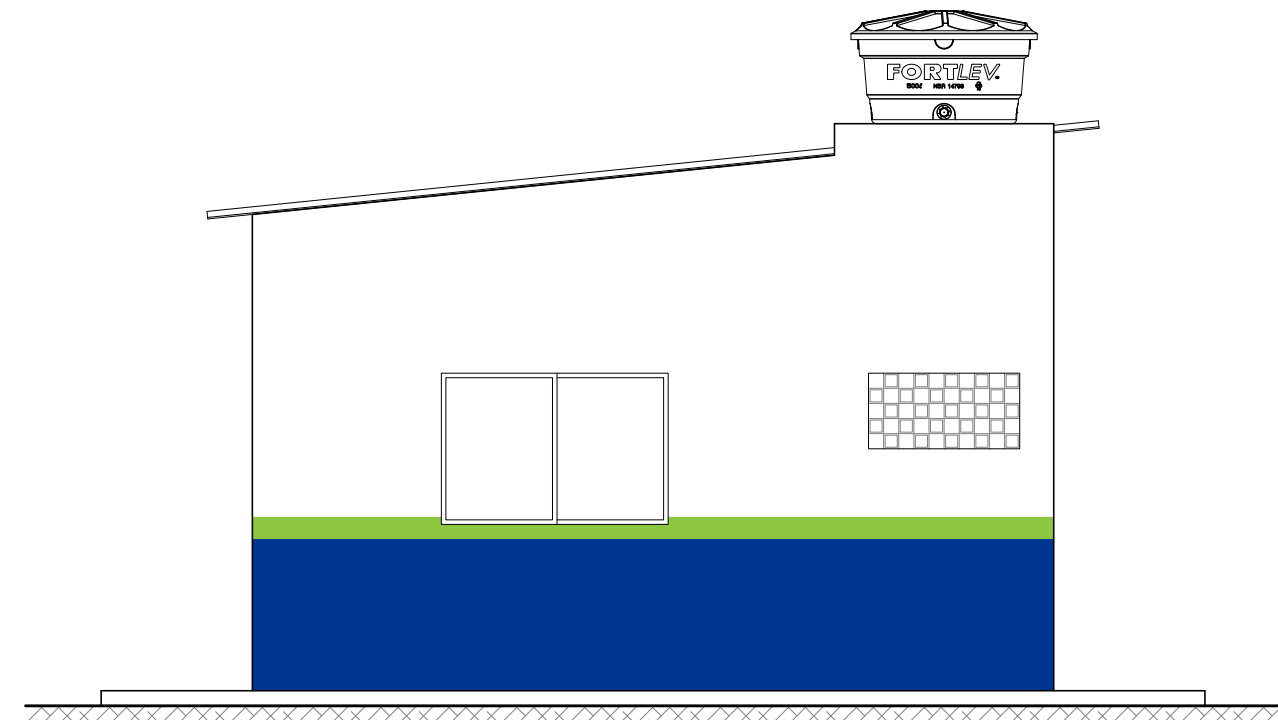


Fachada Lateral Direita
Escala 1 : 50

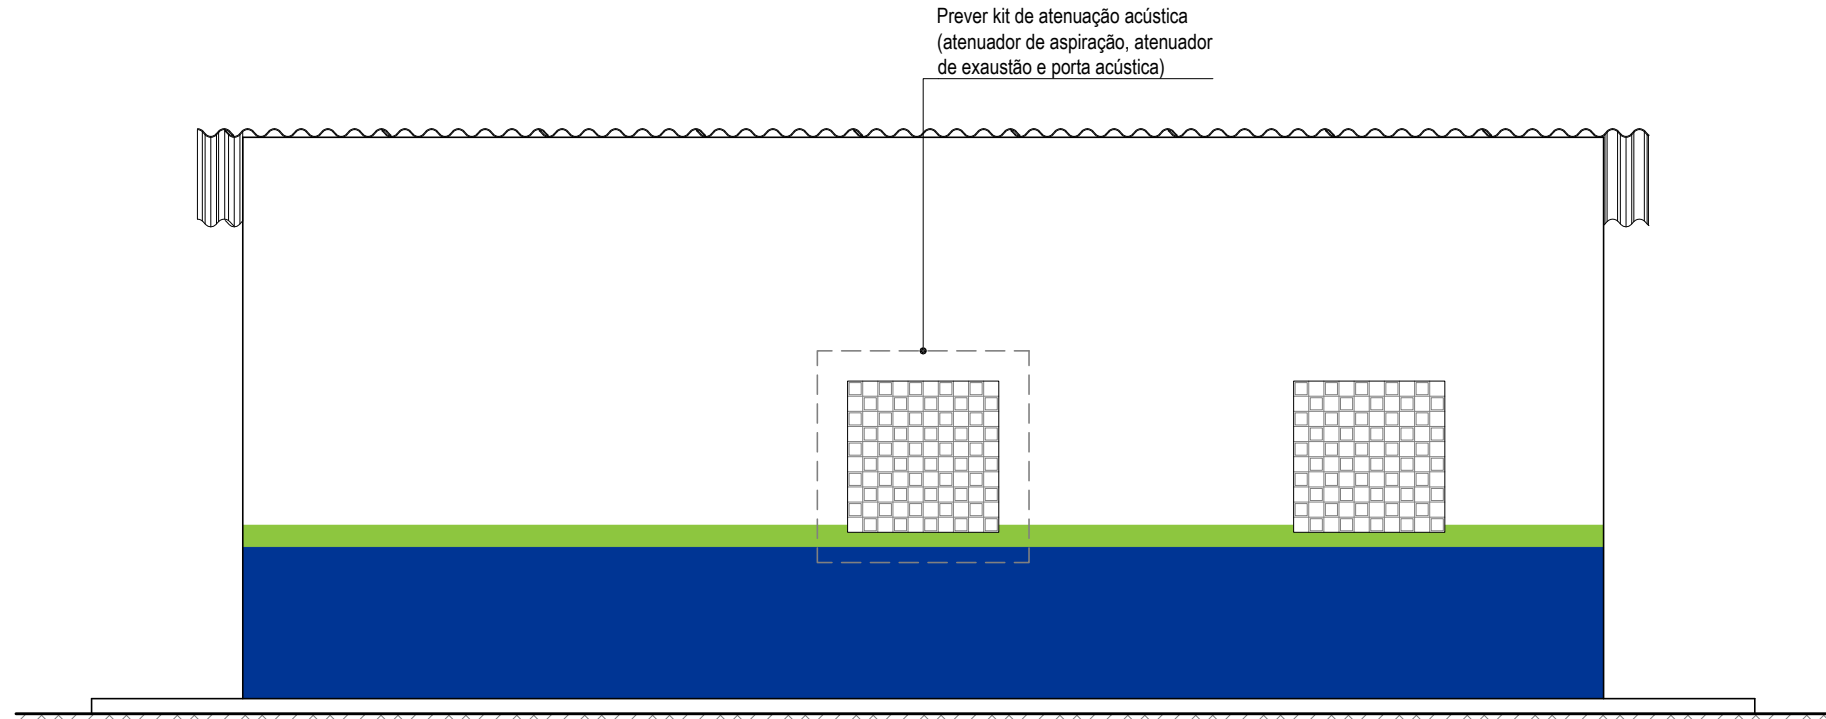

Fachada Posterior
Escala 1 : 50

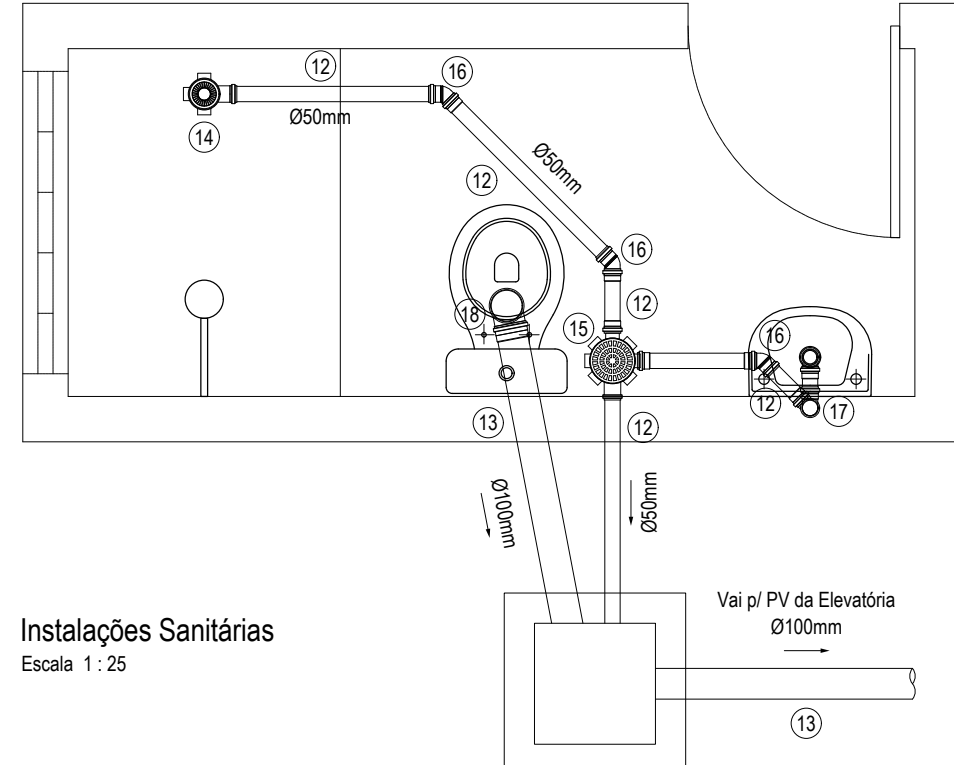

Instalações Sanitárias
Escala 1 : 25

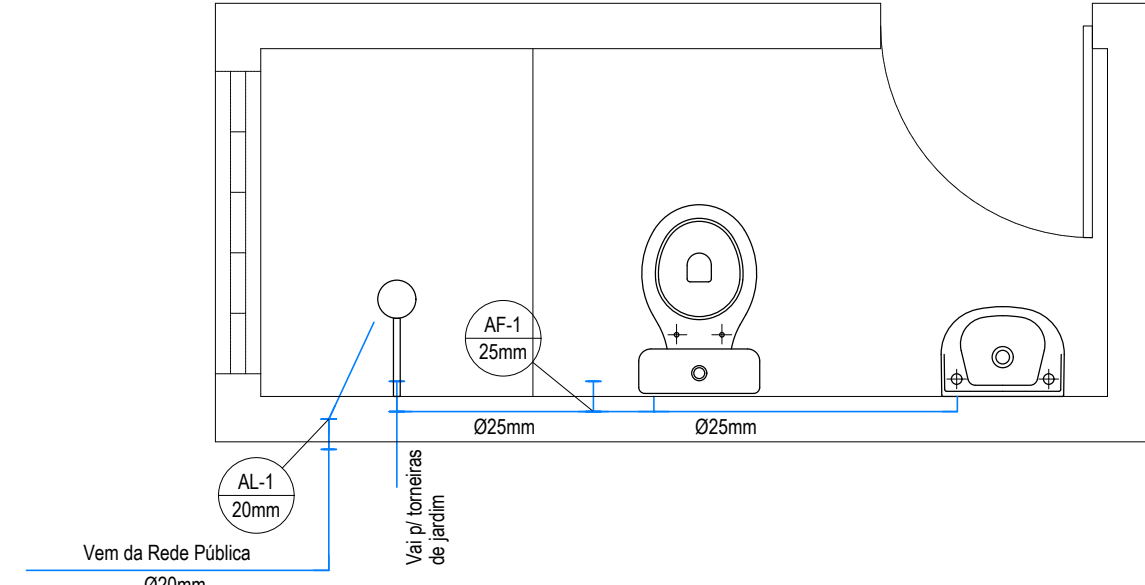

Instalações Hidráulicas - Planta Baixa
Escala 1 : 25

NOTAS

- 01 - Quando não indicado, medidas em metros;
- 02 - Letreiro e logotipo da Compessa deverá ser de acordo com o Manual de Identidade Visual;
- 03 - Quadro de Comando abrigado de baixa/média tensão, utilizando inversores de frequência, conforme NTC-026 / NTC-146, respectivamente, em suas versões mais atualizadas, bem como a Norma GPE-NI-018;
- 04 - Grupo gerador trifásico conforme a NTC-033 mais atualizada.

CÓPIA DIGITAL VÁLIDA

Caso esse documento seja impresso, verificar a vigência na lista mestra.

OBS:
Faixa Azul: 1,00 m a partir da base, cor PANTONE 661C
Faixa Verde: 0,15 m acima da faixa azul, cor PANTONE 360C