


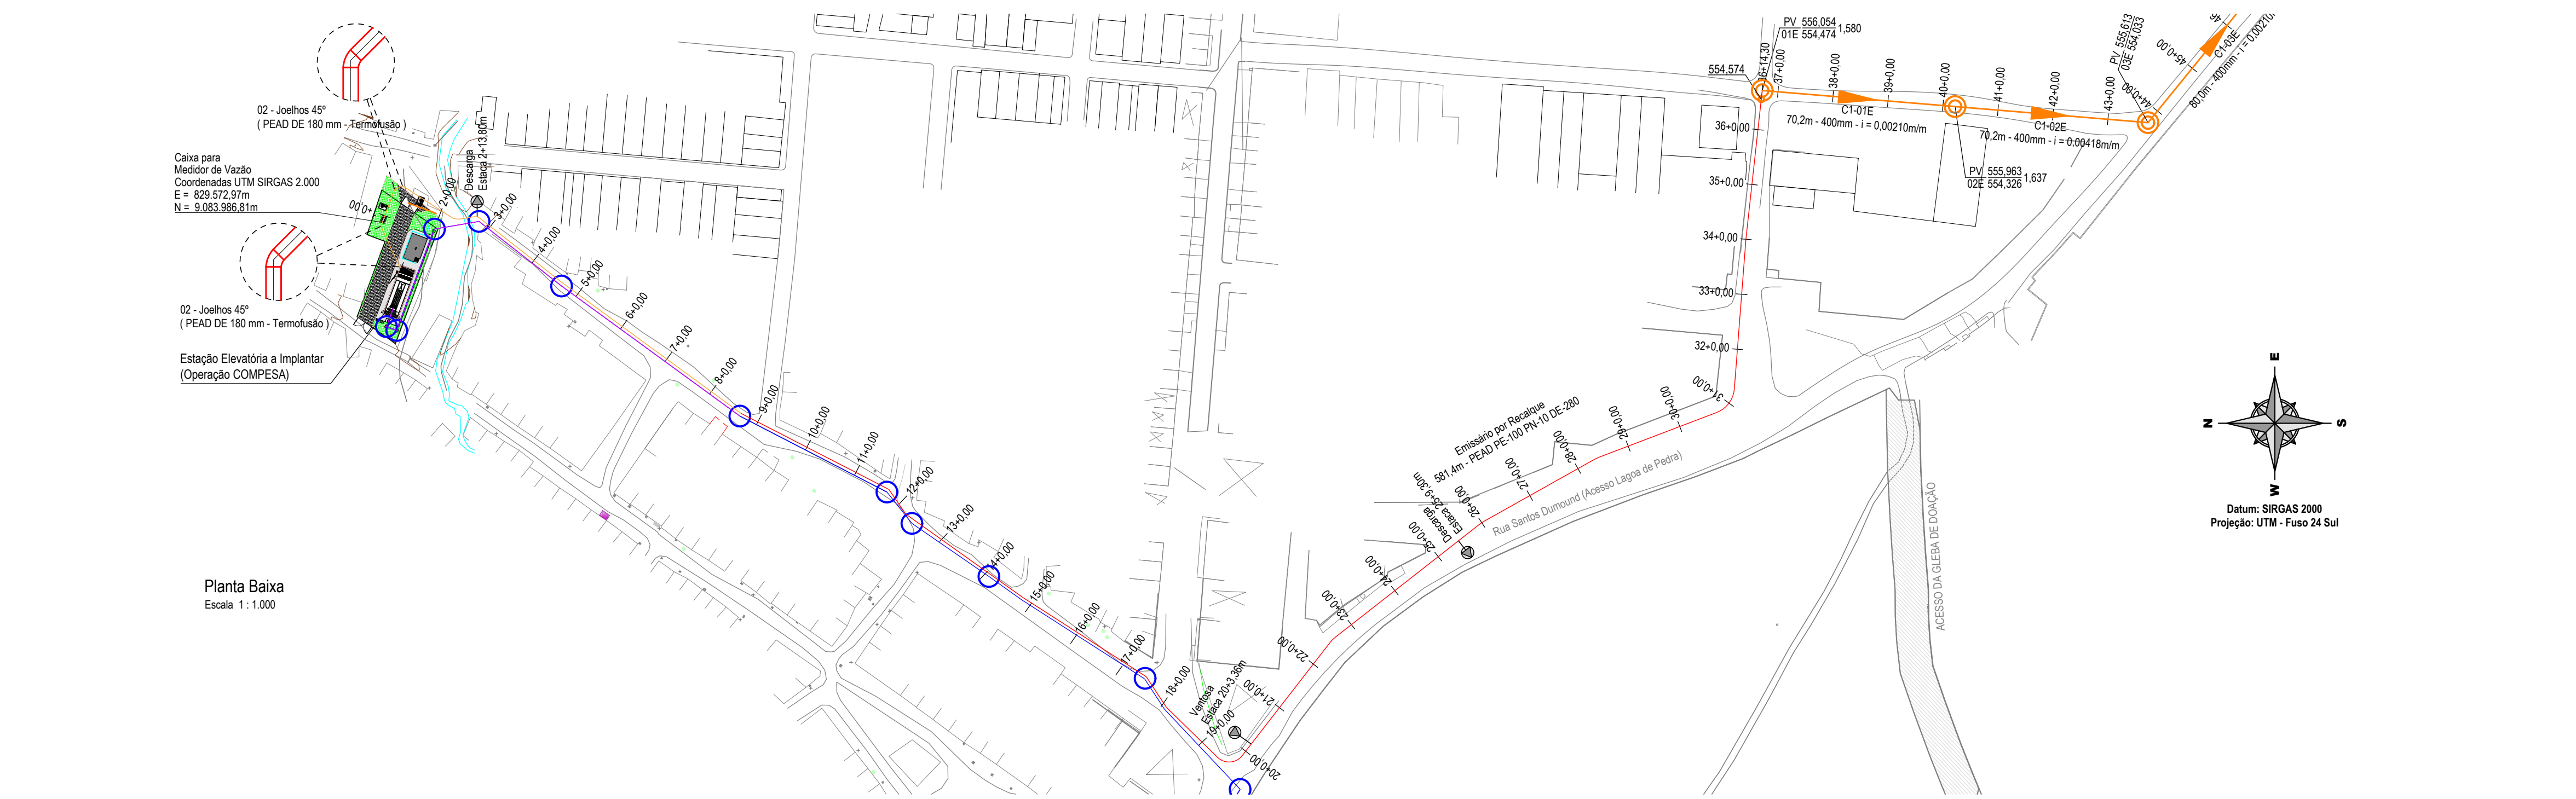

CONVENÇÕES:

Rede Coletora Externa (Operação COMPESA)

Emissário por Recalque (Operação COMPESA)

Rede Coletora Externa (NÃO LIBERADA PARA EXECUÇÃO)

Emissário por Recalque (NÃO LIBERADO PARA EXECUÇÃO)

Emissário por Gravidade a Implantar (Operação COMPESA)

Emissário por Gravidade com Conduto Forçado a Implantar (Operação COMPESA)

Trecho com proteção mecânica

Poço de Visita Emissário (Operação COMPESA)

Poços de Visita Emissário com Rebaixo (Operação COMPESA)

Registros de Manobra do Trecho por Conduto Forçado

Cota da geratriz inferior do tubo de chegada

Cota da geratriz inferior do tubo de chegada

PV

Cota do topo do poço de visita

Numero do PV

Cota da geratriz inferior do tubo


NOTAS:

01 - Quando não indicado, medidas em metros;

02 - Rede coletora, ramais condominiais e emissário por gravidade com tubulação em PVC tipo Coletor Público;

03 - Emissário por recalque com tubulação em PEAD PE-100 PN-10 DE-180;

04 - Emissário pressurizado por gravidade com tubulação em PVC DEFoFo conforme NBR-7665/2020.

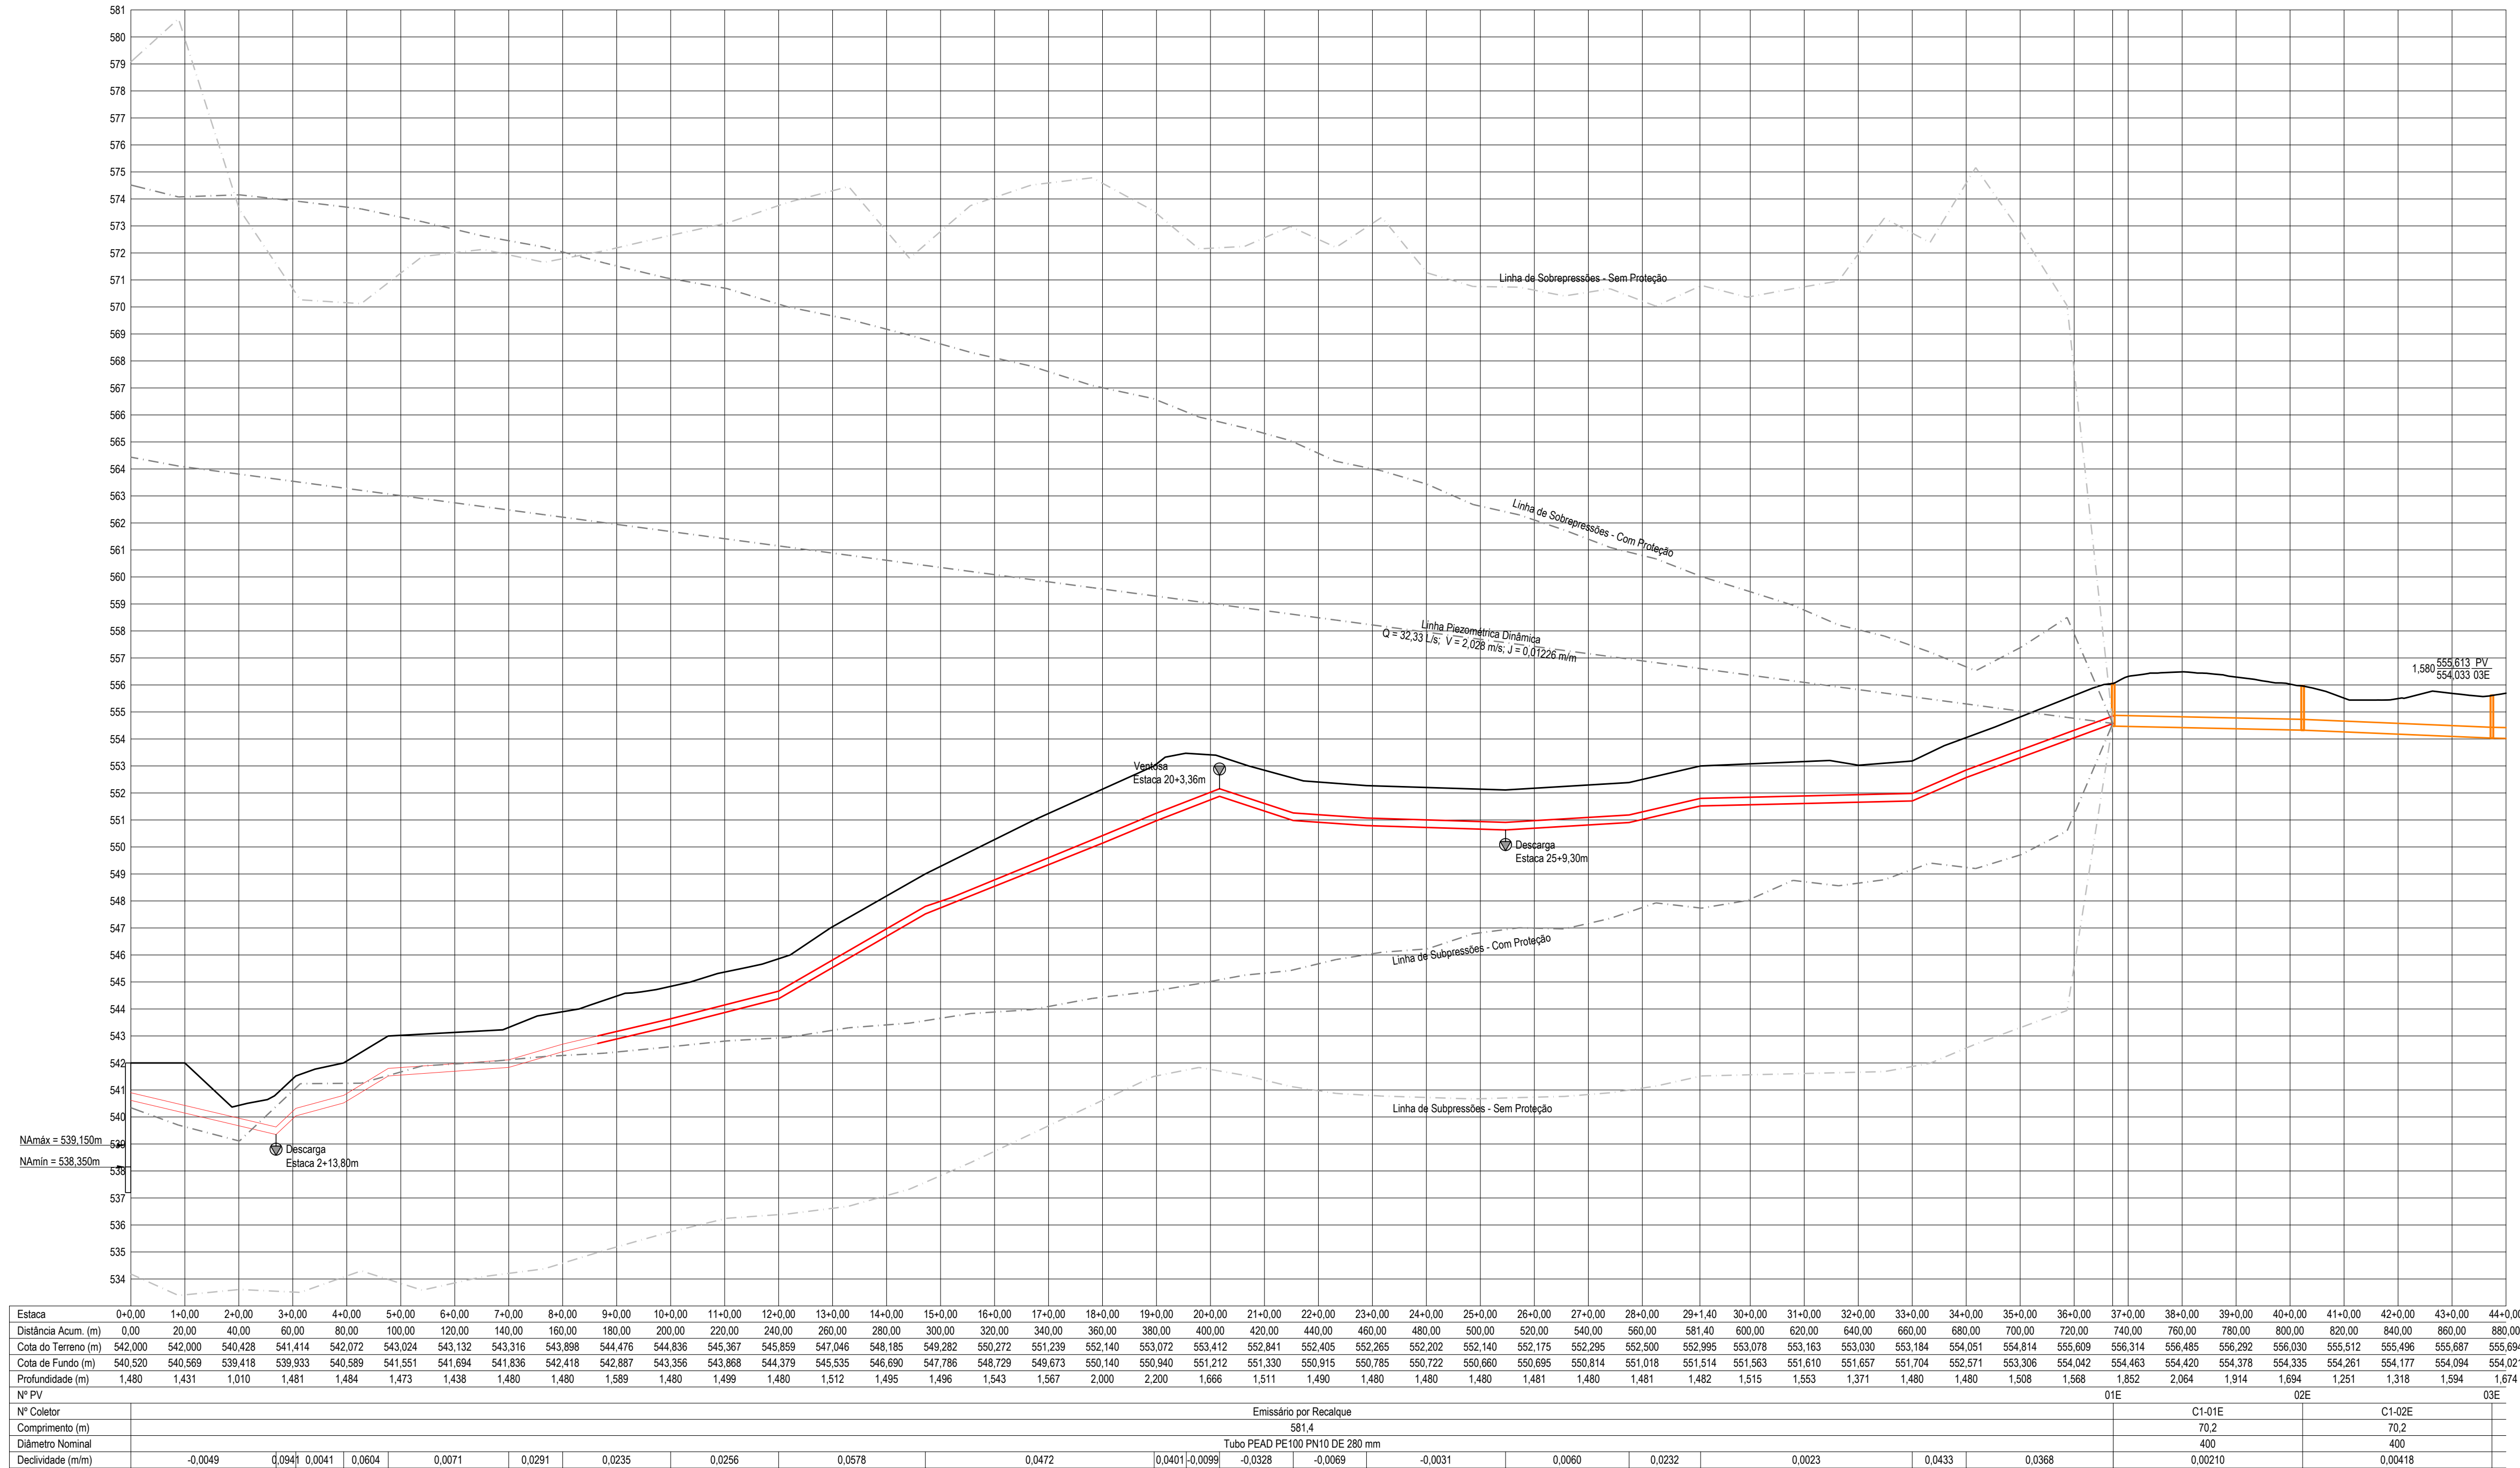

Estaca	0+0,00	1+0,00	2+0,00	3+0,00	4+0,00	5+0,00	6+0,00	7+0,00	8+0,00	9+0,00	10+0,00	11+0,00	12+0,00	13+0,00	14+0,00	15+0,00	16+0,00	17+0,00	18+0,00	19+0,00	20+0,00	21+0,00	22+0,00	23+0,00	24+0,00	25+0,00	26+0,00	27+0,00	28+0,00	29+1,40	30+0,00	31+0,00	32+0,00	33+0,00	34+0,00	35+0,00	36+0,00	37+0,00	38+0,00	39+0,00	40+0,00	41+0,00	42+0,00	43+0,00	44+0,00
Distância Acum. (m)	0,00	20,00	40,00	60,00	80,00	100,00	120,00	140,00	160,00	180,00	200,00	220,00	240,00	260,00	280,00	300,00	320,00	340,00	360,00	380,00	400,00	420,00	440,00	460,00	480,00	500,00	520,00	540,00	560,00	581,40	600,00	620,00	640,00	660,00	680,00	700,00	720,00	740,00	760,00	780,00	800,00	820,00	840,00	860,00	880,00
Cota do Terreno (m)	542,000	542,000	540,428	541,414	542,072	543,024	543,132	543,316	543,898	544,476	544,836	545,367	545,859	547,046	548,185	549,282	550,272	551,239	552,140	553,072	553,412	552,841	552,405	552,265	552,202	552,140	552,175	552,295	552,500	552,995	553,078	553,163	553,030	553,184	554,051	554,814	555,609	556,314	556,485	556,292	556,030	555,512	555,496	555,687	555,694
Cota de Fundo (m)	540,520	540,569	539,418	539,933	540,589	541,551	541,694	541,836	542,418	542,887	543,356	543,868	544,379	545,535	546,690	547,786	548,729	549,673	550,140	550,940	551,212	551,330	550,915	550,785	550,722	550,660	550,695	550,814	551,018	551,514	551,563	551,610	551,657	551,704	552,571	553,306	554,042	554,463	554,420	554,378	554,335	554,261	554,177	554,094	554,021
Profundidade (m)	1,480	1,431	1,010	1,481	1,484	1,473	1,438	1,480	1,480	1,589	1,480	1,499	1,480	1,512	1,495	1,496	1,543	1,567	2,000	2,200	1,666	1,511	1,490	1,480	1,480	1,480	1,481	1,480	1,481	1,482	1,515	1,553	1,371	1,480	1,480	1,508	1,568	1,852	2,064	1,914	1,694	1,251	1,318	1,594	1,674
Nº Coletor	
Comprimento (m)	
Diâmetro Nominal	
Declividade (m/m)	

Perfil do Emissário	
Escala	H - 1 : 1.000;	V - 1 : 100	

CÓPIA DIGITAL VÁLIDA

Caso esse documento seja impresso, verificar a vigência na lista mestra.

PRANCHA

06/12

ASSUNTO

CONDOMÍNIO RECANTO DAS CEREJEIRAS

PLANTA DO EMISSÁRIO

ELABORADO POR:

TÚLIO LINS E ISABELLE FRANÇA

REVISÃO: 01

DATA: 12/03/2026

viana e moura

construções