


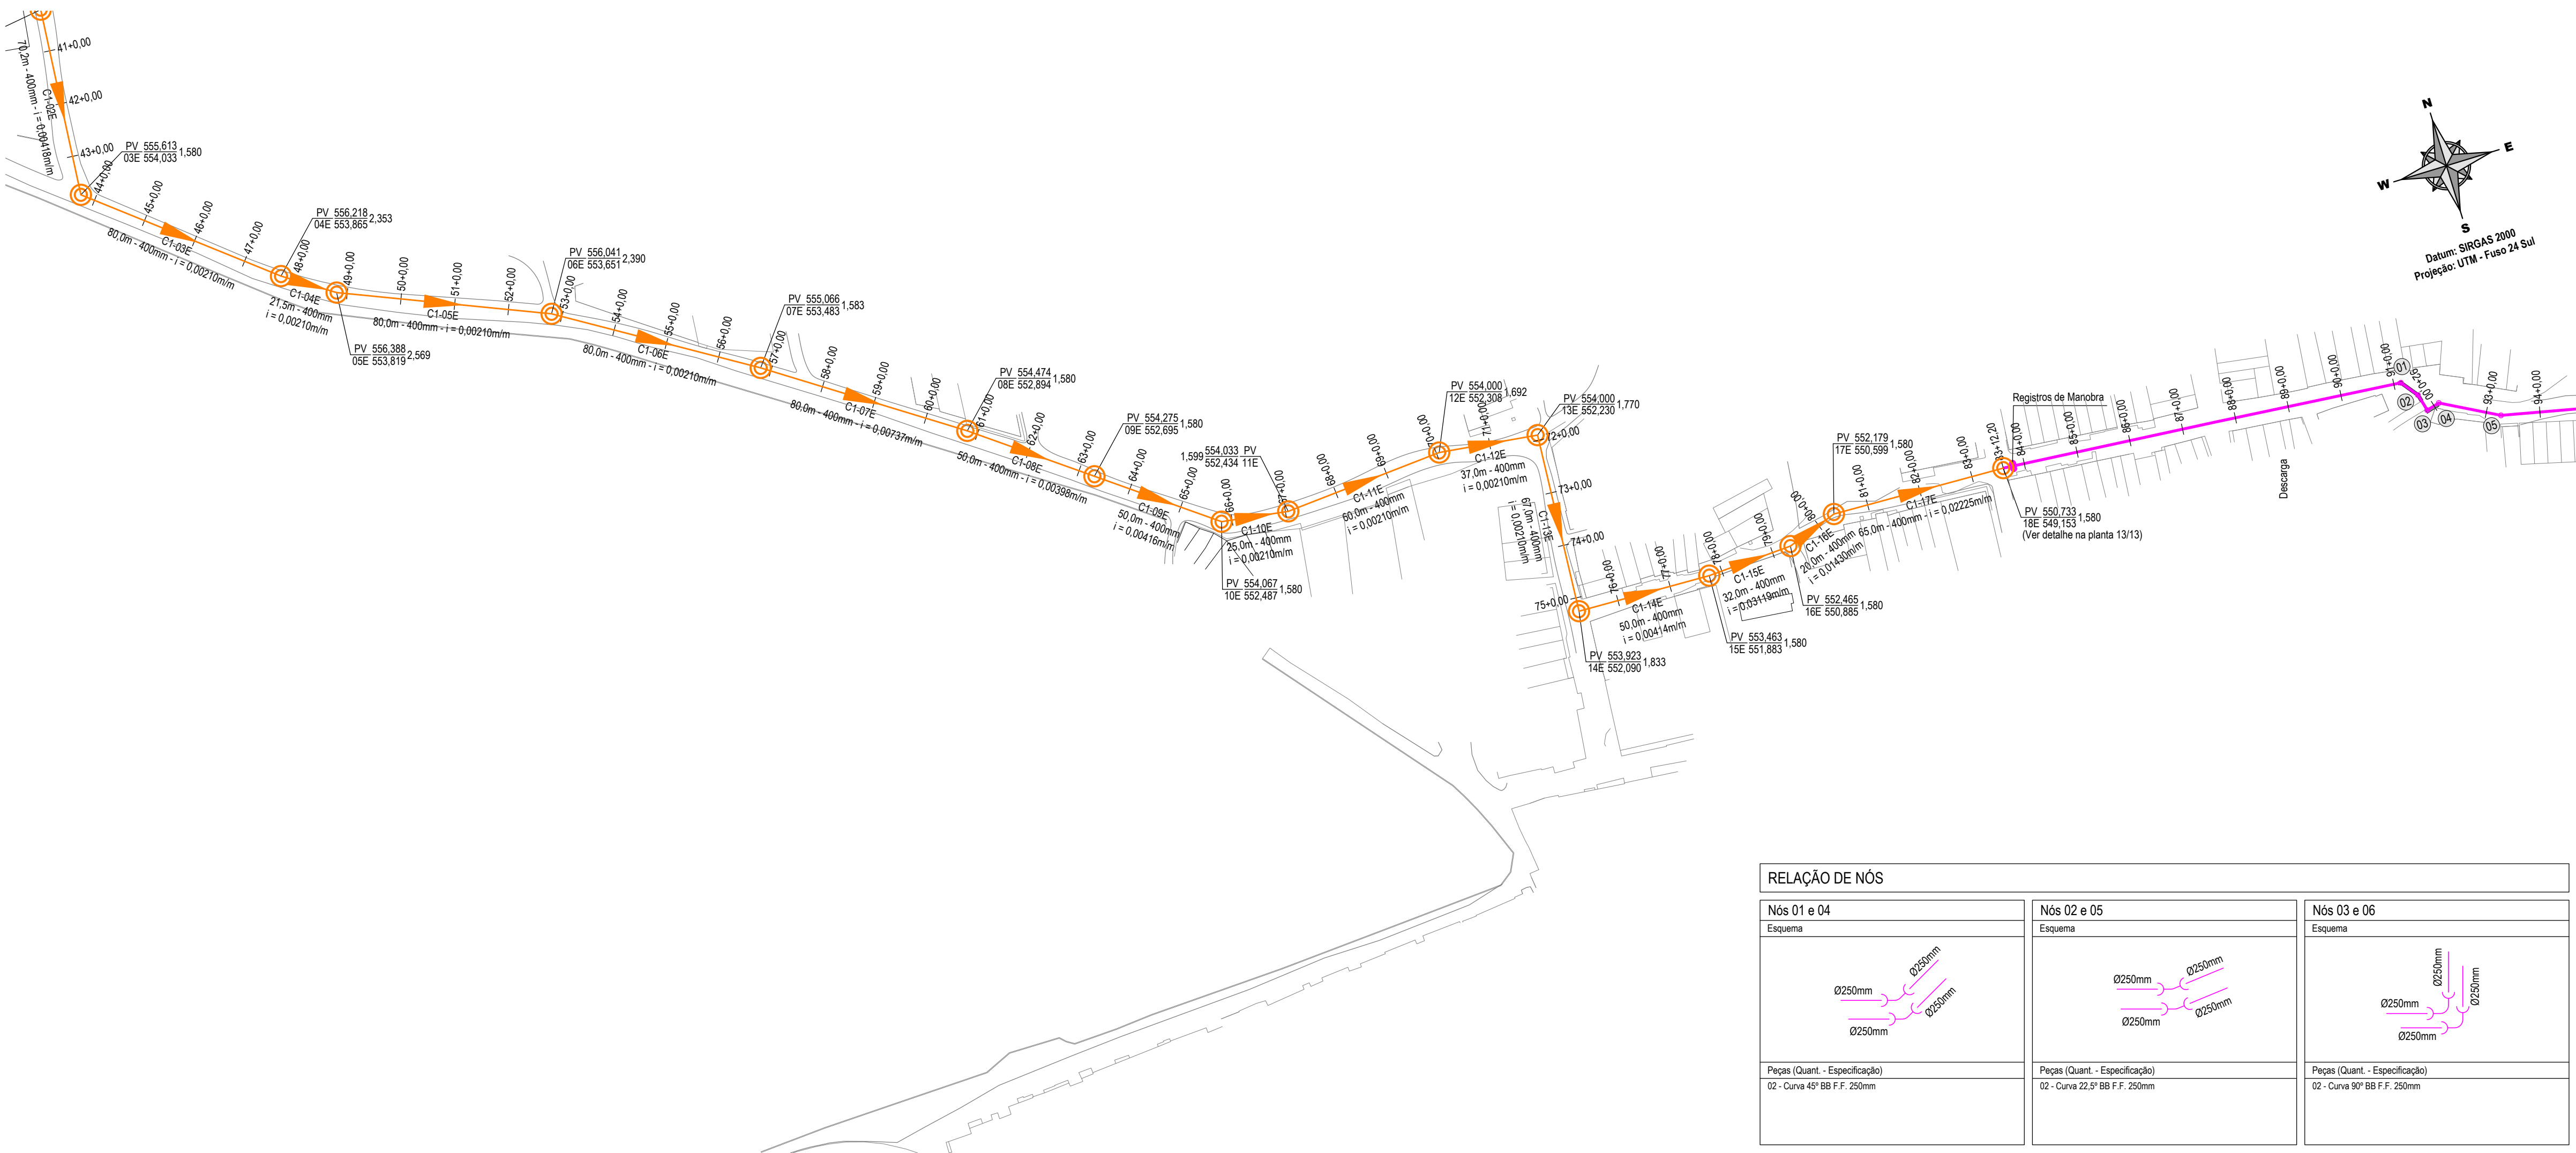

Planta Baixa
Escala 1:1.000

CONVENÇÕES:

Rede Coletora Externa (Operação COMPESA)

Emissário por Recalque (Operação COMPESA)

Emissário por Gravidade a Implantar (Operação COMPESA)

Emissário por Gravidade com Conduto Forçado a Implantar (Operação COMPESA)

Trecho com proteção mecânica

Poço de Visita Emissário (Operação COMPESA)

Poços de Visita Emissário com Rabeixo (Operação COMPESA)

Registros de Manobra do Trecho por Conduto Forçado

Cota da geratriz inferior do tubo de chegada

PV

Cota do topo do poço de visita

Número do PV

Cota da geratriz inferior do tubo

NOTAS:

01 - Quando não indicado, medidas em metros;

02 - Rede coletora, ramais condominiais e emissário por gravidade com tubulação em PVC tipo Coletor Público;

03 - Emissário por recalque com tubulação em PEAD PE-100 PN-10 DE-180;

04 - Emissário pressurizado por gravidade com tubulação em PVC DEFoFo conforme NBR-7665/2020.

BLOCOS DE ANCORAGEM:

Curva 90° - Vista Superior

Sem Escala

Curva 90° - Corte A - A

Sem Escala

Curva 45° - Vista Superior

Sem Escala

Curva 45° - Corte A - A

Sem Escala

Estaca	44+0.00	45+0.00	46+0.00	
Distância Acum. (m)	880.00	900.00	920.00	940.00	960.00	980.00	1000.00	1020.00	1040.00	1060.00	1080.00	1100.00	1120.00	1140.00	1160.00	1180.00	1200.00	1220.00	1240.00	1260.00	1280.00	1300.00	1320.00	1340.00	1360.00	1380.00	1400.00	1420.00	1440.00	1460.00	1480.00	1500.00	1520.00	1540.00	1560.00	1580.00	1600.00	1620.00	1640.00	1660.00	1680.00	1700.00	1720.00	1740.00	1760.00	
Cota do Terreno (m)	555.694	556.004	556.087	556.101	556.260	556.418	556.455	556.308	556.161	556.014	555.502	555.255	555.151	555.047	554.906	554.735	554.564	554.461	554.385	554.302	554.218	554.135	554.062	554.035	554.020	554.000	554.000	554.001	554.000	554.000	554.000	553.983	553.804	553.642	553.303	552.655	552.284	552.000	551.434	550.986	550.552	549.811	547.676	545.850	544.198	
Cota de Fundo (m)	554.021	553.979	553.937	553.896	553.854	553.811	553.769	553.727	553.685	553.644	553.601	553.559	553.517	553.456	553.308	553.161	553.014	552.879	552.800	552.720	552.638	552.555	552.479	552.437	552.395	552.353	552.311	552.269	552.226	552.185	552.143	552.101	552.029	551.946	551.736	551.112	550.703	550.316	549.871	549.426	548.593	547.141	545.689	544.237	542.750	
Profundidade (m)	1.674	2.025	2.150	2.205	2.406	2.607	2.686	2.581	2.476	2.370	1.901	1.696	1.634	1.591	1.597	1.574	1.550	1.562	1.586	1.581	1.580	1.580	1.583	1.596	1.625	1.647	1.689	1.732	1.774	1.714	1.815	1.857	1.882	1.775	1.696	1.567	1.543	1.581	1.684	1.362	1.559	1.959	2.670	1.987	1.613	1.446
Nº PV	C1-03E	
Comprimento (m)	80.0	21.5			80.0	
Diâmetro Nominal	400	400			400	
Declividade (m/m)	0.00210	0.00210			0.00210	

Perfil do Emissário
Escala H-1:1.000, V-1:1.100

CÓPIA DIGITAL VÁLIDA
Caso esse documento seja impresso, verificar a vigência na lista mestra.

PRANCHA

07/12

ASSUNTO

CONDOMÍNIO RECANTO DAS CEREJEIRAS

PLANTA DO EMISSÁRIO

ELABORADO POR:

TÚLIO LINS E ISABELLE FRANÇA

REVISÃO: 01

DATA: 12/03/2026

viana e moura

construções