




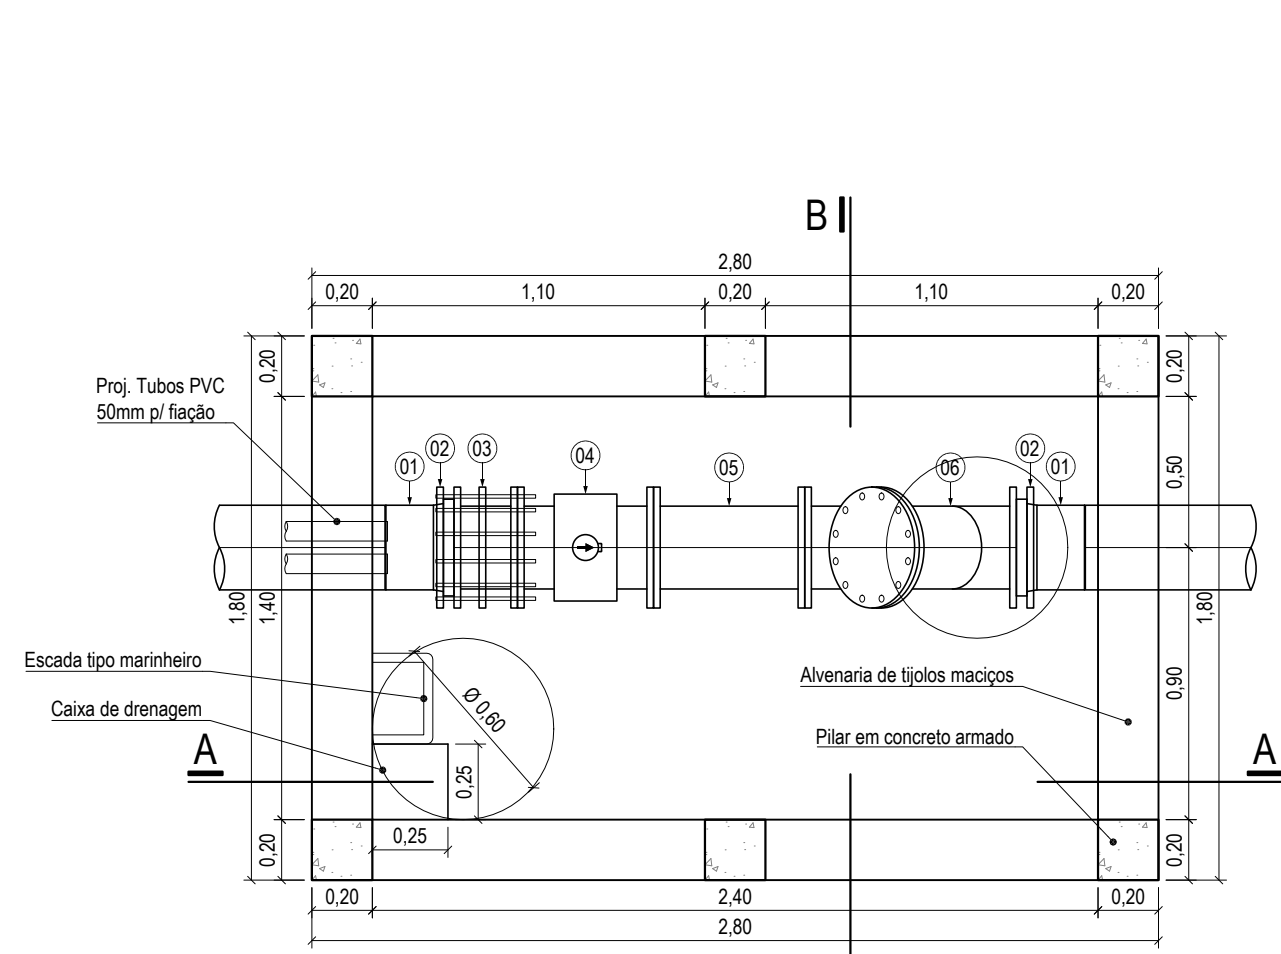


Planta Baixa  
Escala 1 : 25

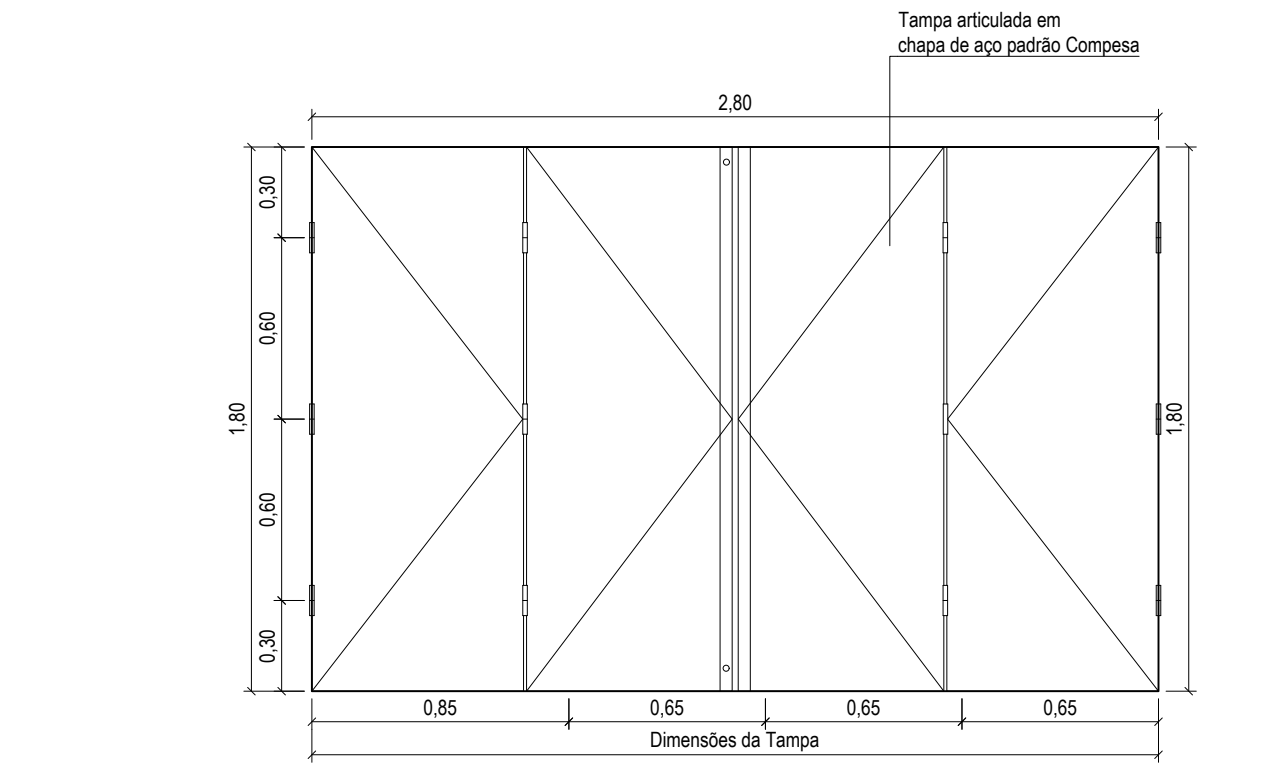


Vista Superior  
Escala 1 : 25

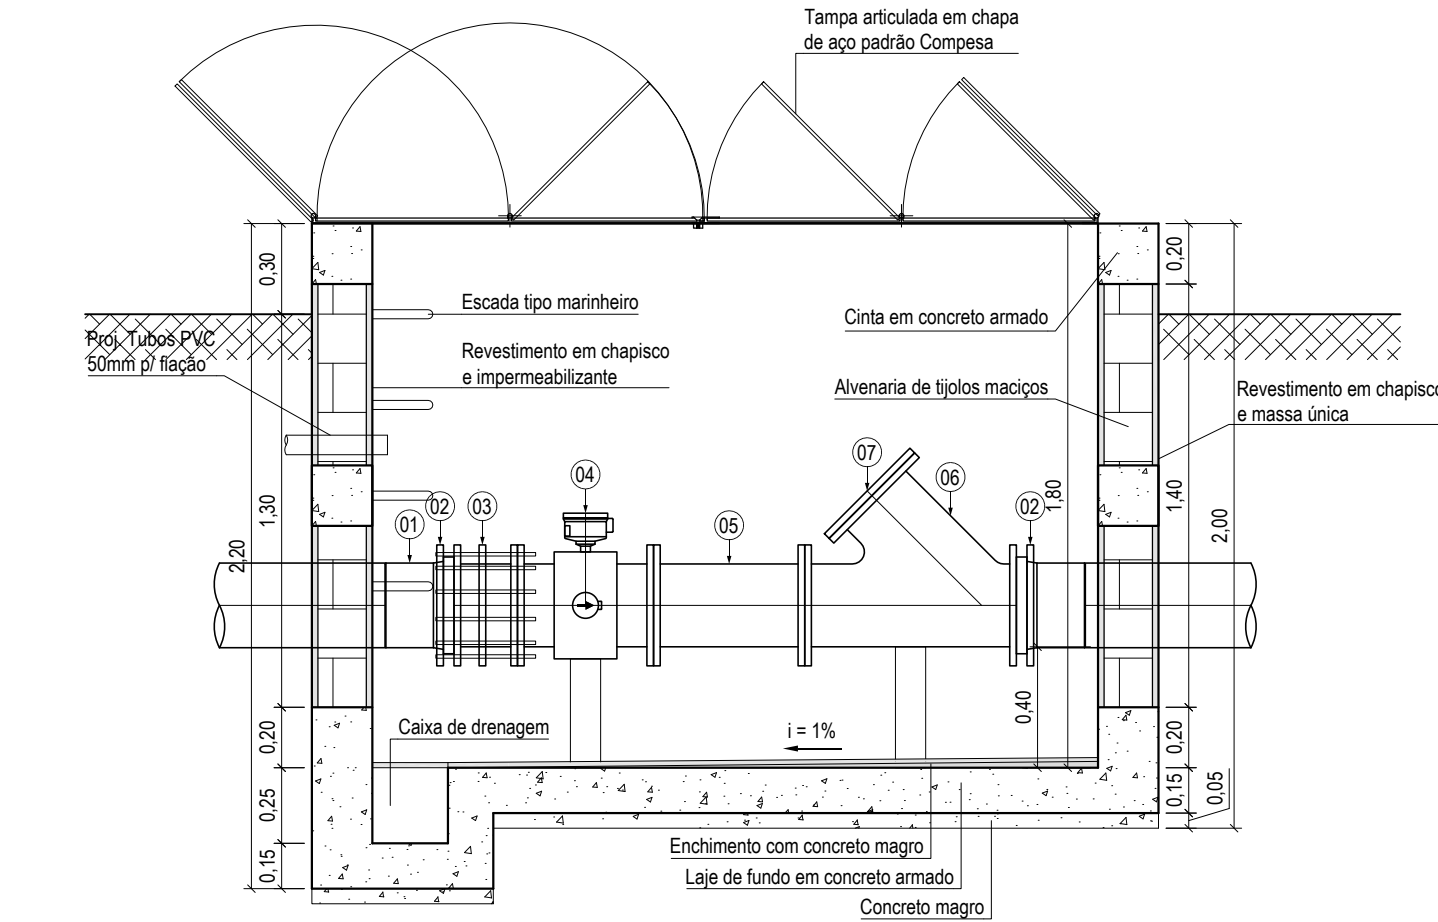

Corte A-A  
Escala 1 : 25

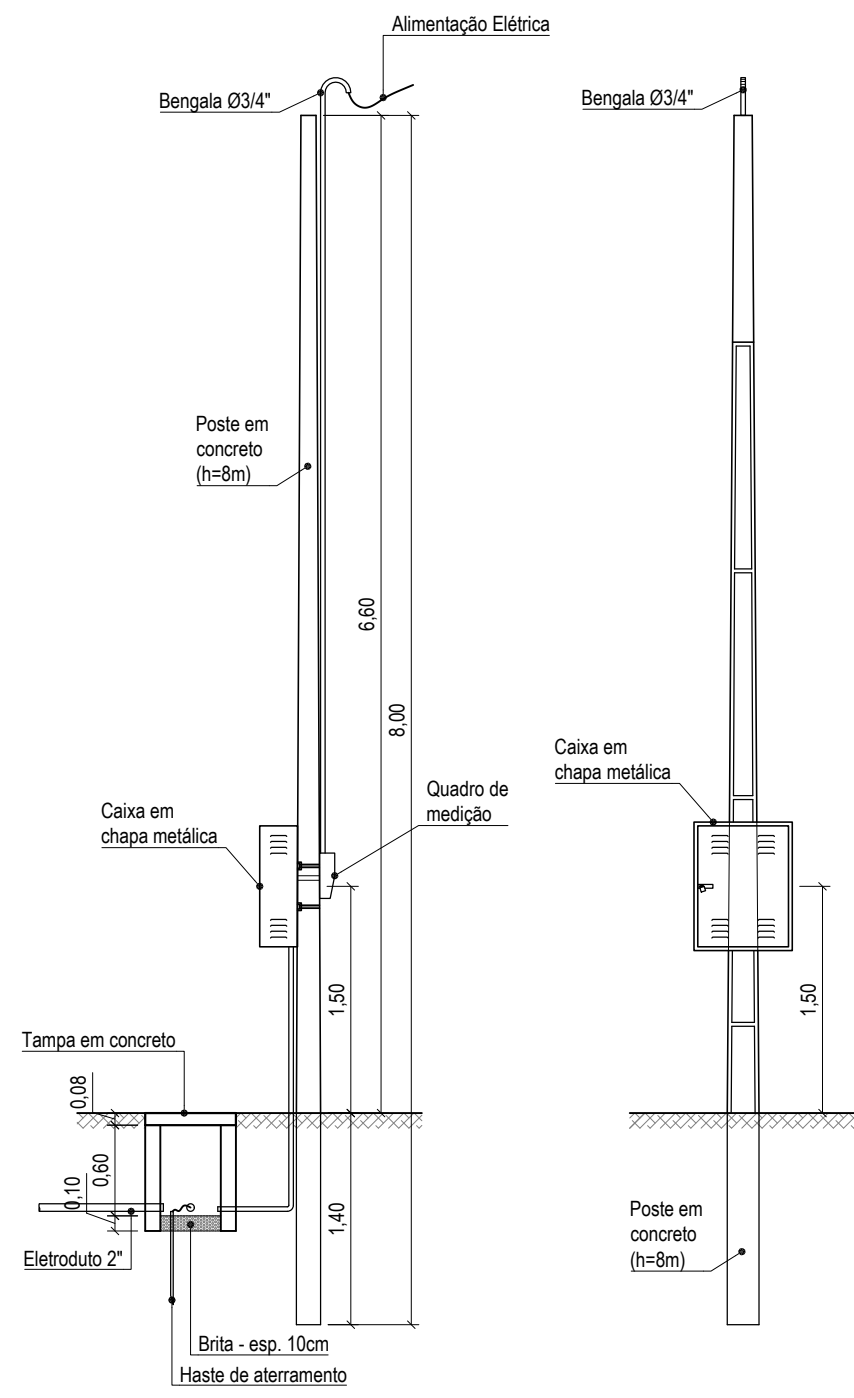


Detalhe do Poste - Vista Lateral e Frontal  
Escala 1 : 50

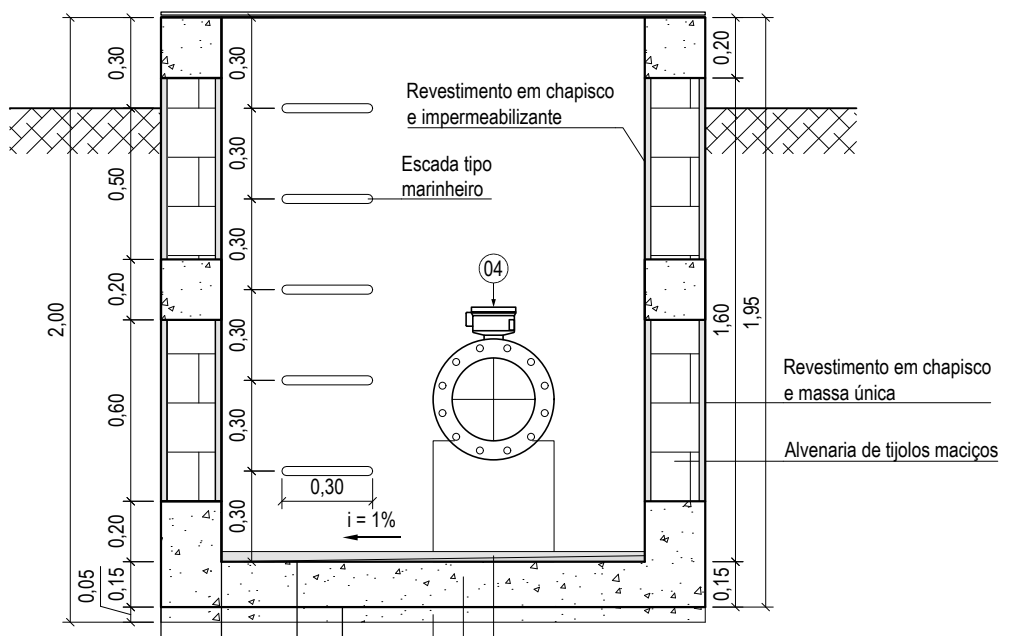


Corte B-B  
Escala 1 : 25

Legenda:


- A - Conversor Vazão
- B - Conjunto de Protetores Contra Surto com Proteção das Partes Vivas
- C - Conjunto Arstop de Sobrepor com Disjuntor de 10 A
- D - Canaleta PVC Aberta (50mmx50mm)

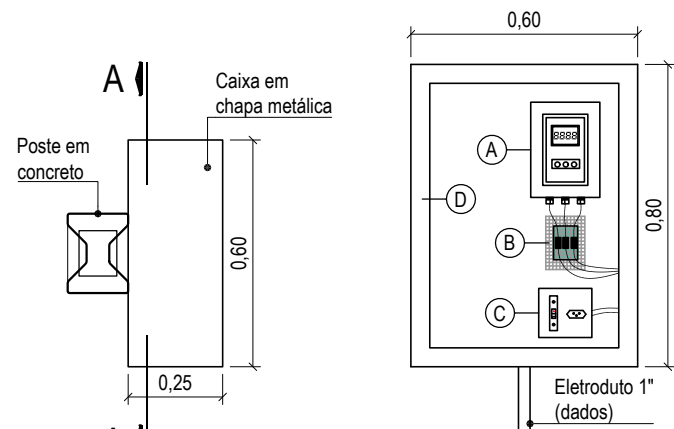

Planta Baixa  
Escala 1 : 20

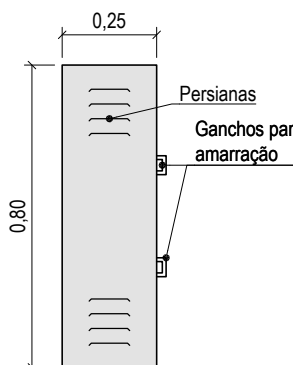


Vista Lateral  
Escala 1 : 20

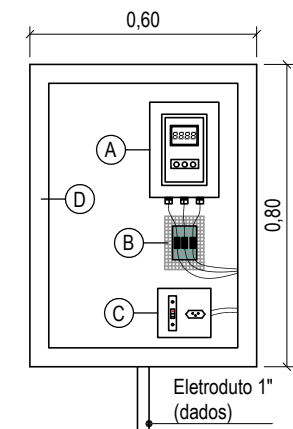

Corte A-A  
Escala 1 : 20



Vista Frontal  
Escala 1 : 20

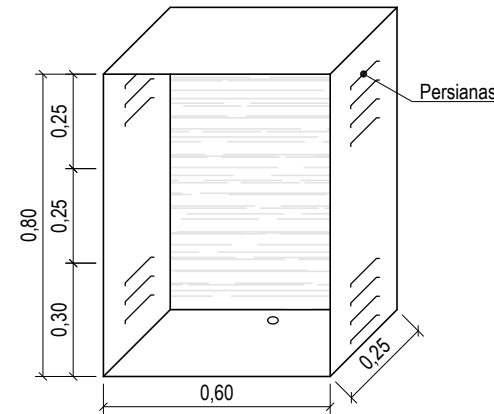

Perspectiva  
Escala 1 : 20

| RELAÇÃO DE PEÇAS |          |    |     |    |                                                           |           |
|------------------|----------|----|-----|----|-----------------------------------------------------------|-----------|
| Item             | Material | PN | DN  | dn | Descrição                                                 | Comp (mm) |
| 01               | PEAD     | 10 | 280 | -  | Colarinho para PEAD termofusão                            | -         |
| 02               | Aço      | 10 | 250 | -  | Franga avulso para PEAD                                   | -         |
| 03               | FoFo     | 10 | 250 | -  | Junta de desmontagem travada axialmente                   | -         |
| 04               | FoFo     | 10 | 250 | -  | Medidor de vazão eletromagnético                          | -         |
| 05               | FoFo     | 10 | 250 | -  | Toco com flanges                                          | 500       |
| 06               | FoFo     | 10 | 250 | -  | Junção para a colocação do raspador de arraste hidráulico | -         |
| 07               | PEAD     | 10 | 250 | -  | Flange cego                                               | -         |
| -                | -        | 10 | 250 | -  | Arruela de borracha para flange                           | -         |
| -                | -        | -  | -   | -  | Parafuso com porca 20x90                                  | -         |

NOTAS

- 1 - Escada de Marinheiro deve ser confeccionada em aço CA 50 com diâmetro maior ou igual a 3/4"
- 2 - Concreto armado com fck > 25 MPa
- 3 - Concreto simples com fck > 15 MPa
- 4 - Massa única deve ter espessura de 2cm, com adição de aditivo impermeabilizante
- 5 - Sobre o revestimento externo, aplicar pintura impermeabilizante flexível
- 6 - Nos locais onde seja possível, deve-se prolongar a parede 30 cm acima do nível do piso
- 7 - Conferir medidas no local
- 8 - Recomenda-se o uso de tijolos maciços
- 9 - Quando não indicado, medidas em metros
- 10 - Todas as peças e equipamentos são para uso em esgoto

CÓPIA DIGITAL VÁLIDA  
Caso esse documento seja impresso, verificar a vigência na lista mestra.