



POÇO DE VISITA - TIPO 01 (PROFUNDIDADE ATÉ 1,80m)
ESCALA: 1:25
(MEDIDAS EM M)

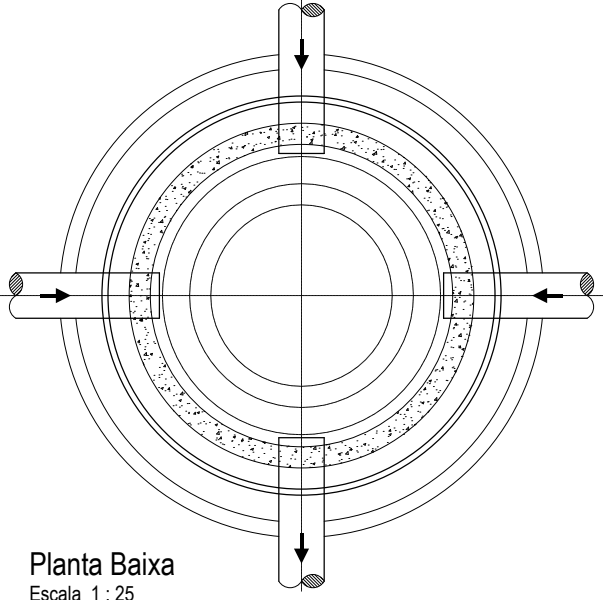


Planta Baixa
Escala 1:25

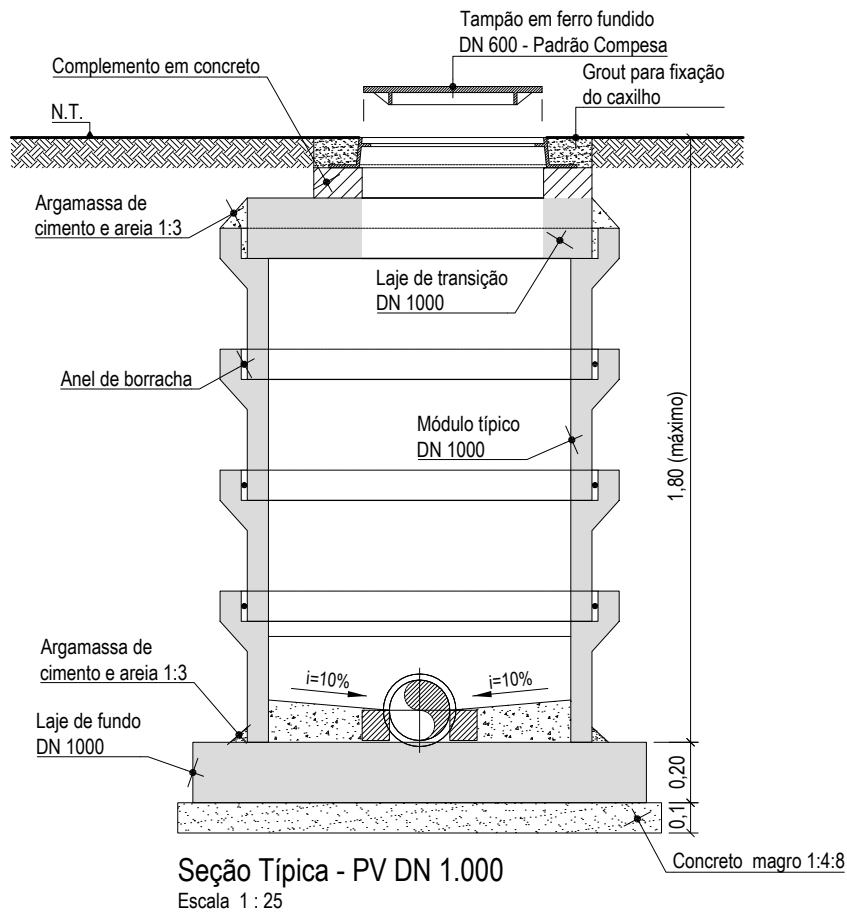


Seção Típica - PV DN 1.000
Escala 1:25


CAIXA DE PASSAGEM EM ANÉIS PRÉ-MOLDADOS ATÉ 1,00m DE PROFUNDIDADE
ESCALA: 1:12,5

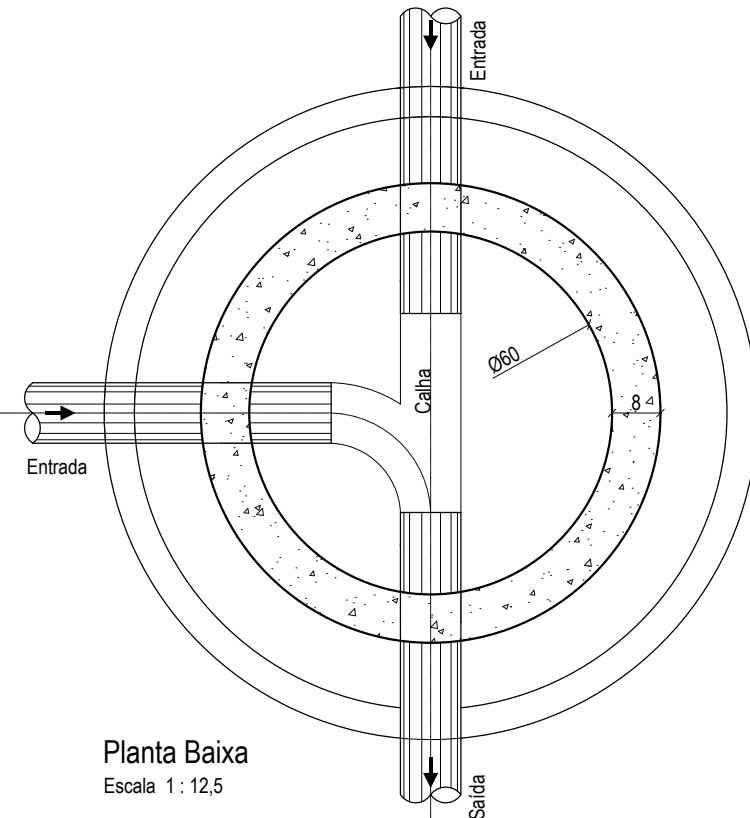


Planta Baixa
Escala 1:12,5

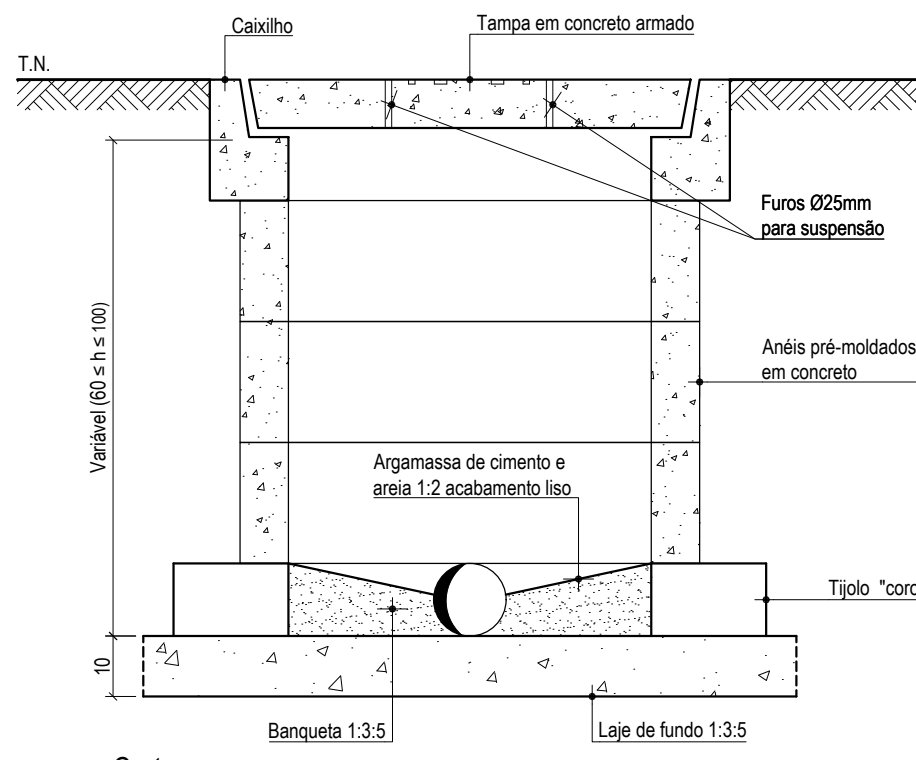


Corte
Escala 1:12,5

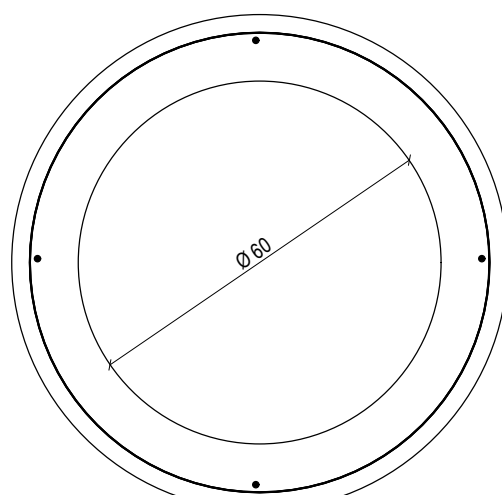


Detalhe do Anel - Planta
Escala 1:12,5

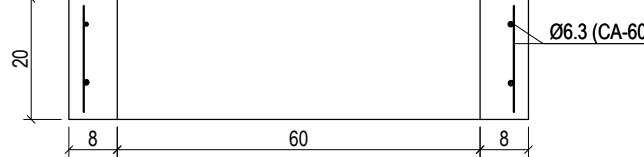

Detalhe do Anel - Corte
Escala 1:12,5

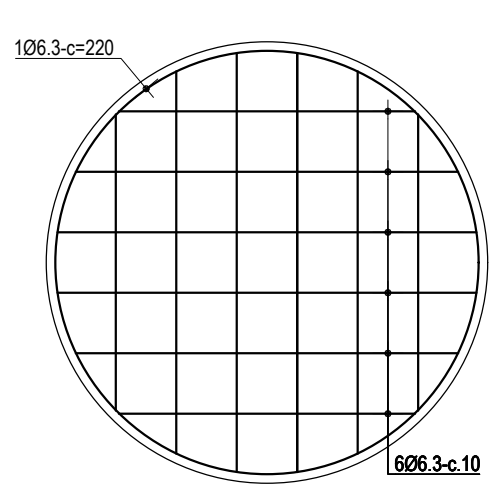


Detalhe da Tampa - Planta
Escala 1:12,5

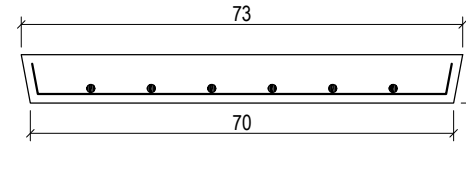


Detalhe da Tampa - Corte
Escala 1:12,5

DETALHE 2: TÍPICO FUNDO DO POÇO DE VISITA COM MAIS DE UMA ENTRADA
ESCALA: 1:25

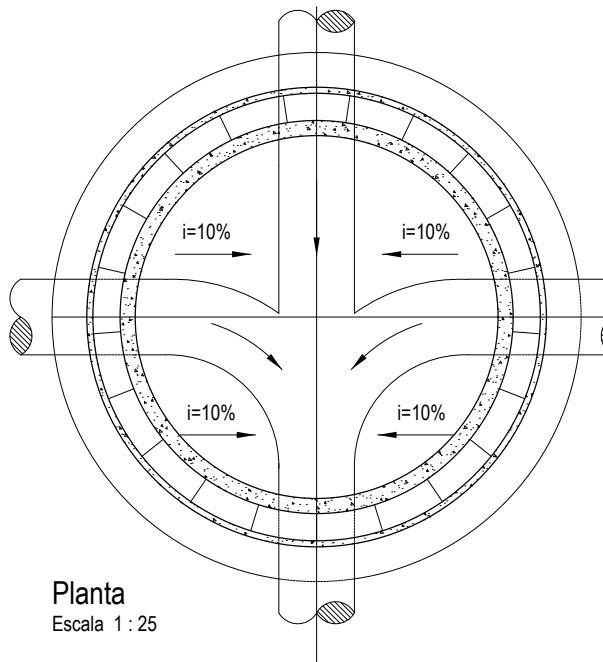


Planta
Escala 1:25

TAMPA DE POÇO DE VISITA
ESCALA: 1:12,5
(MEDIDAS EM CM)

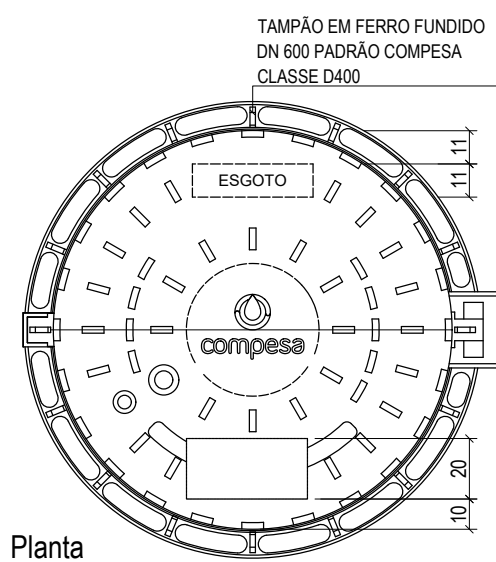


Planta
Escala 1:12,5

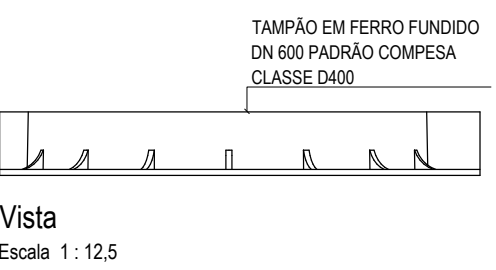


Vista
Escala 1:12,5


DETALHE DAS CONCORDÂNCIAS DAS CALHAS
SEM ESCALA

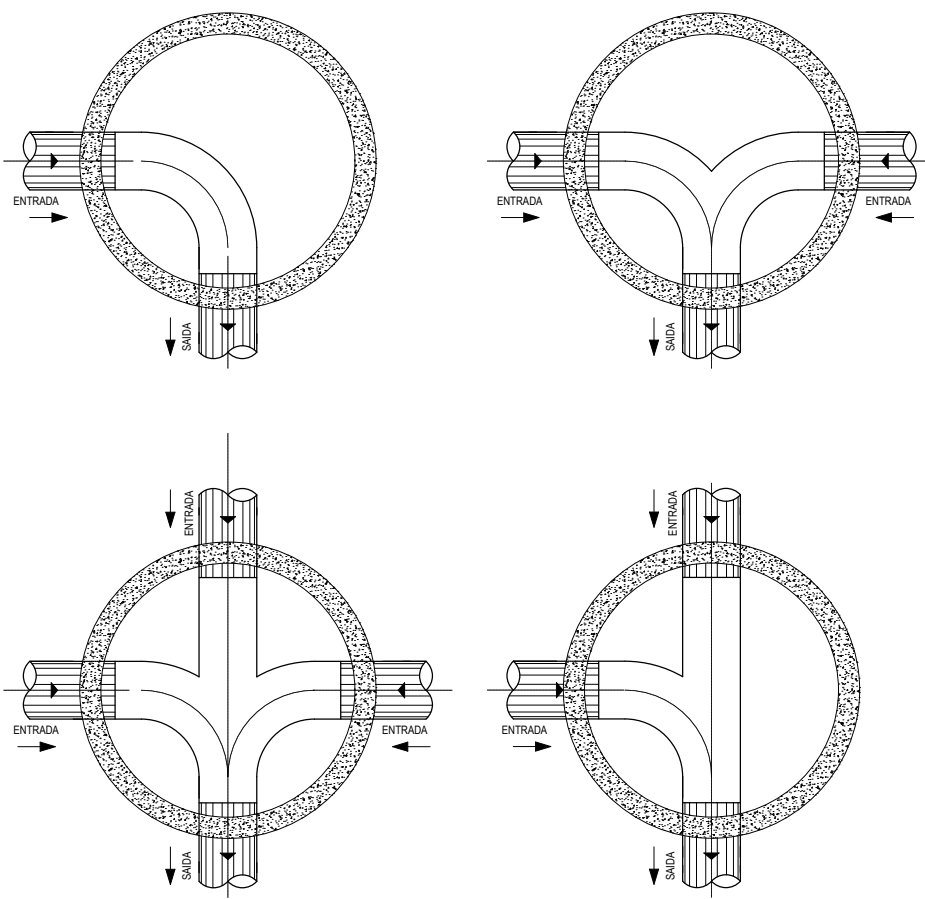


DETALHE DA LAJE DE FUNDO DN 1000
ESCALA: 1:12,5
(MEDIDAS EM CM)

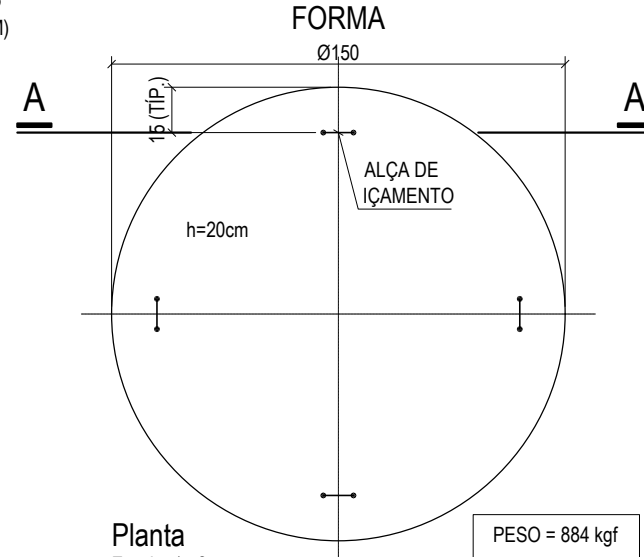

Planta
Escala 1:25

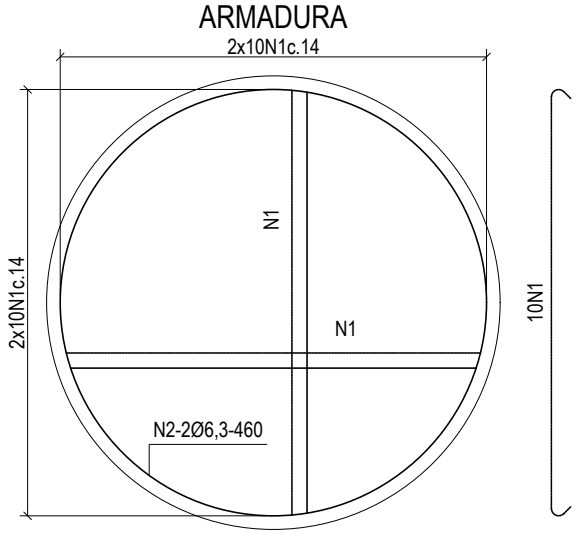

Planta
Escala 1:25

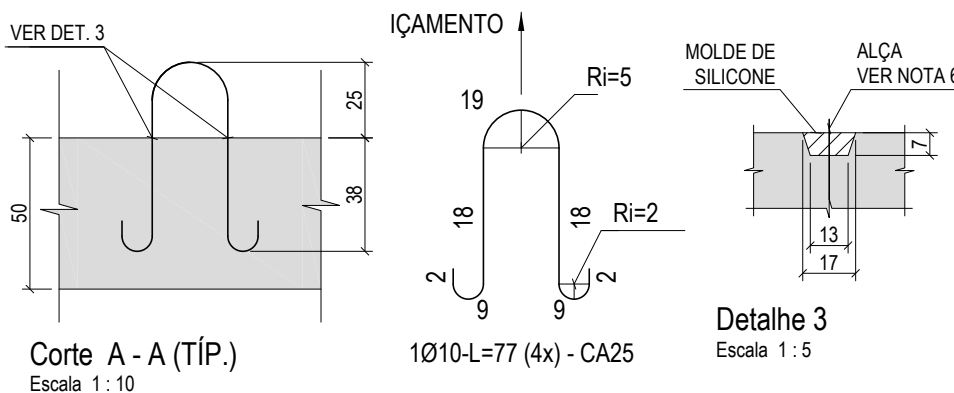


Corte A - A (TÍP.)
Escala 1:10


LAJES DE FUNDO DN 1000				
LISTA DE BARRAS				
N	Ø (mm)	QUANT.	UNITÁRIO (cm)	TOTAL (m)
1	10	40	VAR	52
2	6,3	2	460	9

RESUMO			
Ø (mm)	COMPRIMENTO (m)	kg/m	M. PARCIAL (kg)
6,3	9	0,25	2
10	52	0,63	33
MASSA TOTAL (kg)			35


MÓDULOS TÍPICOS E ANÉIS DE AJUSTE
ESCALA: 1:25
(MEDIDAS EM CM)

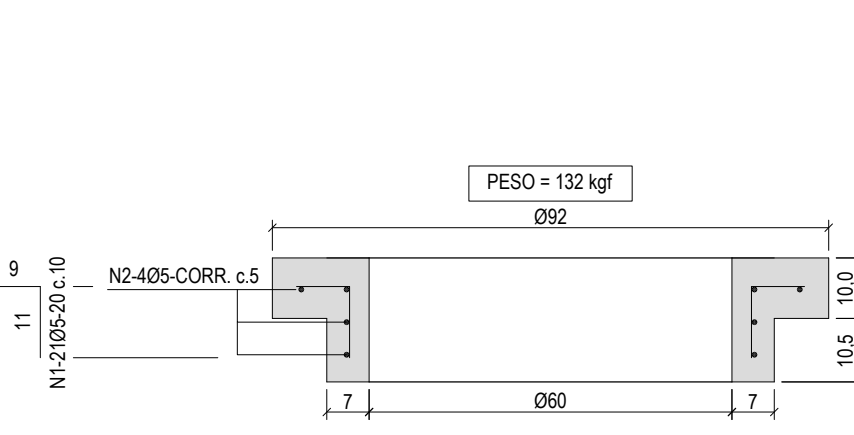

Anel de Ajuste - PV DN 600 (Ponta e Bolsa)
Escala 1:10

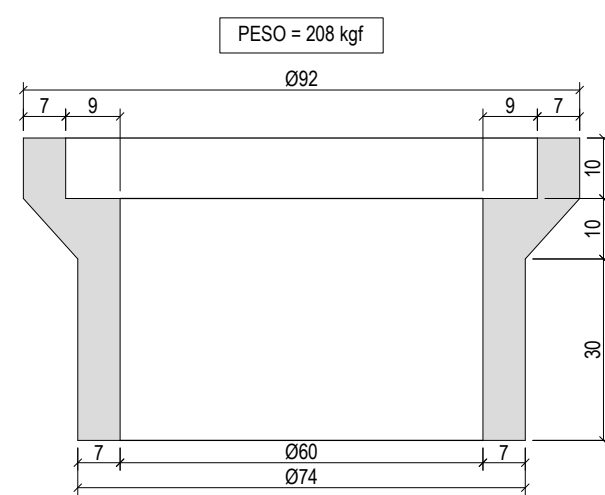


Módulo Típico - PV DN 600 (Ponta e Bolsa)
Escala 1:10

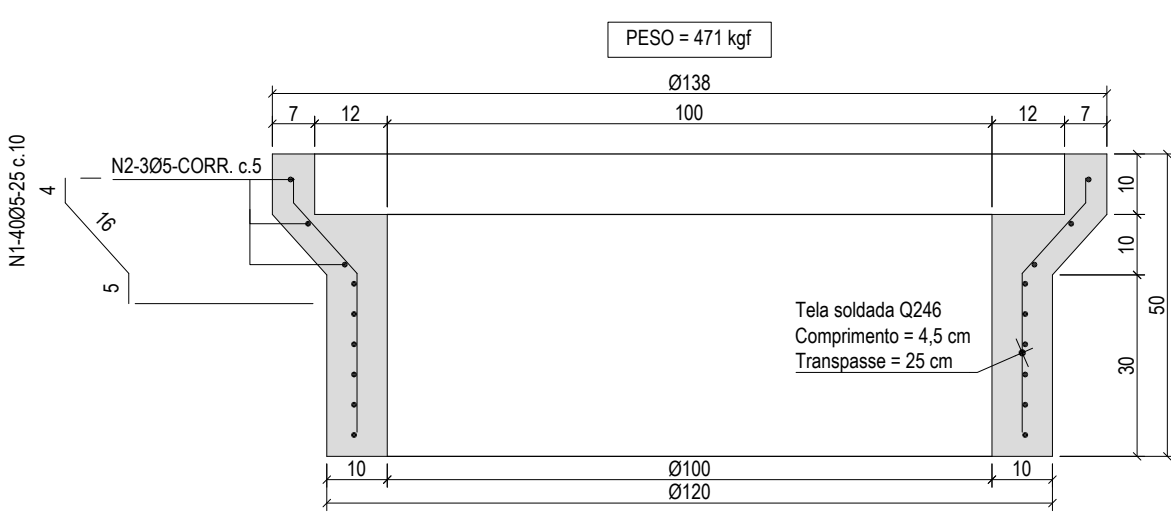


Módulo Típico - PV DN 1.000 (Ponta e Bolsa)
Escala 1:12,5


DETALHE DA LAJE DE TRANSIÇÃO DN 1000
ESCALA: 1:12,5
(MEDIDAS EM CM)

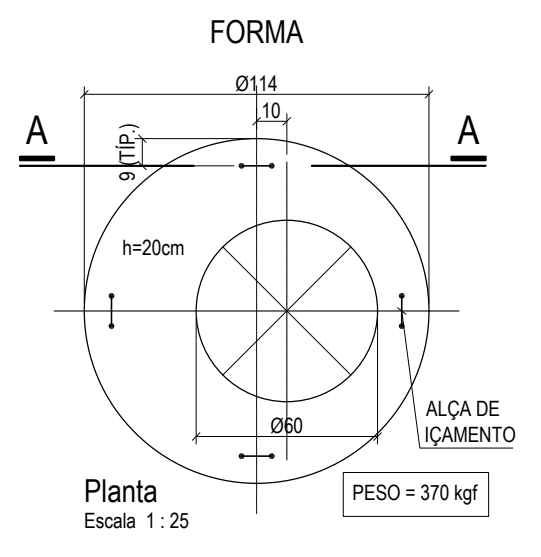

Planta
Escala 1:25

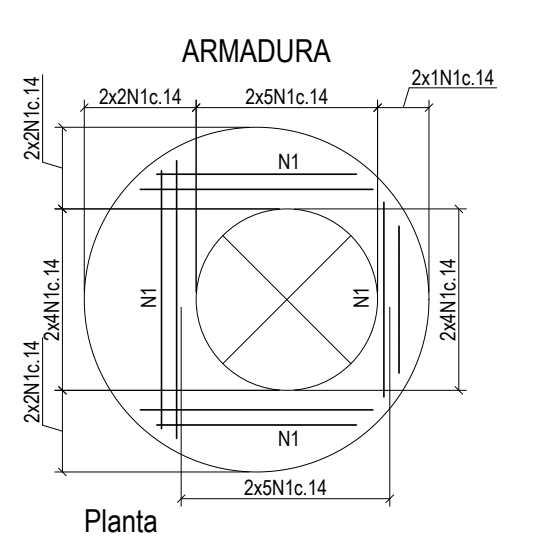

Planta
Escala 1:25

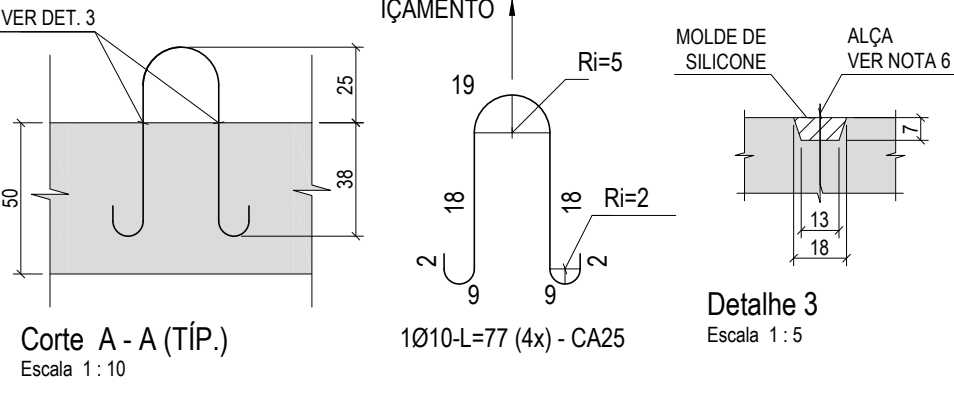


Corte A - A (TÍP.)
Escala 1:10

LAJES DE TRANSIÇÃO DN 1000				
LISTA DE BARRAS				
N	Ø (mm)	QUANT.	UNITÁRIO (cm)	TOTAL (m)
1	10	50	VAR	28
2	10	16	VAR	17


RESUMO			
Ø (mm)	COMPRIMENTO (m)	kg/m	M. PARCIAL (kg)
10	45	0,63	29
MASSA TOTAL (kg)			29

REFORÇO DAS ABERTURAS
DETALHE TÍPICO

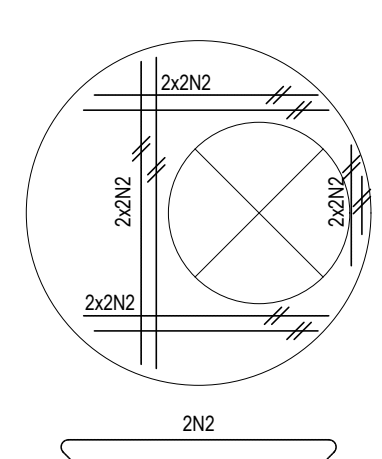

Planta
Escala 1:25

DETALHES DAS VALAS DE ESCAVAÇÃO:

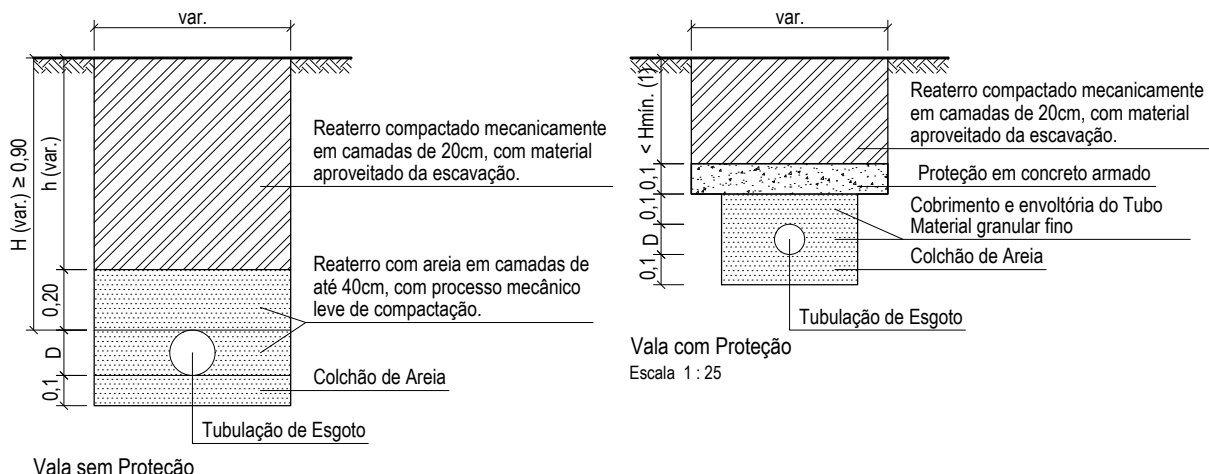

Vala sem Proteção
Escala 1:25


Vala com Proteção
Escala 1:25

Observações:
1 - Altura Total de Recobrimento Mínimo (H_{rec}): 0,90m em vias urbanas;
2 - Utilizar na última camada solo igual ao do terreno adjacente;
3 - Reposição de pavimento com características iguais ao existente;
4 - O material a ser reaproveitado para reaterro deverá ser isento de entulhos, pedras e matéria orgânica. Deverá ser feita uma avaliação visual para sua validação, sendo descartado o material impróprio e utilizado material de empréstimo quando necessário.

DETALHE DA IMPERMEABILIZAÇÃO
ESCALA: 1:25

REVESTIMENTO DE CIMENTO POLIMÉRICO VIAPLUS PROTEC RS (OU SIMILAR)

EMULSÃO ASFÁLTICA BETUFURO (OU SIMILAR) OU REVESTIMENTO DE CIMENTO POLIMÉRICO VIAPLUS PROTEC RS (OU SIMILAR)

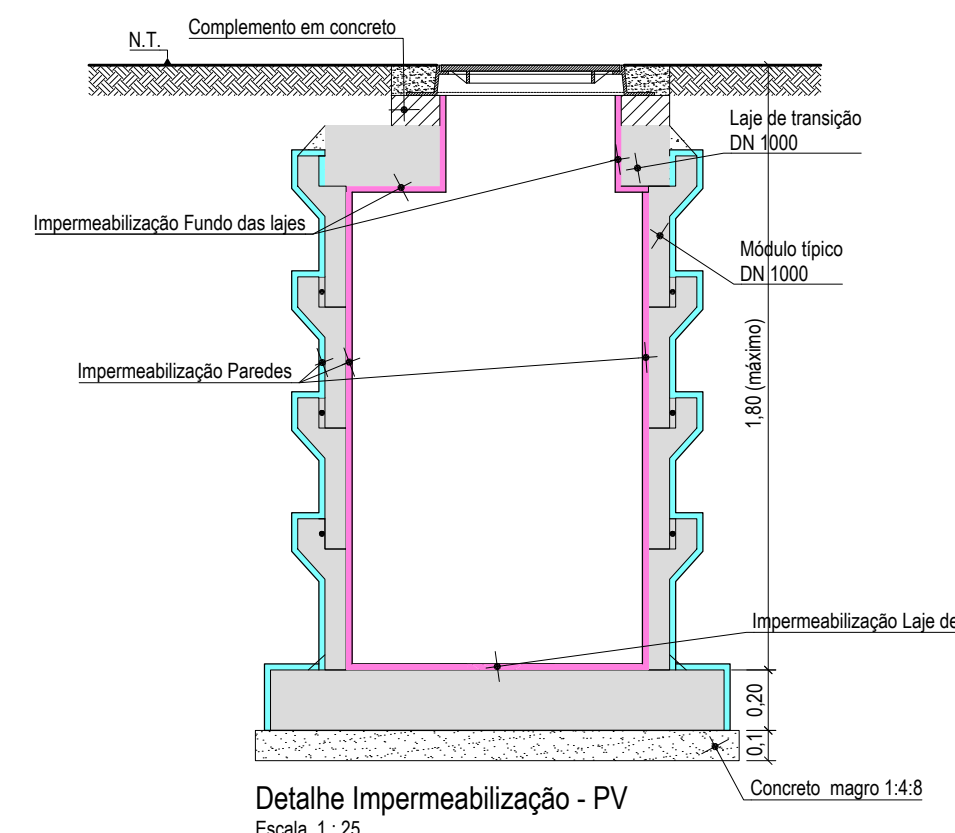

Detalhe Impermeabilização - PV
Escala 1:25

NOTAS GERAIS:

- 1 - MEDIDAS EM METROS, DIÂMETROS DAS BARRAS EM MILÍMETRO, EXCETO ONDE INDICADO
- 2 - MATERIAIS:
CONCRETO ESTRUTURAL
fck=40MPa; FATOR AC=50,45
CONSUMO MÍNIMO DE CIMENTO = 450kg/m³
DIMENSÃO MÁXIMA CARACTERÍSTICA DO AGREGADO GRAUADO = 19mm (VER NBR-7211)
AÇO - CA50
AÇO - CA25 (PARA ALÇAS)
3 - PARA A EXECUÇÃO, SEGUIR AS PRESCRIÇÕES DAS NORMAS:
NBR-6118 - PROJETO DE ESTRUTURAS DE CONCRETO - PROCEDIMENTO
NBR-9062 - PROJETO E EXECUÇÃO DE ESTRUTURAS DE CONCRETO PRÉ-MOLDADO
NBR-6122 - PROJETO E EXECUÇÃO DE FUNDAÇÕES
NBR-7170 - TUBO MACIÇO CERÂMICO PARA ALVENARIA
4 - IMPERMEABILIZAÇÃO DA ESTRUTURA:
A APLICAÇÃO DEVE SEGUIR RIGOROSAMENTE AS ESPECIFICAÇÕES DO FABRICANTE E DETALHES DE PROJETO. EM CASO DE SUBSTITUIÇÃO DE MATERIAIS OU FORNECEDORES, É OBRIGATÓRIA A VERIFICAÇÃO DE COMPATIBILIDADE QUÍMICA PARA GARANTIR A RESISTÊNCIA E DURABILIDADE EM CONTATO PERMANENTE COM EFLUENTES/ESGOTO.
5 - TENSÃO ADMISSÍVEL ADOTADA PARA O TERRENO = 100 kPa. ESTA TENSÃO ADMISSÍVEL DEVERÁ SER CONFIRMADA POR ENGENHEIRO ESPECIALISTA EM FUNDAÇÕES ANTES DA EXECUÇÃO DO COLCHÃO DE AREIA.
6 - APÓS A MONTAGEM DAS PEÇAS, RETIRAR O SILICONE, CORTAR AS ALÇAS E PREENCHER AS CAVIDADES COM ARGAMASSA DE CIMENTO-AREIA (1:3)
7 - COBRIMENTO DAS ARMADURAS = 4,5cm, EXCETO ONDE INDICADO
8 - AS ARESTAS DA PEÇA DE CONCRETO PRÉ-MOLDADO DEVERÃO SER CHANFRADAS EM 1 cm x 1 cm
9 - QUANDO NÃO INDICADO, MEDIDAS EM METROS

CÓPIA DIGITAL VÁLIDA

Caso esse documento seja impresso, verificar a vigência na lista mestra.