


[illegible]



escala 1:25

VISTA EM PLANTA

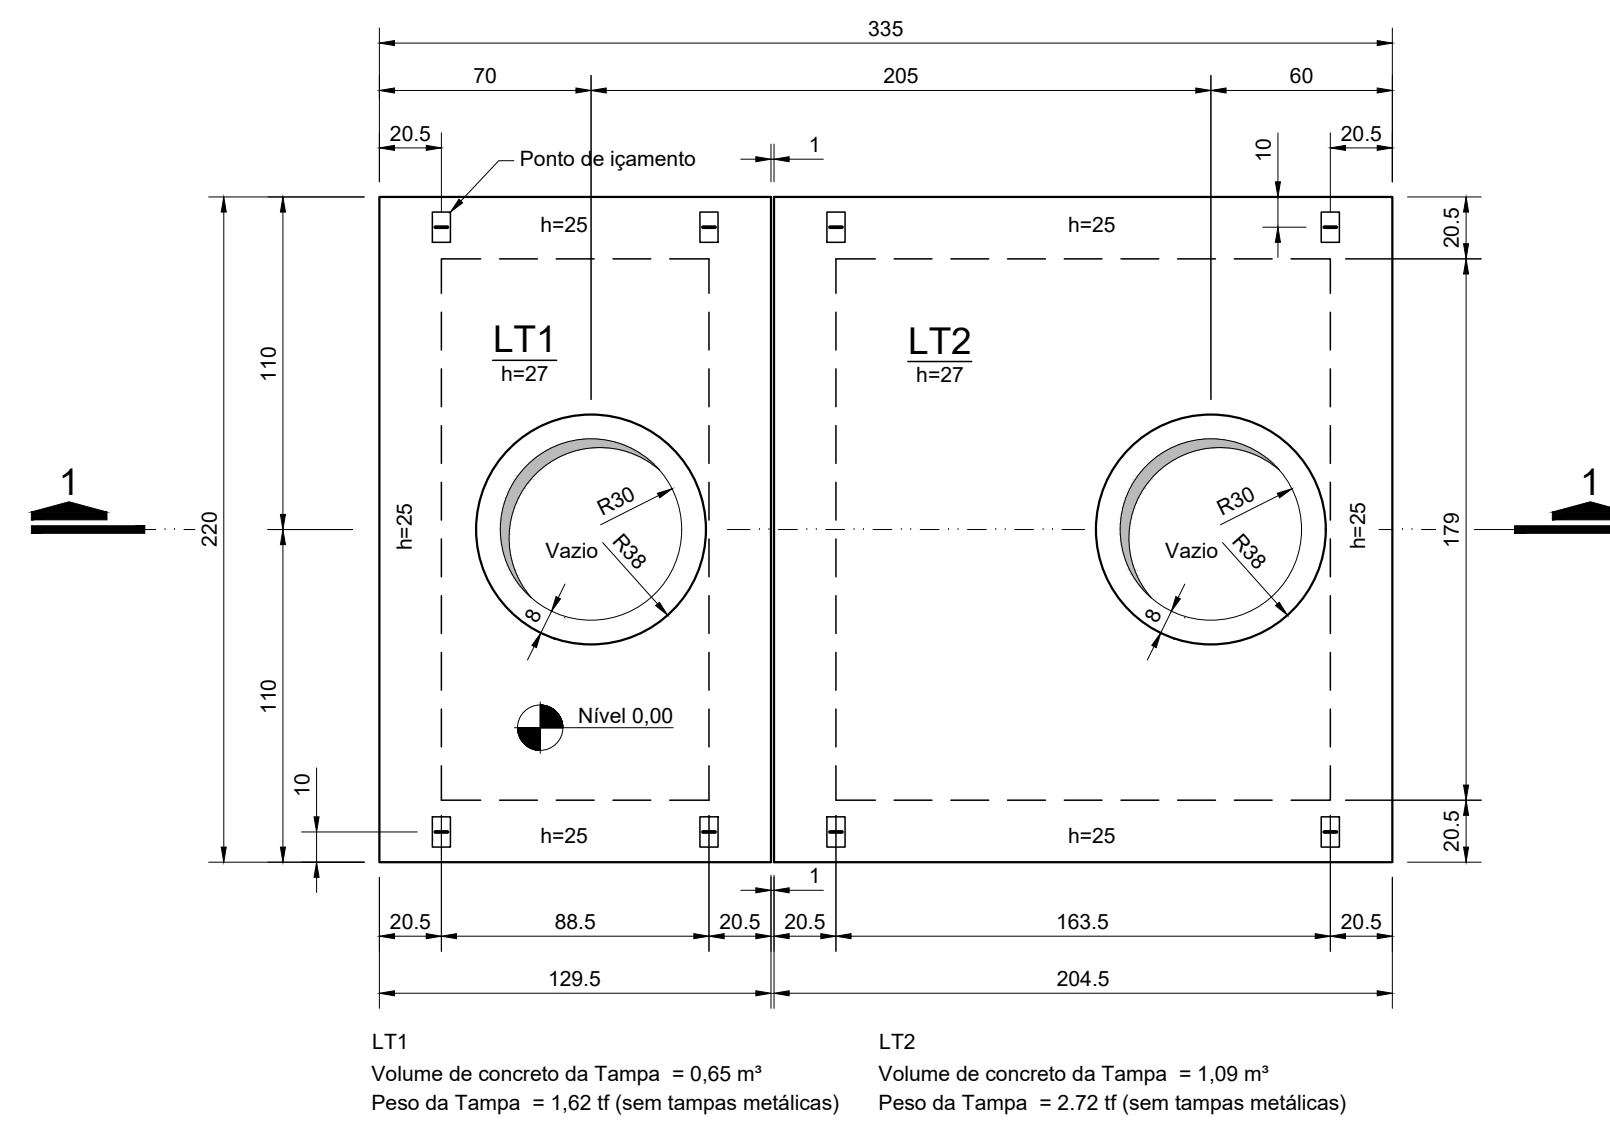


escala 1:25

TAMPA LT2

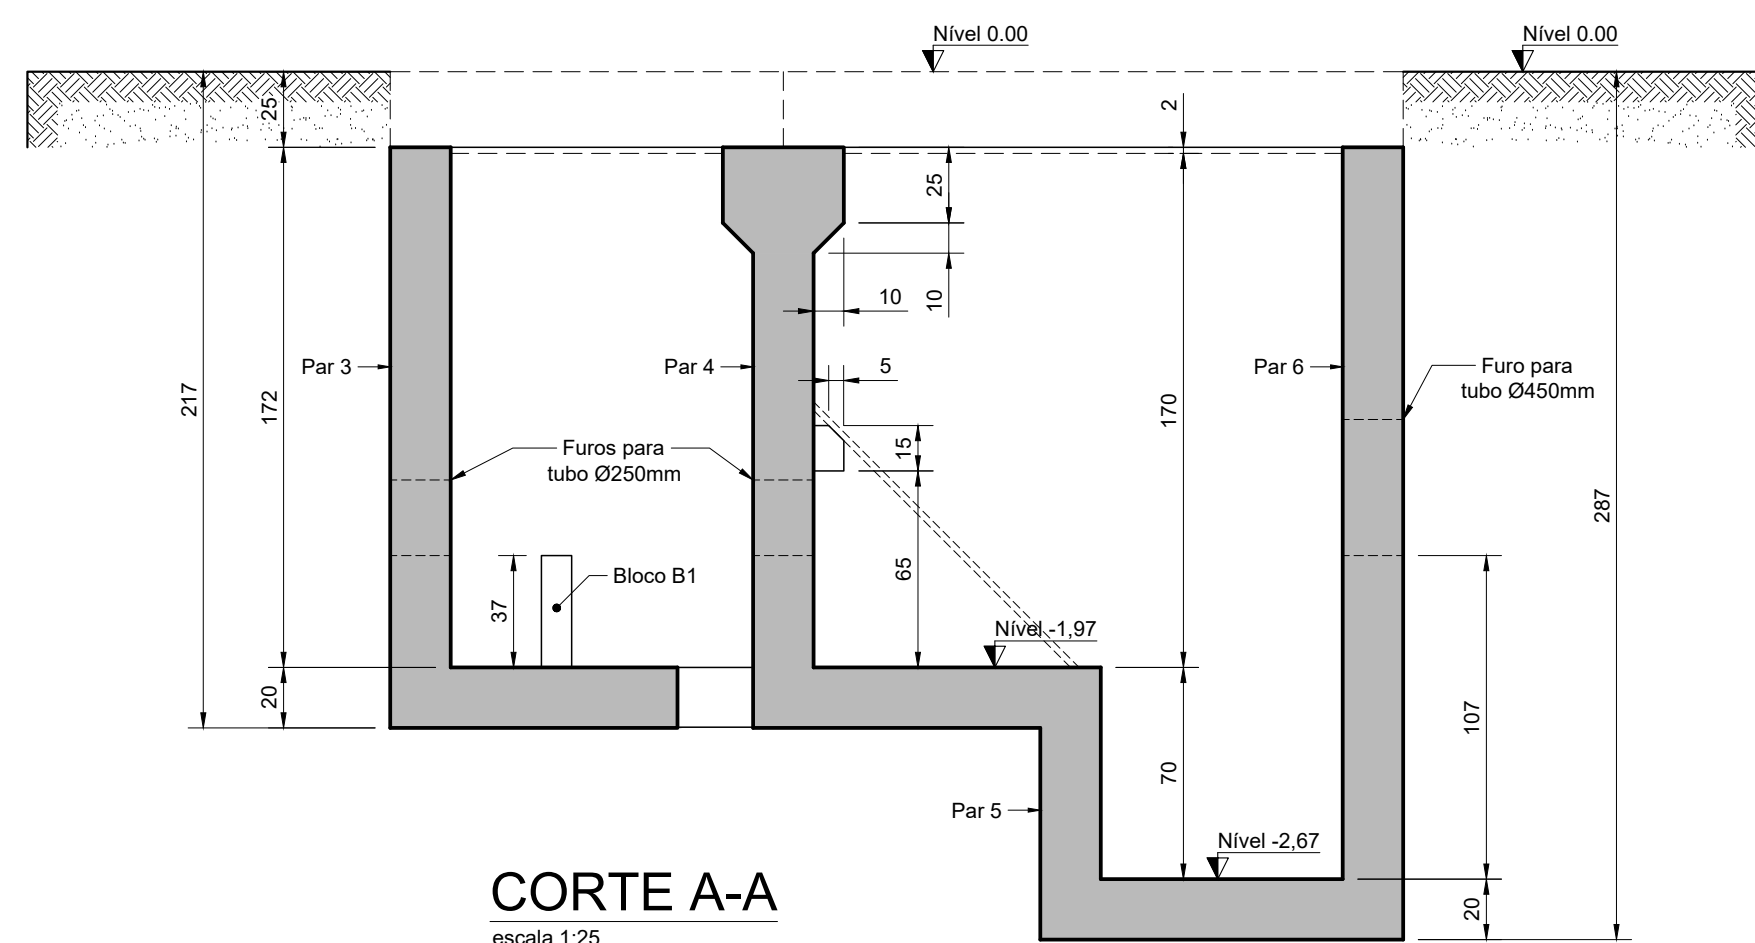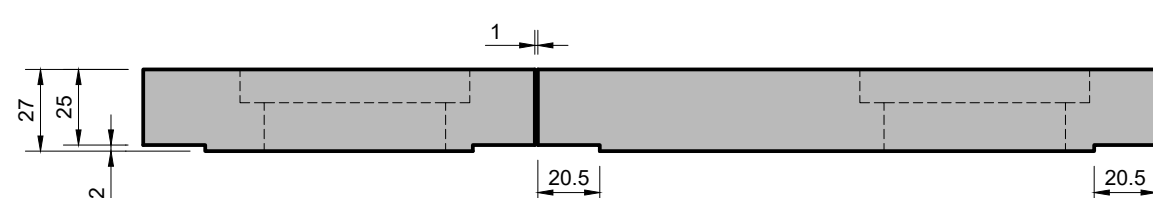


CORTE A-A
escala 1:25

TAMPA LT2

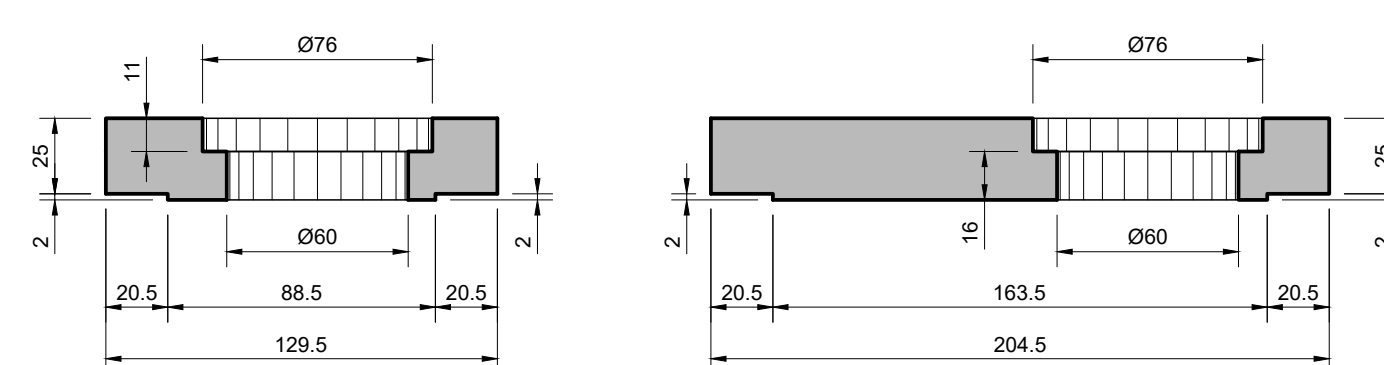

escala 1:25

escala 1:12.5

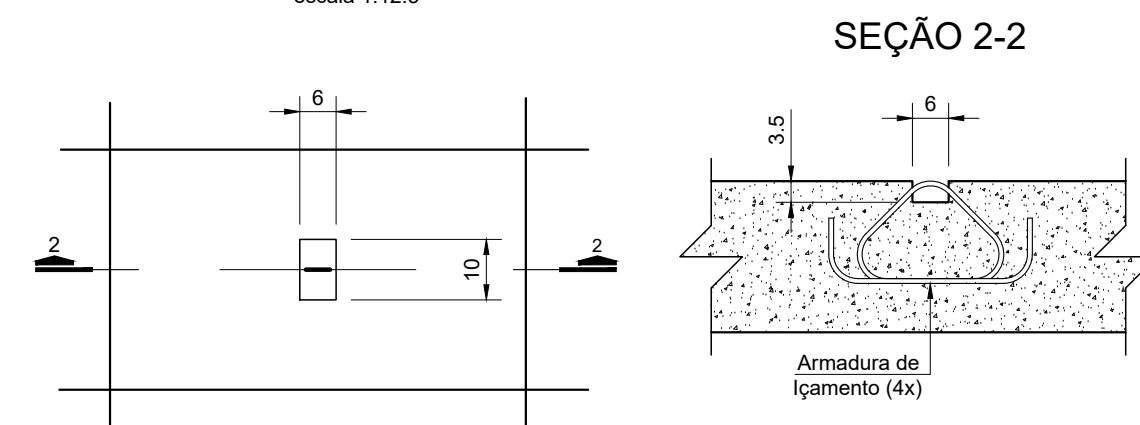

-Para execução, observar NBR 6118 / 2023 ; NBR 6122 / 2022, NBR 14931 / 2023 E NBR 12655 / 2022



LAJES	
VIGAS	
PILARES	
SAPATAS	
OUTROS	

[illegible]


Ramsés Maciel Netto
Engenheiro Civil - CREA 180626453-6
Rua das Pernambucanas 407, Sala 202- Graças - Recife (PE)
CEP 52011-010 Fones: (81) 3423-2564 / 9.9767-4163
ramsés.estruturas@gmail.com

Cliente	VIANA & MOURA CONSTRUÇÕES		
Serviço	SISTEMA DE ESGOTAMENTO SANITÁRIO - SES CONDOMÍNIO RECANTO DAS LARANJEIRAS - CARUARÚ - PE CAIXA DE MANOBRAS (GCF) - FORMAS GERAIS E CORTES		
Projeto Ramés	Pranchas do projeto Pranchas 01 a 08	Materiais Fck ≥ 30 MPa. Aço: CA-50/60 (A)	Esc. 1:25
Desenho Ramés	Data da emissão 23/10/2024	Desenho N. VM.25.2024 - C04.01/08	Rev. 0
Assinatura Digital	Vide Prancha 01		


escala 1:25

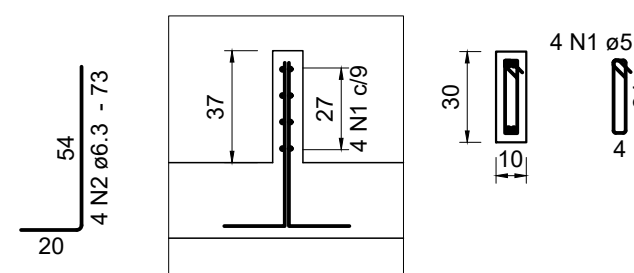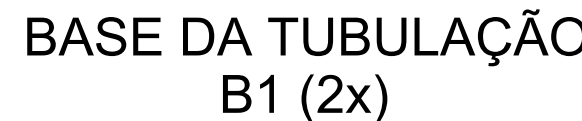


escala 1:25

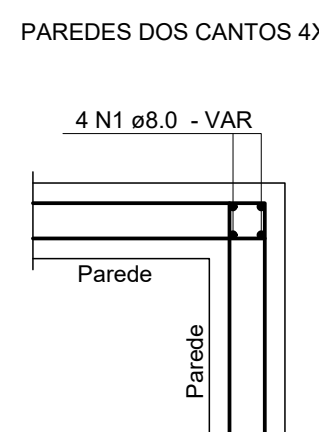


escala 1:25

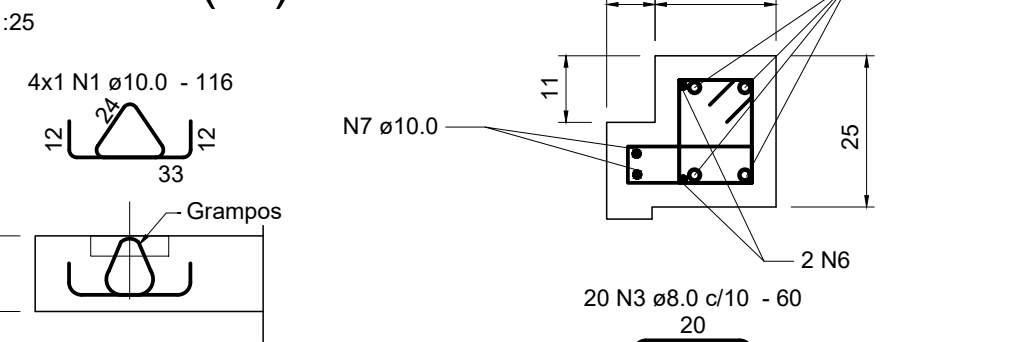


escala 1:25

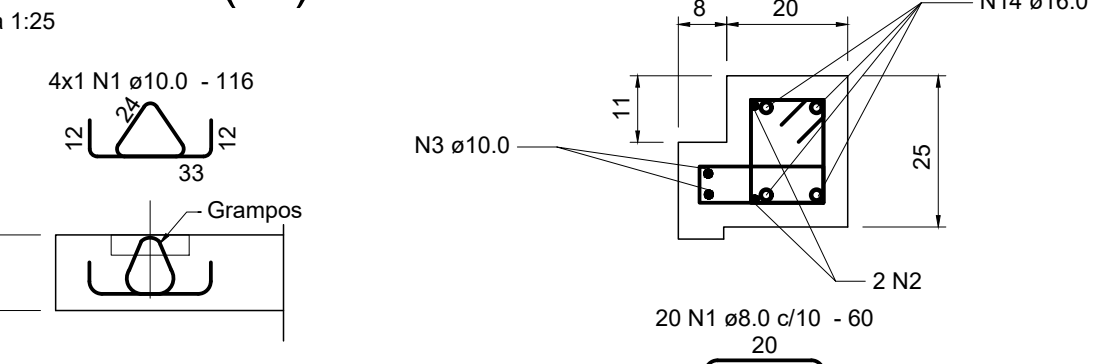


escala 1:25

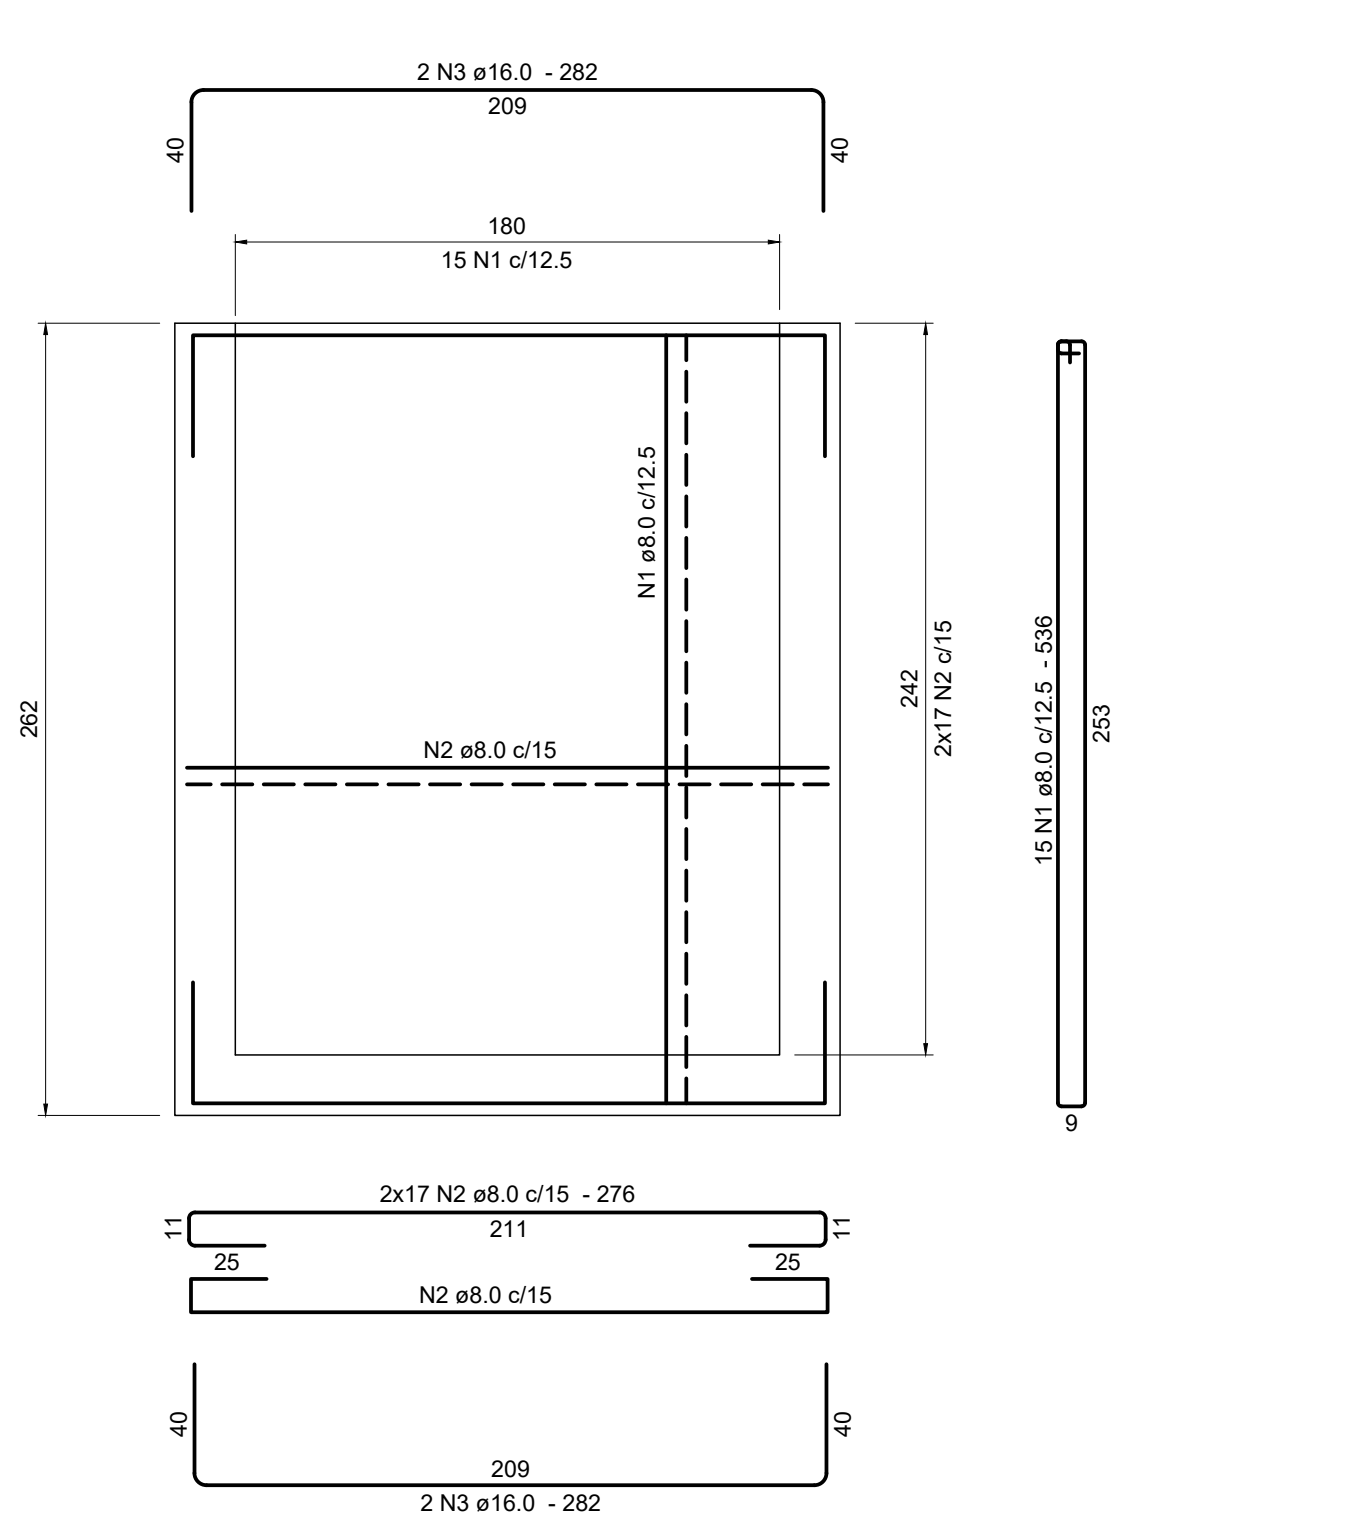


escala 1:15

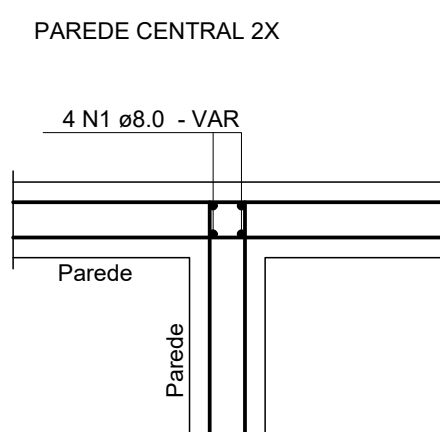

escala 1:2

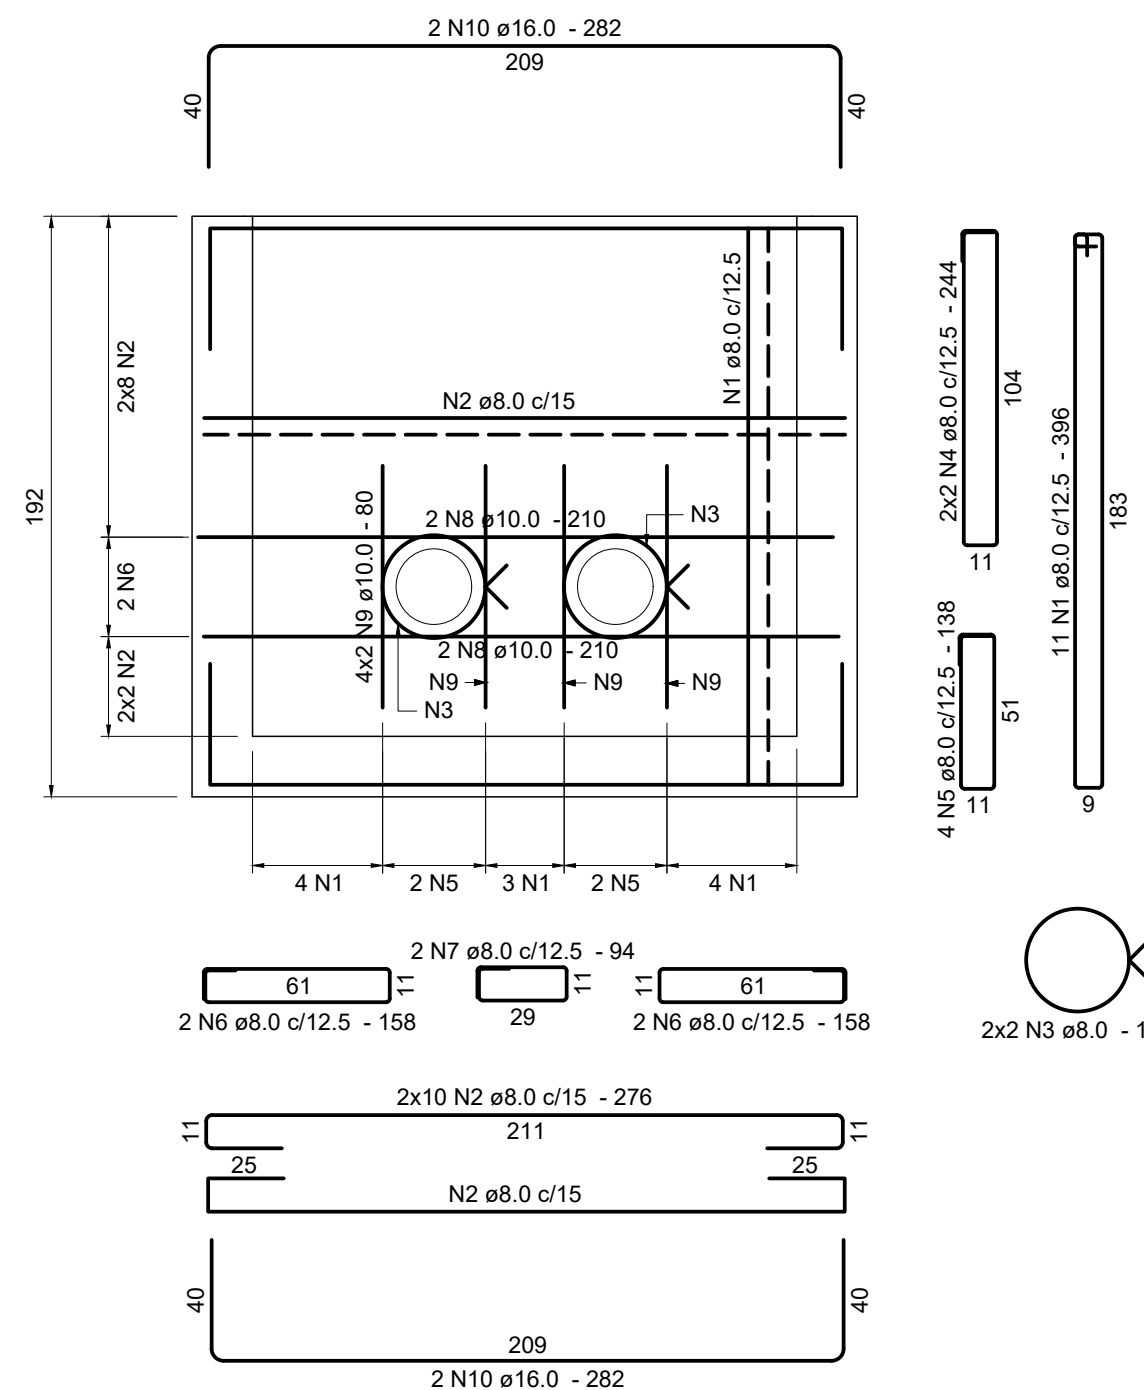

escala 1:25

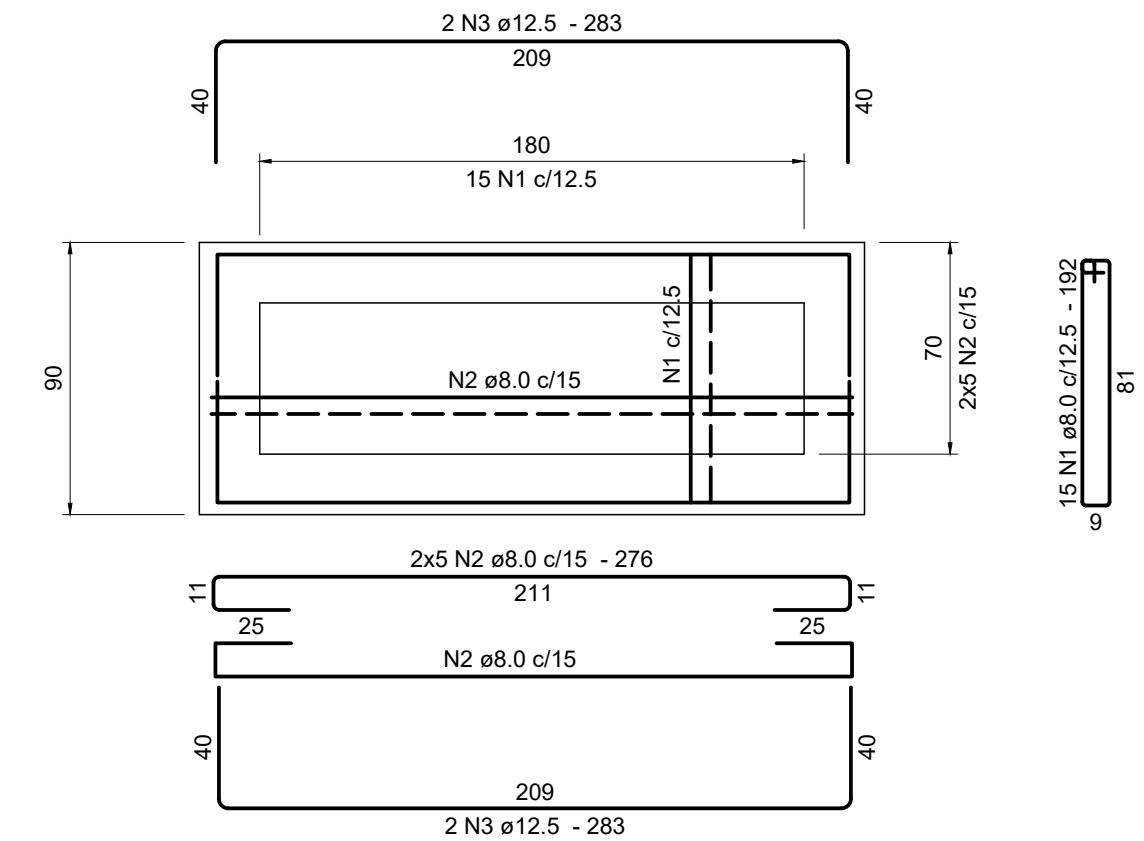

Relação do aço						
ELEMENTO	AÇO	N	DIAM (mm)	QUANT	C.LIMIT (cm)	C.TOTAL (cm)
Manobra 2x360	CASO 1	5,0	8	67	536	
	CASO 2	6,3	8	73	584	
4xCantos-1	CASO 1	1,0	16	VAR	VAR	VAR
	CASO 2	10,0	16	1856	1856	1856
4xCantos-2	CASO 1	1,0	16	116	1856	
	CASO 2	8,0	13	317	4121	
LF1At-305	CASO 1	8,0	20	305	6100	
	CASO 3	8,0	13	240	3120	
2xPar 1	CASO 4	8,0	2	197	394	
	CASO 5	8,0	2	120	240	
	CASO 6	8,0	20	428	4560	
	CASO 7	8,0	2	266	532	
	CASO 8	8,0	2	189	378	
	CASO 9	8,0	2	182	364	
	CASO 10	8,0	2	105	210	
	CASO 11	8,0	15	202	3030	
	CASO 12	8,0	15	125	1875	
	CASO 13	10,0	2	80	160	
	CASO 14	10,0	2	95	190	
	Par 3	CASO 1	8,0	8	396	12672
CASO 2		8,0	8	48	18768	
CASO 3		8,0	20	176	3520	
CASO 4		8,0	14	536	7504	
CASO 5		16,0	4	307	1958	
CASO 6		16,0	4	310	1240	
CASO 7		16,0	4	283	1132	
CASO 8		1,0	11	396	4356	
CASO 9		2,0	276	5520		
CASO 10		8,0	4	127	508	
CASO 11		8,0	4	244	976	
CASO 12		8,0	8	138	552	
Par 4	CASO 6	8,0	4	158	632	
	CASO 7	8,0	2	94	188	
	CASO 8	10,0	4	210	840	
	CASO 9	10,0	8	80	640	
	CASO 10	10,0	4	282	1128	
	CASO 11	5,0	45	45	45	
	CASO 12	5,0	3	91	273	
	CASO 3	6,3	30	82	2460	
	CASO 4	8,0	11	396	4356	
	CASO 5	8,0	20	276	5520	
	CASO 6	8,0	4	127	508	
	CASO 7	8,0	4	244	976	
Par 5	CASO 8	8,0	4	138	552	
	CASO 9	7,0	4	158	632	
	CASO 10	8,0	2	94	188	
	CASO 11	8,0	8	210	840	
	CASO 12	10,0	8	210	840	
	CASO 13	10,0	30	84	2520	
	CASO 14	16,0	4	282	1128	
	CASO 1	8,0	192	2880		
	CASO 2	8,0	10	276	2760	
	CASO 3	12,5	4	283	1132	
	CASO 4	8,0	536	536	536	
	CASO 5	2,0	34	276	9384	
Tampa LT1	CASO 3	16,0	4	282	1128	
	CASO 1	6,3	12	123	1476	
LT2	CASO 2	8,0	16	VAR	VAR	VAR
	CASO 3	8,0	20	60	1200	
	CASO 4	8,0	1	295	295	
	CASO 5	5,0	1	212	212	
	CASO 6	10,0	2	289	578	
	CASO 7	10,0	2	239	478	
	CASO 8	10,0	8	VAR	VAR	VAR
	CASO 9	10,0	12	202	2424	
	CASO 10	10,0	8	VAR	VAR	VAR
	CASO 11	12,5	12	120	1440	
	CASO 12	12,5	6	140	840	
	LT2	CASO 13	16,0	8	120	860
CASO 14		16,0	8	112	1696	
CASO 1		8,0	20	60	1200	
CASO 2		2,0	2	289	578	
CASO 3		10,0	8	239	1912	
CASO 4		10,0	16	VAR	VAR	VAR
CASO 5		10,0	8	VAR	VAR	VAR
CASO 6		10,0	9	212	1908	
LT2	CASO 7	10,0	18	2376	198	
	CASO 8	9,125	4	120	480	
	CASO 9	12,5	9	291	2619	
	CASO 10	12,5	12	275	3300	
	CASO 11	16,0	8	150	1500	
	CASO 12	16,0	8	112	1696	
	CASO 13	16,0	8	112	1696	
	CASO 14	16,0	8	112	1696	

Resumo do aço			
AÇO	DIAM (mm)	C.TOTAL (m)	PESO (kg)
CA50	6.3	45.2	11.1
	8.0	1274.2	502.8
	10.0	261	160.9
	12.5	97	93.4
	16.0	132.6	209.2
CA60	5.0	12.2	1.9
PESO TOTAL (kg)			
CA50	977.3		
CA60	1.9		

NOTAS:

Materiais:

- Cimento Portland CIII com consumo mínimo de 320 kgf/m³
- Slump (abatimento) = 60mm (+/- 10mm)
- Concreto estrutural classe C-30
- Fator água cimento <= 0,55
- Vida útil de projeto 50 anos
- Aço CA-50 / 60 (A)

Dados para dimensionamento:

- Classe de agressividade ambiental CAA III (forte)
- Tensão admissível do terreno de fundação $\sigma_t = 0,00 \text{ MPa}$
- Cobrimento nominal das armaduras: $C_n = 4,0 \text{ cm}$

Recomendações:

- Concreto magro sob as lajes de fundo (e=5cm)
- As formas devem obedecer às recomendações da NBR 14931 / 2003 (ver itens 11 e 12 - Cura, retirada foras e escoramentos respectivamente), como valores mínimos, as remoções devem aguardar 14 dias para remoção total.
- Processo de cura das superfícies expostas, devem perdurar por, no mínimo, 7 dias
- Caso haja necessidade de execução de furos nas paredes já concretadas para passagem de tubulação, estes devem ser executados com equipamentos de baixo impacto, a recomposição deverá ser feita com grout não retrátil e a vedação da tubulação com fita hidró expansiva em volta do tubo.

Controle e referências:

-Projeto de acordo com a norma brasileira NBR 6118 / 2023, NBR 6122 / 2022 E NBR 7188 / 2024

-Para execução, observar NBR 6118 / 2023 ; NBR 6122 / 2022, NBR 14931 / 2023 E NBR 12655 / 2022

ELEMENTOS CONSTANTES NESTE DESENHO	
LAJES	
VIGAS	
PILARES	
SAPATAS	
OUTROS	

[illegible]

CÓPIA DIGITAL VÁLIDA




Ramsés Maciel Netto
Engenheiro Civil - CREA 180626453-6
Rua das Pernambuco 407, Sala 202- Graças - Recife (PE)
CEP 52011-010 Fones: (81) 3423-2564 / 9.9767-4163
ramses.estruturas@gmail.com

Cliente	VIANA & MOURA CONSTRUÇÕES
Serviço	SISTEMA DE ESGOTAMENTO SANITÁRIO - SES CONDOMÍNIO RECANTO DAS LARANJEIRAS - CARUARÚ - PE CAIXA DE MANOBRAS (GCF) - ARMAÇÕES GERAIS

Projeto Ramés	Pranchas do projeto Pranchas 01 a 08	Materiais Fck ≥ 30 MPa. Aço: CA-50/60 (A)	Escala 1:2
Desenho Ramés	Data da emissão 23/10/2024		
Assinatura Digital	Vide Prancha 01	Desenho N. VM.25.2024 - C04.02/08	Revisão C

DESCARGA SIMPLES

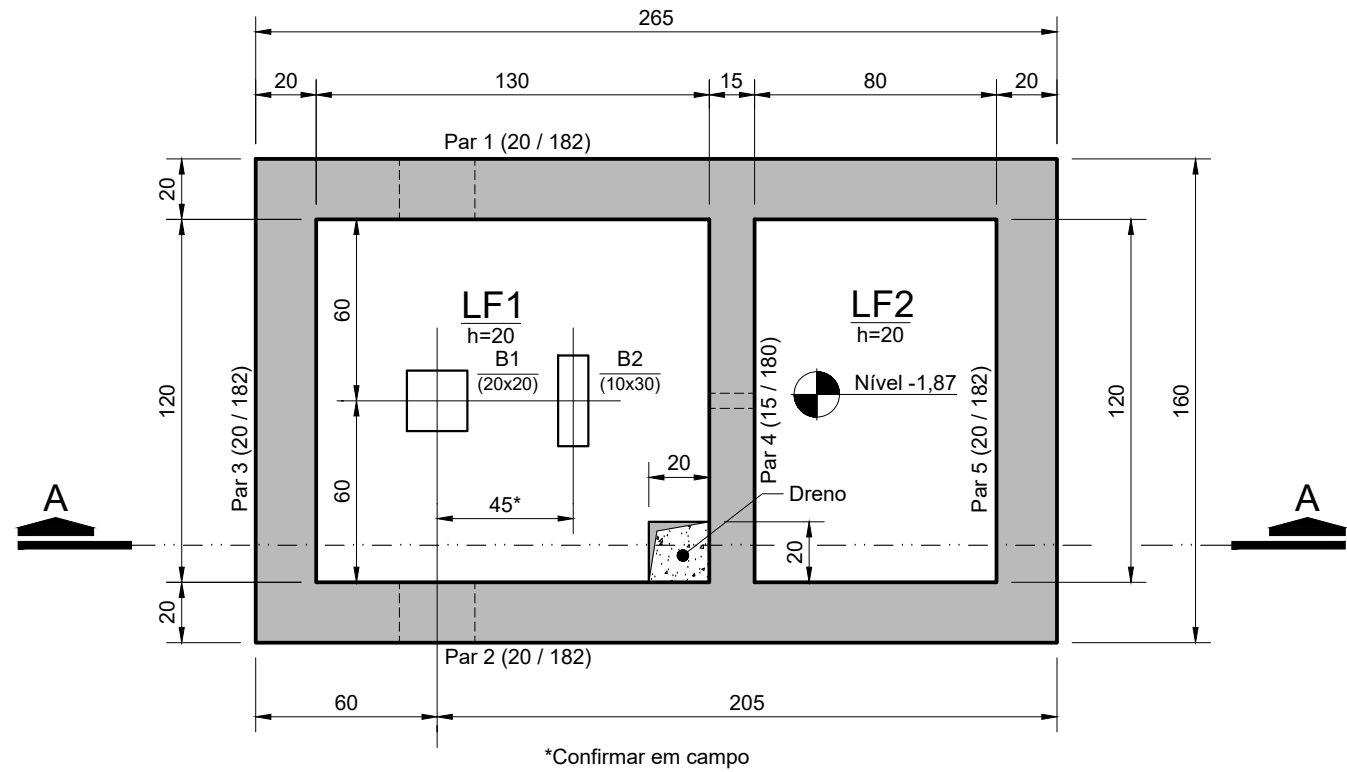


FORMA DA LAJE DE FUNDO - Nível -1,87

escala 1:25

DESCARGA SIMPLES

VISTA EM PLANTA

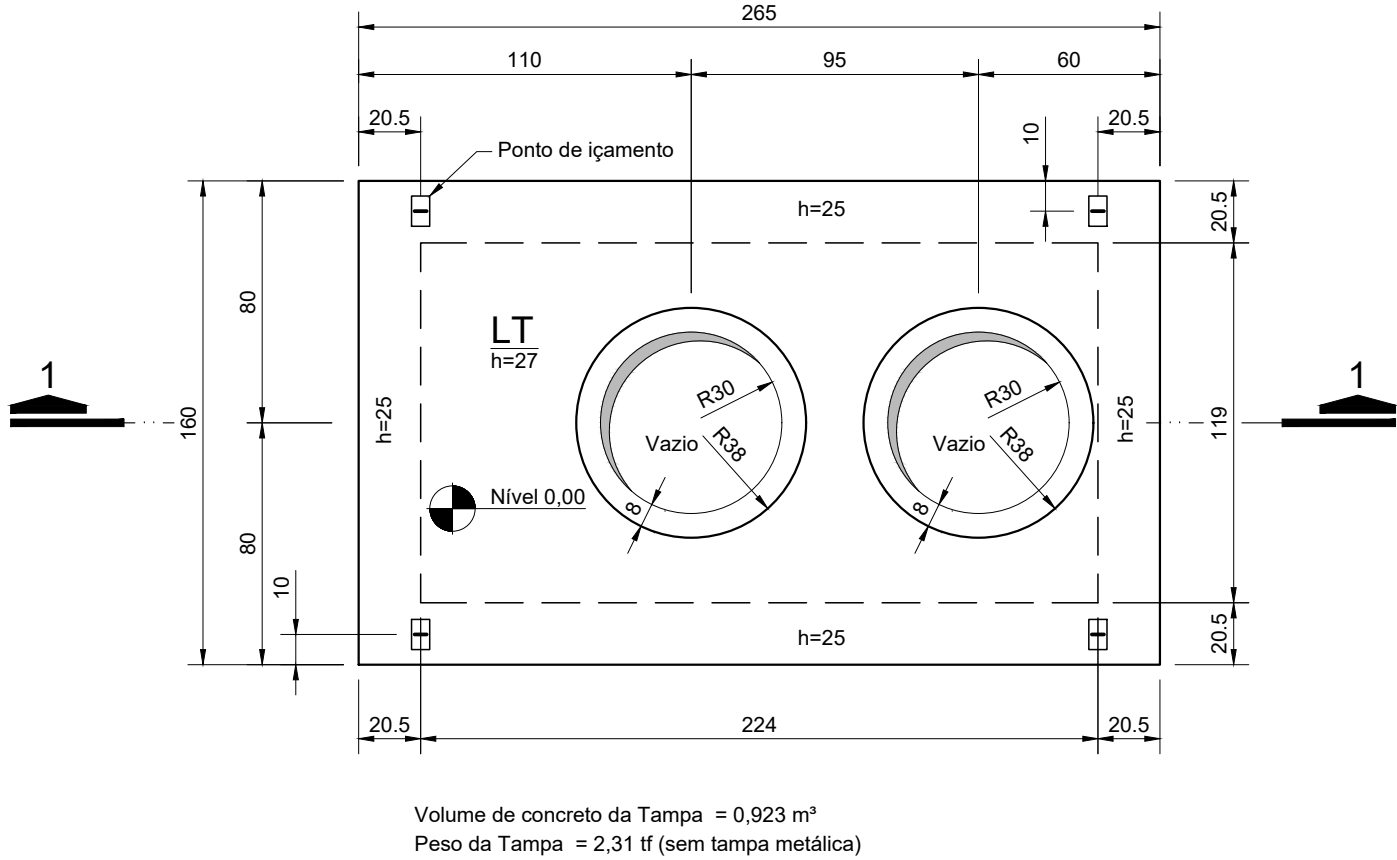

FORMA DA LAJE DE TAMPA - Nível 0,00

escala 1:25

NOTAS:

Materiais:

- Cimento Portland CP11 com consumo mínimo de 320 kgf/m³
- Slump (abatimento) = 60mm (+/- 10mm)
- Concreto estrutural classe C-30
- Fator água cimento <= 0,55
- Vida útil de projeto 50 anos
- Aço CA-50 / 60 (A)

Dados para dimensionamento:

- Classe de agressividade ambiental CAA III (forte)
- Tensão admissível do terreno de fundação St>=0.20 MPa

Lajes e paredes:

- Máximas com espessuras indicadas

Recomendações:

- Concreto magro sob as lajes de fundo com espessura de 5cm
- Ratificar no campo o posicionamento dos furos para a passagem das tubulações
- Os furos previamente indicados neste projeto, deverão ter armadura de reforço previamente executadas conforme detalhado na prancha de armação.
- A dimensão máxima do agregado gráúdo deverá ser de 25mm para facilitar a concretagem em regiões densamente armadas.
- As formas, adensamento e cura, devem obedecer às recomendações da NBR 14931 / 2004 (ver item 10.1 e 10.2)
- Para Impermeabilização das faces expostas dos elementos em contato com o solo, aplicar em toda superfície, impermeabilizante asfáltico para concreto (Igol S da Sika) ou produto similar.

Quantitativos:

- Volume de concreto C-30 da caixa = 3,64 m³
- Volume de concreto C-30 da tampa = 0,923 m³
- Peso de aço CA-50/60 = 556,1 kgf (sem perdas)

Controle e referências:

- Projeto de acordo com a norma brasileira NBR 6118 / 2023, NBR 6122 / 2022 E NBR 7188 / 2024
- Para execução, observar NBR 6118 / 2023 ; NBR 6122 / 2022, NBR 14931 / 2023 E NBR 12655 / 2022

ELEMENTOS CONSTANTES NESTE DESENHO

LAJES	
VIGAS	
PILARES	
SAPATAS	
OUTROS	

Revisões	Discriminação	Data	Verif.

CÓPIA DIGITAL VÁLIDA




Ramsés Maciel Netto
Engenheiro Civil - CREA 180626453-6
Rua das Pernambuco 407, Sala 202- Graças - Recife (PE)
CEP 52011-010 Fones: (81) 3423-2564 / 9.9767-4163
ramses.estruturas@gmail.com

Cliente	VIANA & MOURA CONSTRUÇÕES
Serviço	SISTEMA DE ESGOTAMENTO SANITÁRIO - SES CONDOMÍNIO RECANTO DAS LARANJEIRAS - CARUARÚ - PE CAIXA DE DESCARGA SIMPLES - FORMAS GERAIS E CORTES

Projeto Ramsés	Pranchas do projeto Pranchas 01 a 08	Materiais Fck >= 30 MPa. Aço: CA-50/60 (A)	Esc. 1:25
Desenho Ramsés	Data da emissão 23/10/2024	Desenho N. VM.25.2024 - C04.03/08	Rev. 0
Assinatura Digital	Vide Prancha 01		

TAMPA LT

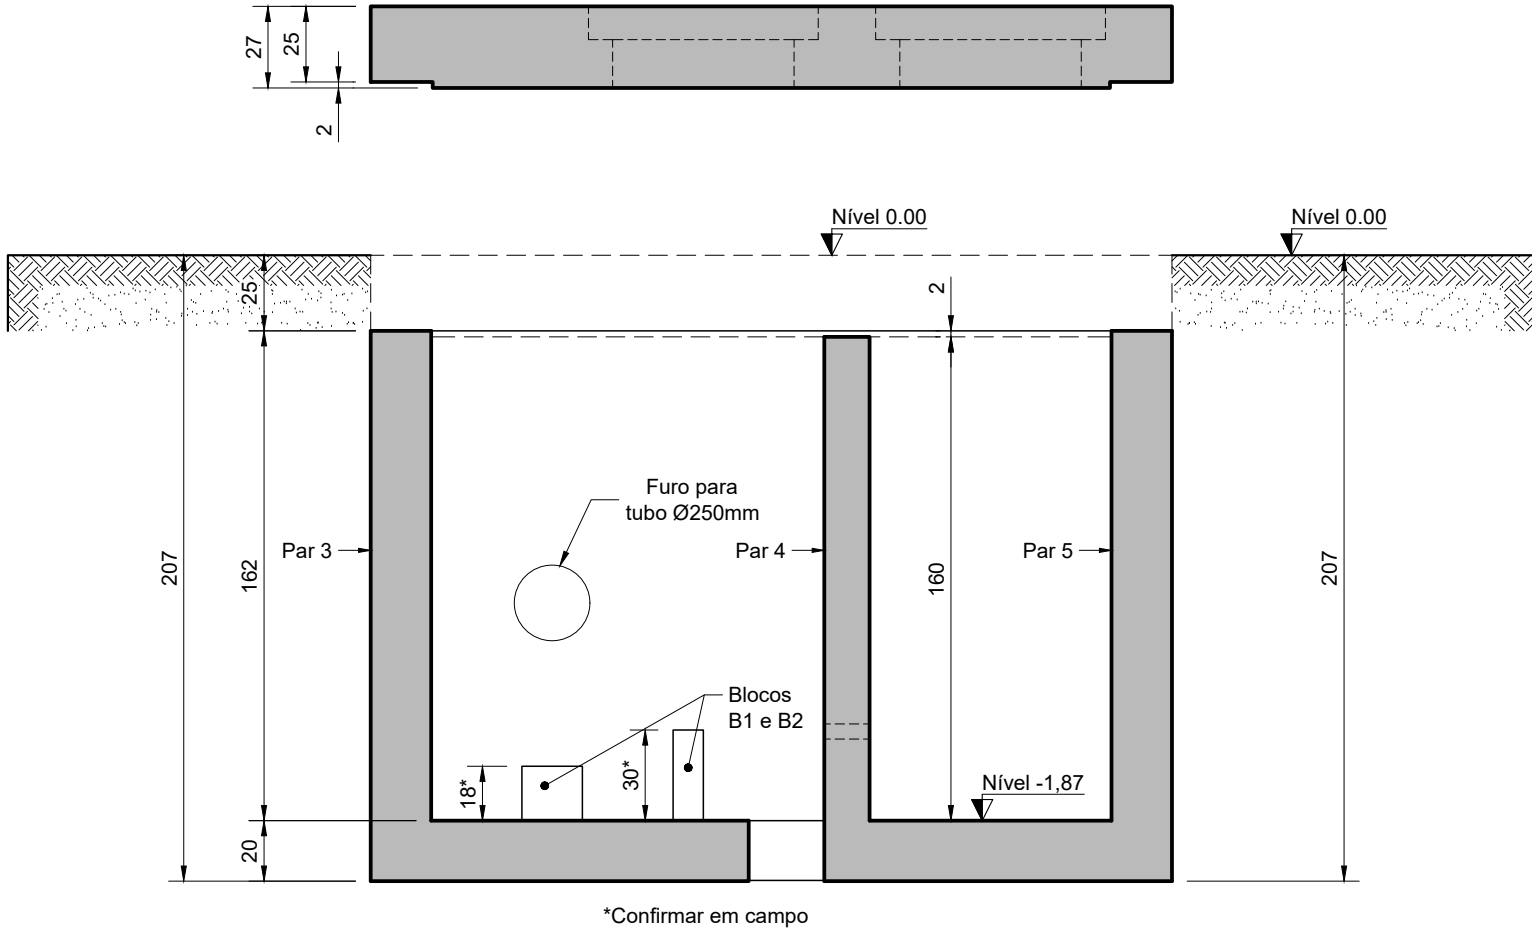

CORTE A-A

escala 1:25


SEÇÃO 1-1

escala 1:25

DETALHE - IÇAMENTO (4x)

escala 1:12.5

SEÇÃO 2-2

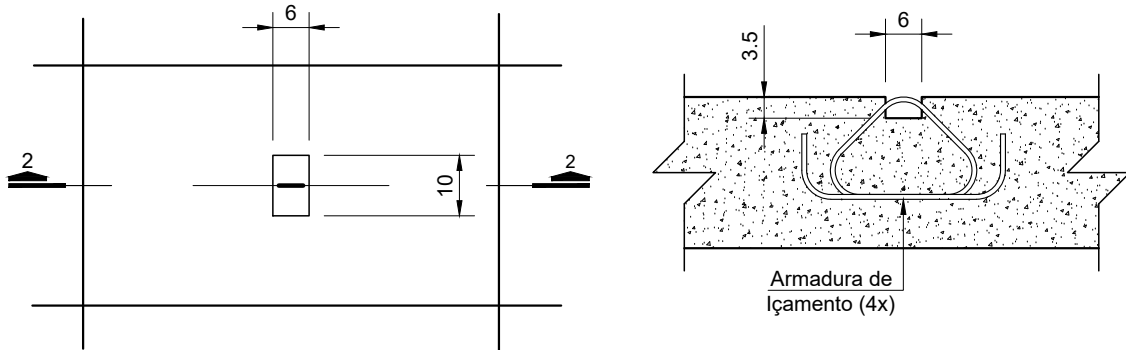

LAJES DE FUNDO LF1 E LF2

escala 1:25

PAREDES Par 1 = Par 2 (2x)

escala 1:25

ARMADURA DOS CANTOS

escala 1:15

PAREDE Par 3

escala 1:25

PAREDE Par 4

escala 1:25

ARMADURA DOS ENCONTROS

escala 1:15

ARMAÇÃO DA LAJE DE TAMPA - LT1

escala 1:25

DETALHE DAS ABERTURAS (Ø60cm) 2x

lçamento 4x

escala 1:25

BASES PARA TUBULAÇÃO B1 E B2

Relação do aço

ELEMENTO	AÇO	N	DIAM (mm)	QUANT	C.UNIT (cm)	C.TOTAL (cm)
Bases	CA60	1	5.0	3	67	201
	CA60	2	5.0	2	67	134
	CA50	3	6.3	4	61	244
	CA50	4	6.3	4	49	196
	CA50	1	8.0	16	172	2752
	CA50	1	8.0	8	172	1376
	CA50	1	10.0	16	116	1856
	CA50	1	8.0	8	347	2776
	CA50	2	8.0	16	246	3936
	CA50	3	8.0	8	270	2160
	CA50	4	8.0	2	197	394
	CA50	5	8.0	2	120	240
	CA50	6	8.0	18	169	3042
	CA50	7	8.0	2	206	412
	CA50	8	8.0	2	129	258
	CA50	9	8.0	2	212	424
LT1	CA50	10	8.0	2	135	270
	CA50	11	10.0	2	110	220
	CA50	12	10.0	2	80	160
	CA50	1	8.0	40	60	2400
	CA50	2	10.0	4	289	1156
	CA50	3	10.0	4	239	956
	CA50	4	10.0	32	VAR	VAR
	CA50	5	10.0	8	VAR	VAR
	CA50	6	10.0	7	152	1064
	CA50	7	10.0	8	VAR	VAR
	CA50	8	10.0	8	VAR	VAR
	CA50	9	10.0	6	337	2022
	CA50	10	10.0	6	257	1542
	CA50	11	12.5	8	125	1000
	CA50	12	12.5	16	120	1920
	CA50	13	12.5	7	231	1617
2xPar 1	CA50	14	12.5	4	85	340
	CA50	15	16.0	8	255	2040
	CA50	16	16.0	8	152	1216
	CA50	1	8.0	32	376	12032
	CA50	2	8.0	36	321	11556
	CA50	3	8.0	4	180	720
	CA50	4	8.0	4	176	704
	CA50	5	8.0	4	130	520
	CA50	6	8.0	8	249	1992
	CA50	7	8.0	4	122	488
	CA50	8	10.0	16	80	1280
	CA50	9	16.0	8	327	2616
	CA50	1	8.0	10	376	3760
	CA50	2	8.0	22	216	4752
	CA50	3	16.0	4	222	888
	Par 3	CA50	1	6.3	22	205
CA50		2	6.3	10	370	3700
CA50		3	10.0	4	224	896
CA50		1	8.0	10	376	3760
Par 4	CA50	2	8.0	22	216	4752
	CA50	3	16.0	4	222	888
Par 5	CA50	1	6.3	22	205	4510
	CA50	2	6.3	10	370	3700
	CA50	3	10.0	4	224	896
	CA50	1	8.0	10	376	3760

Resumo do aço

AÇO	DIAM (mm)	C.TOTAL (m)	PESO (kg)
CA50	6.3	86.5	21.2
	8.0	654.8	258.4
	10.0	175.9	108.4
	12.5	48.8	47
	16.0	76.5	120.7
CA60	5.0	3.4	0.5
PESO TOTAL (kg)			
CA50	555.6		
CA60	0.5		

NOTAS:

Materiais:

- Cimento Portland CPIII com consumo mínimo de 320 kgf/m³
- Slump (abatimento) = 60mm (+/- 10mm)
- Concreto estrutural classe C-30
- Fator água cimento <= 0,55
- Vida útil de projeto 50 anos
- Aço CA-50 / 60 (A)

Dados para dimensionamento:

- Classe de agressividade ambiental CAA III (forte)
- Tensão admissível do terreno de fundação St>=0.20 MPa
- Cobrimento nominal das armaduras: Cn=4,0cm

Recomendações:

- Concreto magro sob as lajes de fundo (e=5cm)
- As formas devem obedecer às recomendações da NBR 14931 / 2023 (ver itens 11 e 12 - Cura, retirada de formas e escoramentos respectivamente), como valores mínimos, as remoções devem aguardar 14 dias para remoção total.
- Processo de cura das superfícies expostas, devem perdurar por, no mínimo, 7 dias
- Caso haja necessidade de execução de furos nas paredes já concretadas para passagem de tubulação, estes devem ser executados com equipamentos de baixo impacto, a recomposição deverá ser feita com graute não retrátil e a vedação da tubulação com fita hidro expansiva em volta do tubo.

Controle e referências:

- Projeto de acordo com a norma brasileira NBR 6118 / 2023, NBR 6122 / 2022 E NBR 7188 / 2024
- Para execução, observar NBR 6118 / 2023 ; NBR 6122 / 2022, NBR 14931 / 2023 E NBR 12655 / 2022

ELEMENTOS CONSTANTES NESTE DESENHO

LAJES	
VIGAS	
PILARES	
SAPATAS	
OUTROS	

Revisões

	Discriminação	Data	Verif.

CÓPIA DIGITAL VÁLIDA

Ramsés Maciel Netto

Engenheiro Civil - CREA 180626453-6

Rua das Pernambucanas 407, Sala 202- Graças - Recife (PE)

CEP 52011-010 Fones: (81) 3423-2564 / 9.9767-4163

rams.es.estruturas@gmail.com

Cliente

VIANA & MOURA CONSTRUÇÕES

Serviço

SISTEMA DE ESGOTAMENTO SANITÁRIO - SES CONDOMÍNIO RECANTO DAS LARANJEIRAS - CARUARÚ - PE CAIXA DE DESCARGA SIMPLES - ARMAÇÕES GERAIS

Projeto

Ramsés

Pranchas do projeto

Pranchas 01 a 08

Desenho

Ramsés

Data da emissão

23/10/2024

Assinatura

Digital

Vide Prancha 01

Materiais

Fck ≥ 30 MPa.

Aço: CA-50/60 (A)

Desenho N.

VM.25.2024 - C04.04/08

Esc.

1:25

Rev.

0

Technical drawing of a drainage system layout. The drawing shows two basins, LF1 and LF2, with various dimensions and labels.

Basin LF1:

- Dimensions: 140 (width) x 180 (depth).
- Labels: LF1, h=20, B1 (20x20), B2 (20x20), B3 (10x30).
- Distances: 50 (from left wall to B1), 5 (between B1 and B2), 55 (from left wall to B3), 20 (from bottom wall to B3).

Basin LF2:

- Dimensions: 140 (width) x 180 (depth).
- Labels: LF2, h=20, Nivel -1.87, Dreno.
- Distances: 20 (from bottom wall to Dreno).

Other Dimensions and Labels:

- Overall width: 275.
- Overall depth: 180.
- Distances from left wall: 20, 140, 15, 80, 20.
- Distances from bottom wall: 20, 50, 225.
- Labels: Par 1 (20 / 182), Par 2 (20 / 182), Par 3 (20 / 182), Par 4 (15 / 180).

escala 1:25

[illegible]

escala 1:25

-Projeto de acordo com a norma brasileira NBR 6118 / 2023, NBR 6122 / 2022 E NBR 7188 / 2024


-Para execução, observar NBR 6118 / 2023 ; NBR 6122 / 2022, NBR 14931 / 2023 E NBR 12655 / 2022

escala 1:25

escala 1:25


Projeto Ramšs		Pranchas do projeto Pranchas 01 a 08		Materiais Fck $\geq$ 30 MPa. Aço: CA-50/60 (A)		Esc. 1:25	
Desenho Ramšs		Data de emissão 23/10/2024		Desenho N. VM.25.2024 - C04.05/08		Rev. 0	
Assinatura Digital		Vide Prancha 01					

CAIXA PARA VENTOSA

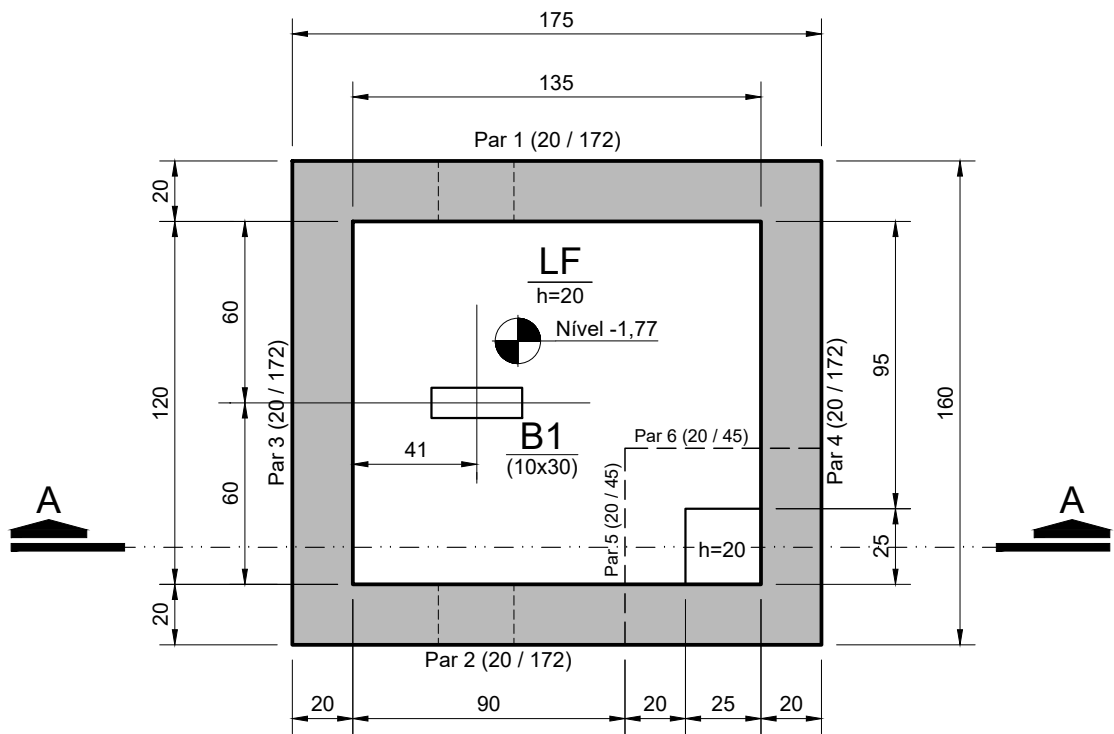

PLANTA BAIXA - Nível -1,77
escala 1:25

CAIXA PARA VENTOSA

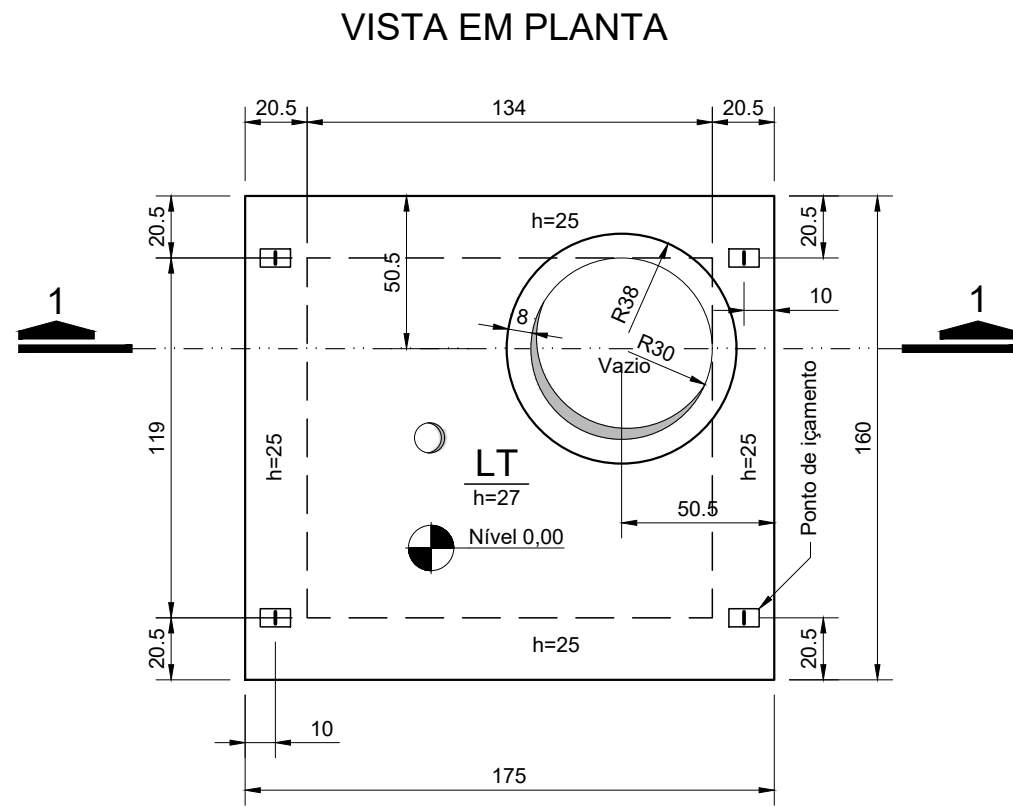

VISTA SUPERIOR
escala 1:25

NOTAS:

- Materiais:**
- Cimento Portland CPIII com consumo mínimo de 320 kgf/m³
 - Slump (abatimento) = 60mm (+/- 10mm)
 - Concreto estrutural classe C-30
 - Fator água cimento <= 0,55
 - Vida útil de projeto 50 anos
 - Aço CA-50 / 60 (A)

- Dados para dimensionamento:**
- Classe de agressividade ambiental CAA III (forte)
 - Tensão admissível do terreno de fundação St>=0.20 MPa

- Lajes e paredes:**
- Maciças com espessuras indicadas

- Recomendações:**
- Concreto magro sob as lajes de fundo com espessura de 5cm
 - Ratificar no campo o posicionamento dos furos para a passagem das tubulações
 - Os furos previamente indicados neste projeto, deverão ter armadura de reforço previamente executadas conforme detalhado na prancha de armação.
 - A dimensão máxima do agregado gráúdo deverá ser de 25mm para facilitar a concretagem em regiões densamente armadas.
 - As formas, adensamento e cura, devem obedecer às recomendações da NBR 14931 / 2004 (ver item 10.1 e 10.2)
 - Para Impermeabilização das faces expostas dos elementos em contato com o solo, aplicar em toda superfície, impermeabilizante asfáltico para concreto (Igol S da Sika) ou produto similar.

- Quantitativos:**
- Volume de concreto C-30 da caixa = 2,44 m³
 - Volume de concreto C-30 da tampa = 0,64 m³
 - Peso de aço CA-50/60 = 328,4 kgf (sem perdas)

- Controle e referências:**
- Projeto de acordo com a norma brasileira NBR 6118 / 2023, NBR 6122 / 2022 E NBR 7188 / 2024
 - Para execução, observar NBR 6118 / 2023 ; NBR 6122 / 2022, NBR 14931 / 2023 E NBR 12655 / 2022

ELEMENTOS CONSTANTES NESTE DESENHO

LAJES	
VIGAS	
PILARES	
SAPATAS	
OUTROS	

Revisões	Discriminação	Data	Verif.





CÓPIA DIGITAL VÁLIDA



Ramsés Maciel Netto
Engenheiro Civil - CREA 180626453-6
Rua das Pernambucanas 407, Sala 202- Graças - Recife (PE)
CEP 52011-010 Fones: (81) 3423-2564 / 9.9767-4163
ramses.estruturas@gmail.com

Ciente	VIANA & MOURA CONSTRUÇÕES
Serviço	SISTEMA DE ESGOTAMENTO SANITÁRIO - SES CONDOMÍNIO RECANTO DAS LARANJEIRAS - CARUARÚ - PE CAIXA PARA VENTOSA - FORMAS GERAIS E CORTES

Projeto Ramsés	Pranchas do projeto Pranchas 01 a 08	Materiais Fck ≥ 30 MPa. Aço: CA-50/60 (A)	Esc. 1:25
Desenho Ramsés	Data da emissão 23/10/2024	Desenho N. VM.25.2024 - C04.07/08	Rev. 0
Assinatura Digital	Vide Prancha 01		

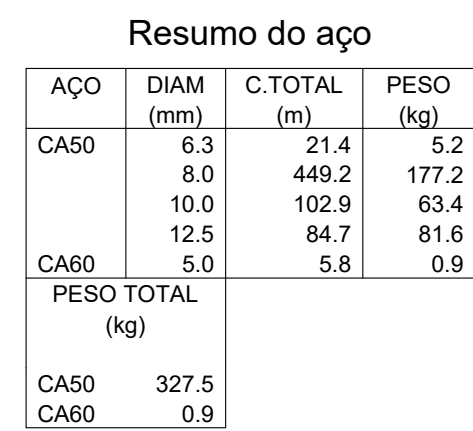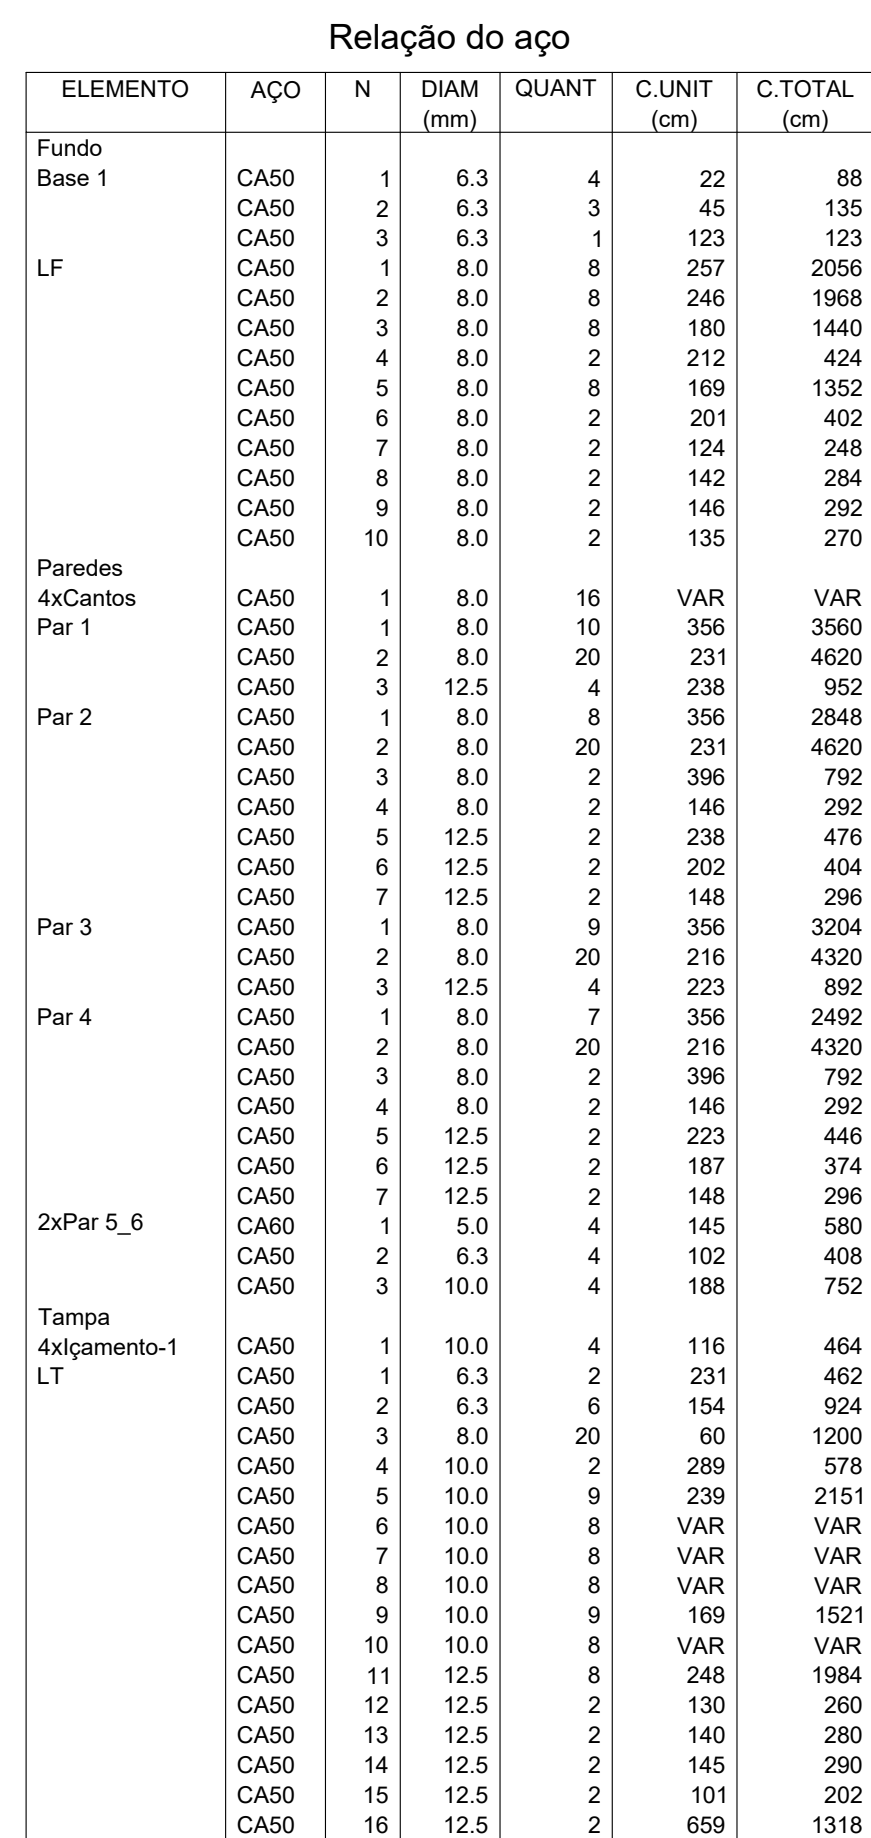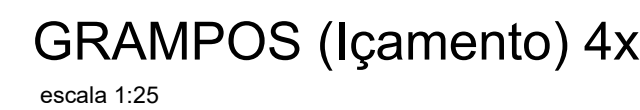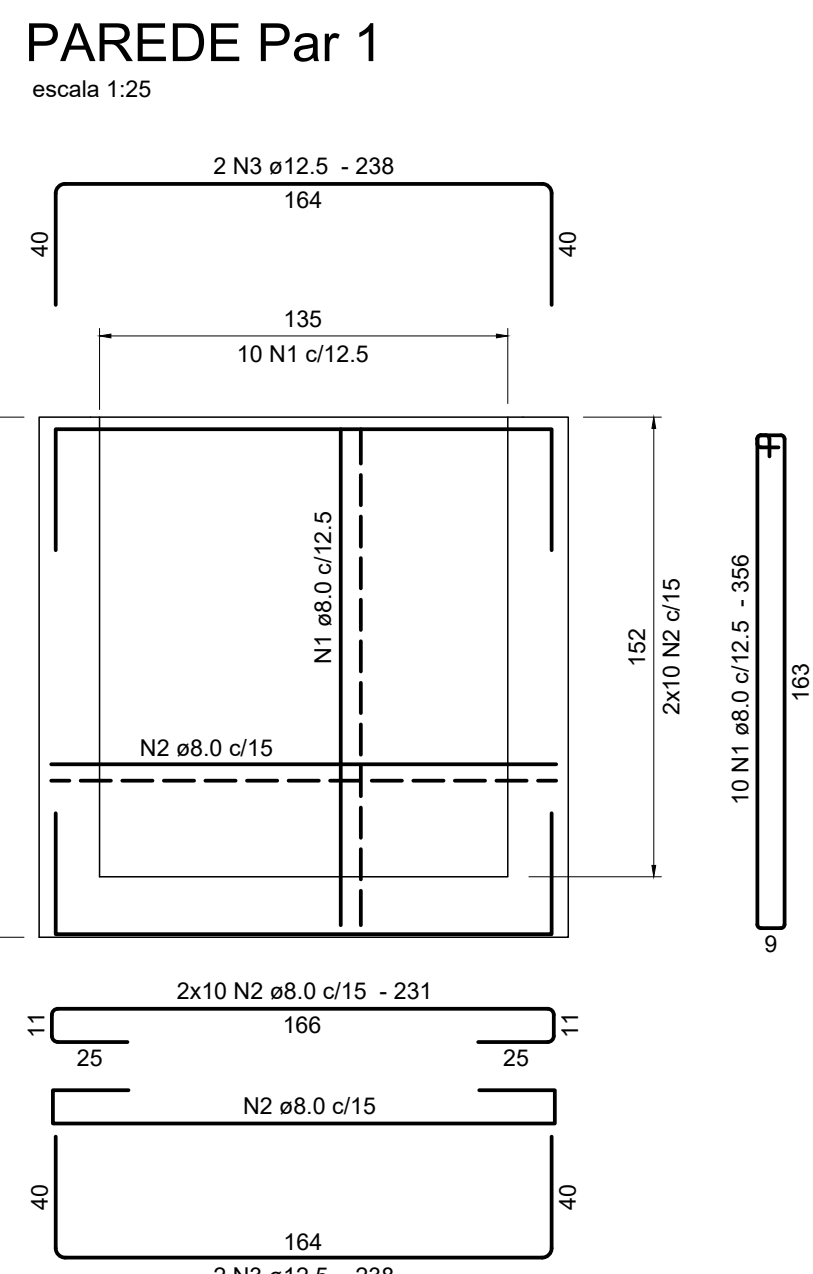

ELEMENTOS CONSTANTES NESTE DESENHO

LAJES	
VIGAS	
PILARES	
SAPATAS	
OUTROS	

[illegible]

CÓPIA DIGITAL VÁLIDA



Ramsés Maciel Netto
Engenheiro Civil - CREA 180626453-6
Rua das Pernambucanas 407, Sala 202- Graças - Recife (PE)
CEP 52011-010 Fones: (81) 3423-2564 / 9.9767-4163
ramses.estruturas@gmail.com

Cliente		VIANA & MOURA CONSTRUÇÕES	
Serviço			
SISTEMA DE ESGOTAMENTO SANITÁRIO - SES CONDOMÍNIO RECANTO DAS LARANJEIRAS - CARUARÚ - PE CAIXA PARA VENTOSA - ARMAÇENS GERAIS			
Projeto	Pranchas do projeto	Materiais	Esc.
Ramsés	Pranchas 01 a 08	Fck ≥ 30 MPa.	1:25
Desenho	Data de emissão	Aço: CA-50/60 (A)	
Ramsés	23/10/2024		
Assinatura	Vide Prancha 01	Desenho N.	Rev.
Digital		VM.25.2024 - C04.08/08	0